备注栏

设计单位 杭州园林设计院股份有限公司 HANGZHOU LANDSCAPE ARCHITECTURE DESIGN INSTITUTE CO.,LTD
建筑、风景园林甲级(A133031139) 城镇乡规、城市编制(142056)
市政乙级(A253011126) 文物保护工程勘察设计乙级(WHXS2300)
全国统一客服电话:400-8777-111 地址:浙江省杭州市拱墅区半山路98号 邮编:310007
电话:0571-85059111 传真:0571-85059000 网址:www.hzla.com.cn

建设单位	江苏茂源电气有限公司
工程总称	云创中心生产综合楼
子项名称	生产综合楼
图纸名称	图纸目录

	姓名	签名
审定		
审核		
项目负责人		
专业负责人		
设计		
制图		
校对		

执业专用章

按规定加盖

出图章

未盖出图专用章无效

工号	25-14	图别	建施
图号	m1	修改版次	
日期	2025.12		

杭州园林设计院股份有限公司

图 纸 目 录

建 设 单 位	江苏茂源电气有限公司	工 程 编 号	25-14
工 程 名 称	云创中心生产综合楼	图 纸 编 号	建施m1
子 项 名 称	生产综合楼		

图别图号	图　　名	图幅	备　　注
建施 m1	图纸目录	A1	
建施 00	总平面图	A1	
建施 01	建筑设计总说明	A1	
建施 02	工程做法	A1	
建施 03	绿色建筑节能设计专篇	A1	
建施 04	地下室平面图	A1	
建施 05	一层平面图	A1	
建施 06	二层平面图	A1	
建施 07	三层平面图	A1	
建施 08	四层平面图	A1	
建施 09	屋顶平面图	A1	
建施 10	1-1 剖面图	A1	
建施 10-2	2-2 剖面图	A1	
建施 11	立面图1	A1	
建施 12	立面图2	A1	
建施 13	立面图3	A1	
建施 14	立面图4	A1	
建施 15	坡道详图	A1	
建施 16	卫生间大样	A1	
建施 17	电梯井详图	A1	
建施 18	1#楼梯详图	A1	
建施 19	2#楼梯详图	A1	
建施 20	墙身大样	A1	
建施 21	门窗大样	A1	

完成日期2025年12月09日

专业会签栏	园林	给排水	电气	弱电
	建筑		暖通	

建 筑 设 计 说 明

专业会签栏 | 园林 建筑 | 结构 给排水 | 电气 暖通 | 弱电

一 工程概况

1. 工程名称：云创中心生产综合楼
2. 建设地点：江苏省东台市
3. 建设单位：江苏茂源电气有限公司
4. 工程设计编号：25-14
5. 总建筑面积：5074.12平方米　　建筑基底面积：1119.5平方米
6. 建筑高度：22.2米(室外地面至屋面板高度)
7. 建筑层数：地上4层/地下1层
8. 设计使用年限：50年
9. 耐火等级：一级
10. 屋面防水等级：Ⅱ级　　地下室防水等级：/级　　建筑分类：服务建筑　　建筑工程设计等级：二级
11. 本工程抗震设防烈度为7度，楼梯间和人流通道的填充墙，应采用钢丝网砂浆面层加强。(在不同材料交接处及暗埋管线出现细微裂缝时，应采用钢丝网砂浆面层加强。)

线出增加Φ0.9mm钢丝网，钢丝网与各种基体器装长度不小于150mm。)

二 设计依据

1. 业主提供的实测地形图及用地红线图。
2. 业主提供的相关设计要求及相关批复。
3. 国家及地方现行工程建设规范标准：《中华人民共和国城市规乡法》；《城市规划编制办法》；《屋面工程技术规范》GB50345-2012；《公共建筑节能设计标准》GB50189-2019；《建筑设计防火规范》GB50016--2014（2018版）；《民用建筑设计统一标准》GB50352-2019；《无障碍设计规范》GB50763-2012；《建筑内部装修设计防火规范》GB50222-2017；《屋面工程技术规范》GB50345-2012；《绿色建筑评价标准》GB/T50378-2014；《民用建筑热工设计规范》GB50176-2016；《建筑地面设计规范》GB50037-2013；《建筑玻璃应用技术规程》JGJ113-2015；《民用建筑工程室内环境污染控制标准》GB 50325-2020；《建筑用墙面涂料中有害物质限量》GB 18582-2020；《建筑外门窗气密、水密、抗风压性能检测方法》GB/T 7106-2019；其他现行的国家及地方有关建筑设计规范、规程和规定。

三 设计总则

1. 图中所注尺寸以毫米为单位，总平面图、标高以米为单位，所有尺寸均以标注为准，不应在图上度量。
2. 凡施工及验收规范已对建筑物各部位（如屋面、砌体、地面、门窗等）所用材料、规格、施工及验收要求等有规定者，本说明不再重复，均按有关现行规范执行。
3. 设计中采用的标准图、通用图，不论采用其局部节点或全部详图，均应按照该图集的图纸和说明等要求进行施工。
4. 所有与给排水、建筑电气、空调通风等专业有关的预埋件、预留孔洞，施工时必须与相关专业的图纸密切配合施工。
5. 工程采用玻璃幕墙、轻钢雨篷、装饰构架时，应由具备相应专业资质的单位承担制作与安装，并应得到本院认可，方能实施。该单位应负责所承担部分的结构安全，满足防水、密闭、耐火等各项性能要求。
6. 内装修部分：本工程验收后附室内外装修做法表规定的装修项目外，其余均由二次室内装修设计确定，不列入土建施工范围，二次装修必须符合消防安全要求，同时不能影响结构安全和损坏水电设施，各种装修材料的质量、颜色、规格尺寸等均应选好样品，经建设单位和设计单位协商认可后，才能订货、施工。

四 建筑物位置及设计标高

1. 建筑总体标高及定位以东台市建设局提供的测绘图为依据。基地周边道路标高以业主提供的测绘数据为准。
2. 本建筑物所在用地范围内的位置按总平面图及轴网定位图中所示坐标位置定位施工。
3. 所注±0.00标高相当于绝对标高4.20室内外高差为0.30米。
4. 本图纸除注明外所注地面、楼面、楼梯平台均为建筑完成面标高。屋面标高为结构板面标高(不包括找平层、保温层、防水层等)。门垛及窗洞口标高为结构窗洞口标高。
5. 门窗所注尺寸均为洞口尺寸；木门门扇（除图中标注外）位置与开启侧墙体内平；门垛除图中注明外均为砌体过120或240，混凝土墙柱边用表砖做120宽门垛，凡层中开设或者凝宽120的门或洞口在图中不再注明定位尺寸。

五 墙 体

1. 本工程均采用钢筋混凝土框架结构。
2. 局部地下室外墙为钢筋砼，采用自防水混凝土，抗渗等级详结施，具体防水做法详室内外装修做法表。地下室内隔墙采用200厚B07级砂加气。
3. ±0.000以上的墙体：

1)外墙、内墙均采用B07级砂加气。

2)外墙采用外保温做法，保温材料采用无机保温浆料，具体见<节能计算表>。

3)B07级砂加气具体构造措施及施工做法需满足国家及地方相关规范

4)厨房、卫生间等有水房间均应作墙面防水处理（两处防水卷材结合聚氨酯防水涂料搭配使用，采用两道防水），

涂刷高出地坪1800。

5)二次装修施工前需提出具体材料容重以便复核

4. 凡无地下室、地圈梁的建筑墙身均需在底层地面标高下150处做20厚1:2水泥砂浆防潮层（内掺水泥重量5%的防水剂）

底层室内相邻地坪有高差时，应在高差处墙身的侧面加设防潮层。当墙身一侧设有花坛和覆土时，相邻外侧应设防潮层，防潮层做法采用两处防水卷材结合防水涂料搭配使用，采用两道防水。

5. 内外墙预留孔洞的位置详见各专业施工图，并与建筑专业图纸核对后施工。
6. 门窗洞口过200底圈内应用实心砖砌边，底层砌体下部200高及埋入土体内砌体也应为实心砖。

砖砌体须按照总规定设置构造柱和圈梁过梁。窗台砌体顶部应设置条砖压顶，高60，宽同墙厚。

六 外墙面

1. 外墙采用干挂石材、玻璃、金属构件及预涂涂料，均应在现场做出样板，经设计单位及建设单位认可后方可订货。
2. 外墙采用幕墙的部分，委托有专项设计资质的专业单位设计及施工，本施工图仅提出以下设计要求：

(1) 分格及材料按相关建施立面及大样（预埋件为示意）。

(2) 部分详图待幕墙厂家确定后再作调整，专业单位设计后应经本单位审核同意后方可施工。

(3) 铝合金幕墙、门窗采用断桥热铝合金框，中空安全玻璃，低于800的窗台须加护栏等安全措施，幕墙与楼面和墙面交接处由幕墙公司负责做防火棉封堵处理。幕墙的固定均用预埋件连接，具体详幕墙专项设计单位设计图纸。

七 屋面

1. 本工程屋面防水等级为Ⅰ级，屋面具体防水做法详室内外装修做法表。
2. 屋面按皮脸排泄雨水，平屋面、露台的按皮均为2%；排水沟的按皮均为1%,按层顶按皮详图纸。找按材料均为轻质砼。屋面的低质砼找坡、防水层或水泥砂浆保护层均应设分格缝，分格缝纵横间距不大于6000。缝宽20，用防水油膏嵌密实。
3. 平层面保温隔热材料采用B1级挤塑聚苯板，按层面保温隔热材料采用A级岩棉板，厚度详节能计算书。
4. 卷材防水层面基层与突出的屋面结构（如女儿墙、立墙等）的连接处以及基层的阳角、阴角形状变化处（如水基口、檐沟等），均应增设一层干铺卷材增强层，并做成圆弧。穿屋面板管道或泛水以上外墙穿管，待安装完后应用细石砼封严；管板周围应做钢筋网水胶，与防水层闭合（具体做法详出屋面节点大样）。
5. 高低跨卷材屋面若高跨屋面为无组织排水时，低跨屋面受水冲刷的部位，应加铺一层整幅卷材，再铺设30厚C20，细石混凝土板（内配Φ4@200双向钢筋网）。当有组织排水时，水管基下应增设钢筋混凝土水簸箕。
6. 刚性层面按《屋面工程质量验收规范》要求设置分格缝，缝内填密封材料，刚性层面与女儿墙以及突出屋面的交接处，均用柔性密封材料密封。
7. 屋面做法详建筑装修做法表。屋面的泛水、排水口、透气管、进出风口、变形缝设备基础支架、烟道等突出、嵌入物均要求严格按详图和防水厂家、金属屋面厂家构造图施工，并应符合《屋面工程质量验收规范》GB50207-2012要求。

八 内墙及吊顶

1. 有吊顶的房间，其粉刷或装饰面层应做至吊顶标高以上100mm处。
2. 凡柱、墙和门洞阳角处均应宽80、高2400、与粉刷层同厚的1：2水泥砂浆护角。
3. 凡无吊顶处的内墙顶棚肚刷，均做顶棚角线。
4. 有噪声的机房（补风机房、排烟机房、空调机房）墙面及顶板均做隔音处理，设备采用低噪音设备，基础考虑隔震，隔音做法详室内外装修做法表。　　当管道穿过有水房的楼地面时，采用预埋套管，套管与楼地面防水胶泥堵实，以防渗漏。伸缩缝处楼地面做法详平面图

九 楼地面

1. 楼地面做法详见室内外装修做法表，踢脚高120，用料除注明者外均同相应楼面。
2. 卫生间、厨房等有排水要求的房间楼地面标高（除注明外）低于其余同层房间30，按向地漏，坡度不小于0.5，地漏水封比相应地面标高低8mm，地漏应在该房间最低处，地漏管道周围与找平层同点预留10X7mm,并应做填聚氨酯建筑密封膏。
3. 卫生间、厨房等有排水要求的房间地面均做聚氨酯防水层，并向四周墙面上做350高，卫生间墙面做1800高防水砂浆底。

房间楼板上四周墙体以及存在外露台的分界外墙下部均设同墙宽，200高C20混凝土翻边，与楼板一起浇筑以利防水

(除门处外)，当管道穿过有水房的楼地面时，采用预埋套管，并高出楼地面50mm，套管与楼地面用防水胶泥堵实，以防渗漏。

4. 伸缩缝处楼地面做法详平面图
5. 楼地面满足《建筑地面工程防滑技术规程》(JGJ/T331-2014)要求，室外工程、室内工程防滑安全程度为高级。

十 地下室防水

1. 本工程地下室防水工程按《地下工程防水技术规范》GB50108-2008的有关要求执行。
2. 本工程根据地下室使用功能，防水等级为 一 级。

地下室采用明挖法施工，设防做法为详表3.3.1-1(见《地下工程防水技术规范》)。

3. 本工程设有1层地下室，防水等级为一级，抗渗等级：P6，采用钢筋混凝土自防水结合卷材防水。

具体做法详室内外装修做法表。

4. 设防高度应比室外地坪高出500mm，附加防水层应须保作保护层，迎水面基层应按规范要求做圆角。

所有防水节点、指危处应有防水加强层。施工单位必须保证工程质量。

5. 地下室防水工程施工必须严格遵循国家或行业的标准规范，由专业人员操作施工，施工前应编制防水工程的施工方案和操作说明，施工中对防水工程的主要部位进行严格的质量控制，防水做法详建筑材料做法表。
6. 地下室外墙外侧20厚1:2.5水泥砂浆找平，1.2+1.2厚高分子防水卷材（后浇带、施工缝处1.5厚/,40厚挤塑聚苯板，回填土(300宽粘土)分层压实。外墙内侧粉20厚1:2水泥砂浆，分层抹平。
7. 地下室钢筋砼底板下，20厚1:2.5水泥砂浆保护层，1.2+1.2厚高分子防水卷材，150厚C15垫层，素土分层夯实。
8. 所有穿地下室外墙的管道，必须预埋防水穿墙套管。管道穿外墙防水构造详国标图集02J301《地下建筑防水构造》。
9. 地下室的预留孔穿位必须准确，不允许后期任意打洞，且预留孔洞封堵上方500，下方300范围内不得留施工缝。

十一 管道井及预留洞

1. 所有管道井/除钢筋混凝土墙外)均用120厚页岩砖，待设备管道安装完毕和检验合格后再砌筑。
2. 凡内外墙上留洞见建筑图，钢筋混凝土墙或楼板留洞详见结构图，施工前土建图须与设备图核对，各留洞净尺寸为长X宽X深，施工中土建、安装单位须密切配合。
3. 管道井在每层楼板用钢筋混凝土封隔，风道按修门的用丙级防火门。
4. 各种不同性质的管道应按有关规定规各色油漆以便区别，详设备说明。
5. 墙体上设计要求预留的洞、管道、沟槽等均应在砌筑时正确留出。
6. 配电箱、消火栓、水表墙面留洞，一般洞口与墙厚相等，管面均按钢板网粉刷，钢板网四周应大于孔洞200，特殊情况另见详图。如在防火隔墙上内嵌消火栓，必须在背面做防火岩棉隔离，耐火极限满足3小时。
7. 凡风道、烟道、竖井内壁砌筑灰缝须饱满，并随砌随抹平，有检修门的管道井内壁应随砌随抹灰。钢筋砼电梯井道不作粉刷。
8. 空调管穿砖墙时，可待管道安装后砌墙。

十二 门窗、栏杆及幕墙

1. 按本图纸明确的门窗、幕墙、钢雨篷、木隔栅造型及技术要求，由生产厂家进行荷载计算、节点设计并提出预埋件设置。其中木制品应进行防腐处理。
2. 本工程外窗抗风压性按《建筑外窗抗风压性能分级及检测方法》(GB/T7106-2008)定为6级；气密性按《建筑外窗气密性能分级及检测方法》(GB/T7107-2008)定为6级；水密性按《建筑外窗水密性能分级及检测方法》(GB/T7108-2008)定为3级。建筑外窗的隔声量不得低于GBB485-2002标准中的3级标准（30≤RW≤35）。
3. 本工程幕墙按《建筑幕墙物理性能分级》(GB/T7108-2008)控制抗风压性、气密性及雨水渗透性能，其中气密性等级不低于Ⅱ级。
4. 本工程采用断热铝合金(带纱窗)，表面氟碳喷涂，色彩选样定。安装位置距建筑外侧面80。玻璃选用低辐射中空玻璃窗，具体详节能计算书。
5. 本工程在使用过程中易受撞击部位的玻璃幕墙应有防撞击措施及警示标识。雨棚尽采光顶应采用镀白钢化玻璃合成的安全夹层玻璃，下方设置防坠落措施。
6. 门窗玻璃应符合《建筑安全玻璃管理规定》及《建筑玻璃应用技术规程》JGJ113-2009及J225-2009、发改运2003年2116号批文。
7. 门窗色彩与外墙颜色同时确定，门窗立面图中所示洞口尺寸均未考虑墙体饰面厚度，制作前必须根据实测洞口尺寸加工制作。门窗订货后，厂方须提供有关图纸经设计单位校核后再开工。
8. 抹灰线：窗位置参照中注明外，均立墙中。管道竖井及门槛高200，卫生间门安装时，门扇宜高出地面20mm。
9. 凡防火门窗及防火卷帘均应采用市消防大队认可的合格产品。
10. 门窗尺寸和数量按结构结束后由施工单位复核后再订货。凡非标门窗尺寸提过标准图要求者，须经生产厂家核算后，采取加强措施才能制作安装。
11. 低于800的窗台均采用防护栏杆，防护栏杆相对高度不小于1100。凡栏杆采用玻璃栏板的需采用钢化夹胶玻璃。

天窗采用断热铝合金框、中空夹胶玻璃，预注高偏好防水。

十三 油漆及防腐措施

1. 油漆采用环保型，木材须作防白蚁、防腐、防火处理。凡木材或木材与钢件接触部位均应涂氟化钠防腐剂；凡金属铁件均应先除锈，后涂防锈漆一道，面层再油调和漆二道。
2. 露明木构件采用底漆二度，面罩树脂清漆二度，颜色与档次会同业主商定。木塑件施以防腐油漆二度。
3. 室外露明件、木构件表应经可靠的防腐处理。

十四 防火

1. 各防火分区、设备用房、电梯机房、楼梯间等均须用不燃烧材料的防火墙分隔；防火墙的耐火极限应不低于3h。
2. 各种设备机房、防火墙上开门应为甲级防火门；安全疏散楼梯间及前室均门应为乙级防火门，并向疏散方向开启；管道井的检修门应为丙级防火门。
3. 玻璃幕墙与楼板及隔墙处的缝隙，应采用不燃烧材料填塞。
4. 外露的金属结构构件应涂防火涂料作保护层，耐火极限为：梁≥2h，板≥1.5h，防火涂料采用厚型钢结构防火涂料。
5. 防风井外的所有管道井，当管线安装完毕后，应在每层楼板处现浇钢筋砼（厚度同该层楼板）作上下层用钢筋砼防火分隔。
6. 防烟分区按玻施所示进行分隔
7. 防火分区：本工程分共两个防火分区，防火分区一：地下停车库，1634.6m，设两部疏散楼梯直通室外地面，疏散总宽度为2.4米。

防火分区二：地上建筑，3439.52m，设两部疏散楼梯直通室外地面，疏散总宽度为2.4米。

8. 防火卷帘（双轨）的耐火极限不低于3h,防火卷帘（双轨）应具备防潮性能，与楼板、梁和墙柱之间空隙用防火封堵材料封堵。

十五 电梯

1. 1#、2#客梯为无机房电梯，载重量为1350kg，速度为1.75米/秒,基坑深1.7米,1#、2#客梯来下降坑电梯；
2. 服务建筑1#食梯的载重量为200kg，速度为0.3米/秒，采用无机房、推车式餐梯,轿厢尺寸为800x800x1200(W×D×H).
3. 电梯层门的耐火极限不应低于1.00h，并应同时符合现行国家标准《电梯层门耐火试验 完整性、隔热性和热通量测定法》GB/T 27903 规定的完整性和隔热性要求。

十六 其 他

1. 本工程室外工程中道路、给排水、电力通讯、燃气等市政管线综合设计，以及园林绿化、小品等内容不属本次施工图范围，以上内容特由其他专业另行出图。(本施工图如与专项设计内容不符，请按专项设计图纸调整)。
2. 土建施工过程中，应与水、电、空调、通风等工种密切配合，若发现有矛盾，应与设计单位协商解决。
3. 凡是安装设备的地方，待设备到货后，应与设计图纸核对，相符后才可施工；若不相符，应作相应修改。
4. 本工程需使用预拌砂浆。
5. 凡窗头、窗台、雨蓬、飘板应均作滴水线。卫生洁具暂按常规尺寸考虑，施工中按建设单位要求配置。
6. 风管外墙（窗）上洞口处设铝合金百页窗，色彩同窗框。
7. 楼梯平台、外廊、内天井及上人屋面等临空处栏杆净高不应低于1.05m，且下部100mm高处不应留空。
8. 所有金属栏杆、玻璃栏杆等做法须经厂家和设计单位商定后方可施工，栏杆承受的荷载应符合《建筑结构荷载规范》GB50009-2012有关规定。
9. 散水、种植散水宽900,散水与斜脚处设10宽伸缩缝，每隔12米设20X10的防裂缝，内嵌石油沥青。
10. 弱电机房应由专业施工队伍施工,并满足<防静电工程技术规程>(DGJ08-83-2000)及其他有关规定。
11. 本工程施工及验收应严格执行国家现行有关建筑安装工程施工及验收规范。
12. 凡本工程说明及图纸未详尽处，均按国家有关规程规范执行。
13. 本项目各专业图纸未经专业单位图审以及消防等各级有职能部门审批不得施工。
14. 本项目露台做水泥基渗透结晶型防水涂料(1.5kg/m)，并厚度不小于1.0mm,涂刷至室内900。

十七 室外工程

1. 散水：建筑物四周做900宽种植散水，参05J909做8A/SW20，覆土300厚。散水与墙面交界处及沿散水长度方向每隔6米做20宽温度伸缩缝，1:2沥青砂浆装缝。
2. 其余做法详景观设计。

十八 无障碍设计

1. 本工程主要建筑出入口设有无障碍入口，入口坡度及其他建筑细部满足《无障碍设计规范》(GB 50763-2012)要求。
2. 本工程设残疾人专用厕位、洗手池及小便斗等无障碍设施。
3. 乘坐轮者开启的门窗，安装视线观察玻璃、横执把手和关门拉手，在门扇的下方应安装高0.350m门板（包括首层出入口）
4. 1#、2#客梯满足《无障碍设计规范》(GB 50763-2012) 第3.7条各项要求。

十九 消防设计说明

1. 本工程防火分区详单体。
2. 消防车道可到达建筑,距离主入口的距离均小于60米。

二十 建筑节能设计说明

1. 本工程按《公共建筑节能设计标准》(GB50189-2015)、《民用建筑热工设计规范》(GB50176-93)等现行国家规范进行节能计算并满足要求，具体说明详节能专篇，计算结果详节能计算书。

备注栏

设计单位

杭州园林设计院股份有限公司
HANGZHOU LANDSCAPE ARCHITECTURE DESIGN INSTITUTE CO.,LTD
建筑、风景园林甲级:A133013139
规划乙级:城规编（142056）
市政乙级:A233013136
文物保护工程勘察设计乙级:0102SJ0002
公司地址：杭州市西湖区双龙街138号西溪世纪中心2号楼南楼
电话：0571-87631011　　传真：0571-87631082　　网址：www.hzyly.com

建设单位：江苏茂源电气有限公司

工程总称	云创中心生产综合楼
子项名称	生产综合楼
图纸名称	建筑设计说明

	姓 名	签 名
审 定		
审 核		
项目负责人		
专业负责人		
设 计		
制 图		
校 对		

执业专用章

按规定加盖

出图章

未盖出图专用章无效

工号	25-14	图别	建施
图号	01	修改版次	
日期	2025.12		

工 程 做 法

	工程做法
一	地面做法：
1.	地1：环氧砂浆自流平地面（汽车库地面）
	5厚环氧砂浆自流平面层
	环氧底料一道
	50厚C30细石混凝土，抛打随麻光
	2厚聚合物水泥基防水涂料，四周沿墙泛起150高
	20厚1:3水泥砂浆
	最薄处30厚1.8煤渣混凝土找坡
	结构层
2.	地2：水泥地面（配电间、热水机房、排烟机房、消防水泵房）
	20厚1:2.5水泥砂浆，压实赶光
	2厚聚合物水泥基防水涂料，四周沿墙泛起150高
	20厚1:3水泥砂浆
	水泥浆一道（内掺建筑胶）
	160厚C15混凝土垫层
	结构层
3.	地3：水泥砂浆地面（消防水池）
	10厚1:2水泥砂浆
	12厚1:3水泥砂浆
	结构层
二	楼面做法：
1.	楼1：防滑楼面（厨房、备餐间、卫生间、更衣间、茶水间、配电间、消毒间、洗衣间、
	阳台、储藏间、化妆间、布草间）
	防滑地砖，干水泥擦缝
	20厚1:3干硬性水泥砂浆结合层，表面撒水泥粉
	2厚聚合物水泥基防水涂料
	1:3水泥砂浆找平
	水泥浆一道（内掺建筑胶）
	现浇钢筋混凝土楼板
2.	楼2：玻化砖地面楼面（食堂、门厅、包间、套间、单间、员工休息、办公、接待室、会议室、化妆间、休息室）
	玻化砖
	20厚1:3干硬性水泥砂浆结合层
	水泥浆一道（内掺建筑胶）
	60厚细石混凝土（上下配Φ3@50钢丝网片，中间配敷热管）
	0.2厚真空铝聚酯薄膜
	20厚聚苯乙烯泡沫板（保温层容度≥20kg/m3）
	1.5厚聚氨酯涂料防潮层
	0.2厚真空铝聚酯薄膜
	现浇钢筋混凝土楼板
3.	楼3：防静电地面：（消控室、弱电机房、控制室）
	成品防静电地板
	20厚1:2.5水泥砂浆，压实赶光
	2厚聚合物水泥基防水涂料，四周沿墙泛起150高
	20厚1:3水泥砂浆
	水泥浆一道（内掺建筑胶）
	现浇钢筋混凝土楼板
4.	楼4：花岗岩楼面（电梯厅、走道、休息厅、楼梯间）
	20厚磨光花岗岩
	30厚1:3干硬性水泥砂浆结合层，表面撒水泥粉
	2厚聚合物水泥基防水涂料
	1:3水泥砂浆找平
	水泥浆一道（内掺建筑胶）
	现浇钢筋混凝土楼板
三	汽车库坡道做法：
1.	坡1： 波纹环氧底漆一遍，间隔200宽6厚中黄环氧面漆加7#石英砂一道，间距600宽6厚绿色环氧面漆加3#石英砂一道
	100厚C30细石砼抛抛随抹平，按6×6米设置浇缝，油膏嵌缝，Φ8@200双向钢筋网
	素水泥浆结合层一道
四	屋面做法：
1.	坡屋面：
	琉有瓦
	40厚C20细石混凝土找平层，配Φb4@150网片置1:2水泥砂浆随抛随抹平，每间设10宽分仓缝，内嵌PVC防水油膏
	80厚挤塑聚苯板(XPS)(ρ=25)
	2厚高分子防水卷材（两道）
	30厚1：3水泥砂浆找平
	钢筋混凝土楼板

2.	平屋面一：
	20厚仿木纹地砖
	30厚1:3干硬性水泥砂浆结合层，表面撒水泥粉
	40厚C20细石混凝土找平层，配Φb4@150网片置1:2水泥砂浆随抛随抹平，每间设10宽分仓缝，内嵌PVC防水油膏
	80厚挤塑聚苯板(XPS)(ρ=25)
	2厚高分子防水卷材（两道）
	20厚1:3水泥砂浆找平层
	最薄处30厚LC5.0轻集料混凝土2%找坡
	现浇钢筋混凝土结构顶板
3.	平屋面二：(不上人平屋面)
	撒铺粒径20~50mm鹅石
	40厚C20细石混凝土找平层，配Φb4@150网片置1:2水泥砂浆随抛随抹平，每间设10宽分仓缝，内嵌PVC防水油膏
	80厚挤塑聚苯板(XPS)(ρ=25)
	2厚高分子防水卷材（两道）
	20厚1:3水泥砂浆找平层
	最薄处30厚LC5.0轻集料混凝土2%找坡
	现浇钢筋混凝土结构顶板
五	地下室顶板做法
1.	地下室顶板做法（自上而下）（覆土地带和道路，广场范围由景观设计定）
	覆土层及以上各层做法和景观设计协商定
	250g/m2聚酯长丝土工布过滤层
	60厚高凹凸型排蓄水板（成品），凸点向上
	防渗隔根膜（阻根防水卷材）
	60厚C20细石混凝土Φ6.5@200双向；(分格缝纵横间距小于6米，缝宽20mm，胶泥嵌缝)
	20厚1:2水泥砂浆找平（掺5%防水剂）
	耐根穿刺防水层：聚乙烯丙纶复合防水卷材厚度0.7+0.7,中间聚合物水泥胶结间聚合物水
	泥胶结料厚度不应小于料厚度不应小于1.3mm
	20厚1:2水泥砂浆找平（掺5%防水剂）
	弹性体改性沥青(SBS)防水卷材（U型）两层（4厚+3厚）
	最薄处30厚轻骨料砼找平兼找坡。（排水方向，排水坡度和总图专业协商定）
	现浇钢筋砼结构自防水地下室顶板
六	地下室底板做法：
	密实级配防水砼底板（板厚详结施）
	50厚C20细石混凝土保护层
	隔离层
	1.5厚自粘聚合物改性沥青防水卷材（无胎）
	1.5厚聚氨酯防水涂料
	20厚1:2.5水泥砂浆找平层
	100厚C15细石混凝土垫层
	素土夯实
七	内墙面做法：
1.	墙1：内墙涂料（食堂、包间、套间、单间、办公、会议室、休息室、员工休息、阳台、储藏间、化妆间、消控室、
	弱电机房、控制室、电梯厅、走道、门厅、休息厅、楼梯间）
	刮腻子白色乳胶漆两遍
	10厚1:2水泥砂浆抹面
	15厚1:3水泥砂浆打底
	砖墙面（或混凝土浆柱刷界面处理剂一道）
2.	墙2：水泥砂浆内墙（管道井、排烟机房、热水机房、消防水泵房、配电间）
	5厚1:2.5水泥砂浆抹面
	9厚1:3水泥砂浆打底
	砖墙面（或混凝土浆柱刷界面处理剂一道）
3.	墙3：瓷砖墙面（厨房、备餐间、卫生间、更衣间、茶水间、消毒间、洗衣间、布草间）
	5厚瓷砖白水泥浆擦缝
	6厚1：0.1:2.5水泥石灰膏砂浆结合层
	20厚防水砂浆分两次粉刷
	砖墙面（或混凝土浆柱刷界面处理剂一道）
4.	内墙4：(消防水池)
	20厚1:2防水水泥砂浆
	界面处理剂一道
	钢筋混凝土墙
5.	内墙4：防霉涂料(汽车库)
	刷（喷）乳白色防霉内墙涂料
	10厚1:2水泥砂浆抹面
	15厚1:3水泥砂浆打底
	砖墙面（或混凝土浆柱刷界面处理剂一道）

八	顶棚做法
1.	棚1：内墙涂料顶棚（除棚2、棚3、棚4以外范围）
	白色乳胶漆
	2厚面层耐水腻子刮平
	3厚底基防裂腻子分遍找平
	5厚1:0.5:3水泥石灰膏砂浆
	3厚1:0.5:1水泥石灰膏砂浆打底
	素水泥浆一道甩毛（内掺建筑胶）
	现浇板
2.	棚2：轻钢龙骨纸面石膏板顶棚(电梯厅、走道、门厅、休息厅、会堂)
	防火纸面石膏板
	满刮2厚面层耐水腻子找平，面板接缝处贴玻纤带，刮腻子抹平
	自攻螺丝与龙骨固定，中距≤200，螺钉距板边长边≥10，短边≥15
	C型轻钢覆面次龙骨CB50×20用吸顶吊件联结，间距≤800，次龙骨与次龙骨间距≤400
	龙骨吸顶吊件中距横向≤400，纵向≤800，用膨胀螺栓与钢筋混凝土板固定。
3.	棚3：轻钢龙骨铝扣板吊顶顶棚(卫生间、茶水间、消毒间、洗衣间)
	铝合金方板600×600与配套专用龙骨固定
	与铝合金方板配套的专用下层副龙骨联结，间距≤600
	与安装型式配套的专用上层主龙骨，间距≤1200，用吊件与钢筋吊杆联结后找平
	10号镀锌低碳钢丝吊杆，双向中距≤1200，吊杆上靠与板底预留吊环固定
	钢筋混凝土板底预留Φ10钢筋吊环，双向中距≤1200
4.	棚4：内墙涂料顶棚2（地下车库）
	刷（喷）乳白色防霉内墙涂料
	2厚面层耐水腻子刮平
	3厚底基防裂腻子分遍找平
	5厚1:0.5:3水泥石灰膏砂浆
	3厚1:0.5:1水泥石灰膏砂浆打底
	5厚抗裂砂浆耐碱复合玻纤网（配套固定件）
	50厚岩棉板（4级）保温层
	专用粘结剂
	现浇板
九	踢脚做法
1.	踢脚1：石材踢脚(地面上100高)(电梯厅、走道、门厅、休息厅、楼梯间)
	12厚花岗岩踢脚板
	10厚1：2水泥砂浆粘结层（内掺建筑胶）
	5厚1:3水泥砂浆打底划出纹道
2.	踢脚2：水泥砂浆踢脚(地面上100高)(排烟机房、热水机房、消防水泵房、配电间)
	6厚1:2.5水泥砂浆抹面压实赶光
	素水泥浆一道
	6厚1:3水泥砂浆打底划出纹道
	素水泥浆一道
	内保温薄抹灰完成面
3.	踢脚3：环氧涂层踢脚(地面上100高)(汽车库)
	1厚环氧涂层
	1厚腻子刮平
	6厚1:0.5:2水泥石灰膏砂浆找平
	8厚1:3水泥砂浆打底划出纹道
	素水泥浆一道（内掺建筑胶）
十	外墙面做法
1.	外墙1：(真石漆墙面)
	涂刷罩光漆漆
	真石漆仿花岗岩
	封闭底漆
	涂刮柔性耐水腻子
	抗裂砂浆复合耐碱玻纤网（5.0mm）
	25厚发台材料保温板
	200厚B07级砂加气（或混凝土浆柱刷界面处理剂一道）
2.	外墙2：(挡土墙下室外墙)
	2:8灰土分层夯实
	50厚挤塑聚苯板
	1.5厚自粘聚合物改性沥青防水卷材（无胎）
	1.5厚聚氨酯防水涂料
	20厚1:2.5水泥砂浆找平层
	现浇防水钢筋砼外墙

备注栏

设计单位

杭州园林设计院股份有限公司
HANGZHOU LANDSCAPE ARCHITECTURE DESIGN INSTITUTE CO, LTD
建筑、风景园林甲级：A133013139
规划乙级：城规编（1420056）
市政乙级：A233013136
文物保护工程勘察设计乙级：0102SJ0002
公司地址：杭州市西湖区双龙街53号西湖世纪中心2号楼南楼
电话：0571-87631011　　传真：0571-87631092　　网址：www.hzyly.com

建设单位	江苏茂源电气有限公司
工程总称	云创中心生产综合楼
子项名称	生产综合楼
图纸名称	工程做法

	姓 名	签 名
审 定		
审 核		
项目负责人		
专业负责人		
设 计		
制 图		
校 对		

执业专用章

按规定加盖

出图章

未盖出图专用章无效

工号	25-14	图别	建施
图号	02	修改版次	
日期	2025.12		

专业会签栏

弱电	
电气	暖通
结构	给排水
园林	建筑

江苏省公共建筑施工图绿色建筑专篇（建筑）

一、 项目名称： 云创中心生产综合楼　　子项：生产综合楼

二、 项目概况：

所在城市	气候分区	建筑性质	总建筑面积 $(m)^2$	停车库建筑面积 $(m)^2$	建筑高度	建筑层数	结构形式	绿色星级目标	建筑类别	利用可再生能源种类
东台	■夏热冬冷 □寒冷	食堂/公议办公/住宿	5074.12	1634.6	22.20	地上4层	框架	1星	■甲类 □乙类	■太阳能光热 □太阳能光伏　□地源热泵 □_____

注：停车库面积为地下汽车库面积。

三、 设计依据：

1. 《江苏省绿色建筑设计标准》DGJ32/T 173-2014
2. 《绿色建筑评价标准》GB/T50378-2014
3. 《民用建筑绿色设计规范》JGJ/T 229-2010
4. 《民用建筑热工设计规范》GB50176-2016
5. 《公共建筑节能设计标准》GB50189-2015
6. 《江苏省民用建筑施工图绿色设计文件编制深度规定》(2014年版)
7. 《建筑外门窗气密，水密，抗风压性能分级及检测方法》(GB/T 7106-2008)
8. 《建筑幕墙》(GB/T 21086-2007)
9. 《江苏省城市规划管理技术规定》(2011版)
10. 江苏省《公共建筑节能设计标准》DGJ32/J96-2010
11. 国家、省、市现行的法律、法规、其他相关标准和规定

四、 场地规划与室外环境：

1. 主要技术经济指标：

1）总用地面积_8549_平方米，总建筑面积_5074.12_平方米（其中：地下建筑面积_1634.6_平方米，地上建筑面积_3439.52_平方米

2）地下建筑面积与建设用地面积之比_0.19_，地下一层建筑面积与建设用地面积比率_19.12_ %。

3）机动车停车位数_17_（地上停车数___，地下停车数_17_，停车方式_自走_.

2. 场地周边 □ 有 ■ 无 电磁辐射。有时，其防护措施为：_____/_____。

3. 场地内 有□ 无■ 地质断裂构造。有时，土壤氡浓度为____/__Bq/m/，其防氡措施为：_____/_____。

（注：当土壤氡浓度≤20000 Bq/m 时，可不采取防氡措施。）

4. 本项目场地内无超标辐射的污染源。

5. 场地内无障碍停车位__2__ 辆，占总停车位比例_11.7_%，无障碍停车位位于__地下车库__ 。

6. 场地内道路系统便捷通畅，满足消防、救护及城灾救灾等要求。

7. 景观环境设计应符合下列要求：

1）停车场、人行道遮阳广场应种植高大乔木提供遮阳，机动车停车场遮阴率不应小于20%，景观主干道路乔木遮阴率不应小于50%，

步行道和自行车道遮阴率不应小于60%，室外活动场地、非机动车停车场应设置遮阳避雨措施。

2）场地内应结合绿化景观设计完善步行道路系统，提供配套的休憩设施，并综合遮阳、排水要求。

3）人行道道应安全、舒适，满足无障碍设计要求，且与场地外人行道道无障碍连通。

4）室外硬质铺装地面中透水铺装率不应小于50%，透水铺装垫层应采用透水构造做法；室外机动车停车场采用植草砖做透水地面时，镂空

面积比不应小于40%；场地内70%以上的道路路面的太阳辐射反射系数不低于0.4。

5）景观绿地设计应以乡土植物开发利用为主，兼顾引种，丰富城市绿地系统种种乡种植，本地植物种植坚不宜低于70%。

6）模拟植物的生态习性进行乡种植物的合理配植；种植应当适应当地气候和土壤条件的植物，采用乔、灌，草结合的复层绿化，绿化用地内

绿化覆盖率应大于70%。

五、 建筑设计与室内环境：

1. 主要功能空间的外墙、隔墙、楼板和门窗的隔声性能：

房间名称	构件名称	空气声隔声性能		楼板撞击声隔声性能		主要隔声材料及构造
		设计值 (dB)	标准限值 (dB)	设计值 (dB)	标准限值 (dB)	
办公、会议	外墙	50	>45			B07级砂加气
	隔墙	50	>50			B07级砂加气
	楼板	50	>50	59	65	120厚钢筋砼楼板
	外窗	35	>25			(6中透光low-E+12空气+6透明)（隔热金属窗框）
	外门	35	>20			(6中透光low-E+12空气+6透明)（隔热金属窗框）
住宿	外墙	50	>35			B07级砂加气
	隔墙	50	>45			B07级砂加气
	楼板	50	>45	59	65	120厚钢筋砼楼板
	外窗	35	>30			(6中透光low-E+12空气+6透明)（隔热金属窗框）
	外门	35	>25			(6中透光low-E+12空气+6透明)（隔热金属窗框）
食堂	外墙					B07级砂加气
	隔墙	50	>50			B07级砂加气
	楼板	50	>50			120厚钢筋砼楼板
	外窗					(6中透光low-E+12空气+6透明)（隔热金属窗框）
	外门					(6中透光low-E+12空气+6透明)（隔热金属窗框）

2. 主要房间室内允许的噪声等级符合《民用建筑隔声设计规范》GB50118-2010的要求。

3. 项目应进行专项声学设计的空间：无

4. 本项目产生较大噪音的设备机房（如水泵房、风机房、电梯机房、空调机房等）未与有安静要求的空间相邻布置，有振动的设备基础采取了减震措施，做法详：《建筑隔声与吸声构造》08J931-35，双层吉胶垫

5. 本项目根据《民用建筑工程室内环境污染控制规范》GB50325-2010(2013版)为 ■ I类　□ II类民用建筑工程，建筑材料及装修材料应符合《民用建筑工程室内环境污染控制规范》GB50325-2010(2013版)的相关规定。

室内空气中甲醛、苯、氨、氡和TVOC五类空气污染物应满足下列要求。

污染物名称	I类民用建筑工程限值	II类民用建筑工程限值	备注
甲醛 (mg/m^3)	≤0.08	≤0.10	
苯 (mg/m^3)	≤0.09	≤0.09	
氨 (mg/m^3)	≤0.20	≤0.20	
氡 (mg/m^3)	≤200	≤400	
TVOC (mg/m^3)	≤0.50	≤0.60	

6. 本项目油烟等产生异味或污染物的房间均设有封闭隔墙或门形成独立空间。

7. 本项目厨房专业厨具公司二次设计排油烟、暗卫生间就近在外窗设置建筑防雨百叶，详见图纸：卫生间大样_____，汽车库排风口设置详见图纸：地下室平面图_____。

8. 建筑装修设计时，不得破坏建筑主体结构。

9. 建筑材料选用符合国家和江苏省的相关规定，未采用限制、禁止使用和淘汰的的建筑材料。

六、建筑节能：

1. 基本情况：

气候分区	建筑类别	体形系数	总建筑面积 (m^2)	空调形式	集中采暖空调面积	利用可再生能源种类	节能计算方法	节能计算软件
夏热冬冷	■甲类 □乙类	0.27	5074.12	■集中 □分体		太阳能光热	■ 规定性指标 ■ 性能性指标	PKPM 建筑节能设计分析软件

2. 建筑物围护结构热工性能（详表1、表2、表3、表4）

表1：屋面、外墙、架空楼板、分隔非采暖空调房间与采暖空调房间的隔墙和楼板的热工性能

围护结构部位		主要保温材料 名称	干密度 (kg/m^3)	厚度 (mm)	导热系数 λ[W/(m.K)]	修正系数α	燃烧性能等级	传热系数K W/(m².K) 设计值	传热系数K W/(m².K) 规定限值	屋面基层及墙体材料	备注
屋面	层面1（平屋面）	挤塑聚苯板(XPS)(ρ=25)	25	80	0.030	1.25	B1	0.50	0.50	钢筋混凝土楼板	
	层面2（坡屋面）							0.50	0.50	钢筋混凝土楼板	
外墙	外墙1（墙体）	复合材料保温板	350	30	0.06	1.20	A	0.79		B07级砂加气	
	外墙2（梁）	复合材料保温板	350	25	0.06	1.20	A	1.53		钢筋混凝土梁	
	外墙3（柱）	复合材料保温板	350	25	0.06	1.20	A	1.53		钢筋混凝土柱	
外墙平均热工性能								0.97	0.80		
底面接触室外空气的架空层或外挑楼板		岩棉外墙外保温板	140	60	0.04	1.30	A	0.72	0.70	钢筋混凝土楼板	
非采暖空调房间与采暖空调房间的隔墙											
非采暖空调房间与采暖空调房间的楼板											

经计算本工程屋面、外墙热桥部位的冬季内表面温度均不低于露点温度，其热阻值分别为_2.01_(m².K)/W、_0.65_(m².K)/W 。

表2：地面和地下室外墙热工性能（无）

围护结构部位	主要保温材料 名称	干密度 (kg/m^3)	厚度 (mm)	导热系数 λ[W/(m.K)]	修正系数α	燃烧性能等级	热阻 R (m².K)/W 设计值	热阻 R (m².K)/W 规定限值	基层材料	备注
采暖空调地下室地面										
地上采暖空调房间的地下室顶板										
采暖、空调地下室外墙（与土壤接触的外墙）										

表3：外窗（包括透明幕墙）的热工性能

朝向	构造 窗框（幕墙型材）	构造 玻璃	构造 遮阳形式	窗墙面积比（天窗屋面比） 设计值	窗墙面积比（天窗屋面比） 规定限值	传热系数K W/(m².K) 设计值	传热系数K W/(m².K) 规定限值	太阳得热系数SHGC 设计值	太阳得热系数SHGC 规定限值
东	隔热金属型材 Kf=5.8W/(m2.K)断配20%	6中透光low-E+12空气+6透明	玻璃自遮阳	0.32	0.70	2.60	2.60	0.34	<0.40
南	隔热金属型材 Kf=5.8W/(m2.K)断配20%	6中透光low-E+12空气+6透明	玻璃自遮阳	0.10	0.70	2.60	3.50	0.35	
西	隔热金属型材 Kf=5.8W/(m2.K)断配20%	6中透光low-E+12空气+6透明	玻璃自遮阳	0.27	0.70	2.60	3.00	0.35	<0.44
北	隔热金属型材 Kf=5.8W/(m2.K)断配20%	6中透光low-E+12空气+6透明	玻璃自遮阳	0.11	0.70	2.60	3.50	0.35	

表4：外窗（包括透明幕墙）的可见光透射比、可开启面积比、幕墙可见光反射比、耐火完整性

朝向	玻璃可见光透射比 设计值	玻璃可见光透射比 规定限值	外窗可开启面积比 设计值	外窗可开启面积比 规定限值	幕墙可开启面积比 设计值	幕墙可开启面积比 规定限值	幕墙可见光反射比 设计值	幕墙可见光反射比 规定限值	*耐火完整性(h) 设计值	*耐火完整性(h) 规定限值	备注
东	0.62	>0.6	0.45	30%		10%(5%)		0.2		0.5	玻璃幕墙开启面积比5%的限值用于10层及其上楼层；玻璃幕墙的开启面积不足时，设置通风换气装置
南	0.62	>0.6	0.50	30%		10%(5%)		0.2		0.5	
西	0.62	>0.6	0.35	30%		10%(5%)		0.2		0.5	
北	0.62	>0.6	0.45	30%		10%(5%)		0.2		0.5	

注：*项为外墙外保温按《建筑设计防火规范》GB50016-2014第6.7.7条规定采用B1、B2级材料时，外门窗耐火完整性不应低于0.5h，采用A级材料时无此要求。

本项目外门窗气密性不低于《建筑外门窗气密、水密、抗风压性能分级及检测方法》GB/T7106-2008规定的 6 级。

本项目幕墙气密性不低于《建筑幕墙》GB/T 21086-2007规定的 ／ 级。

3. 可再生能源的利用

1）本项目 ■ 有 □ 无 太阳能热水供应系统，使用_____电_____辅助热源，供热水量_3.024__m /d，占建筑生活热水总量的_52.6__% ，太阳能集热器位置：_____层顶_____。太阳能热水系统应符合《民用建筑太阳能热水系统应用技术规范》GB50364-2005、江苏省《建筑太阳能热水系统设计、安装与验收规范》DGJ32/J08-2008的要求。

2）本项目 □ 有 ■ 无 地源热泵空调系统，承担采暖空调负荷的比例为_____/__%。地源热泵空调系统应符合《地源热泵系统工程技术规范》GB50366-2009、江苏省《地源热泵系统工程技术规程》DGJ32/TJ89-2009的要求。

3）本项目 □ 有 ■ 无 太阳能光伏发电 □ 有 ■ 无 光导照明系统，其总功率为建筑物总安压器装机容量的_____/__%。太阳能光伏系统应符合《民用建筑太阳能光伏系统应用技术规范》JGJ203-2010、江苏省《太阳能光伏与建筑一体化应用技术规程》DGJ32/J87-2009的要求。

4）其他_____。

4. 权衡判断

本工程__仓楼加权外墙平均传热系数；夏热冬冷甲类建筑架空楼板__不符合规定性指标，需要进行权衡判断。

全年采暖和空气调节能耗 (kwh/m²)	设计建筑	参照建筑	结论
	40.19	40.33	满足

5. 其他


1）本项目采用___复合材料保温板_____外保温系统应符合《复合材料保温板外墙外保温系统应用技术规程》DGJ32-TJ204-2016标准的要求。

2）本项目采用外遮阳系统应符合江苏省《建筑外遮阳工程技术规程》DGJ32/J123-2011的要求（根据是否设置外遮阳增删）。


3）本项目开列集中设置的多台电梯应具有集中调度和群控功能；自动扶梯、自动人行披道应具有节能拖动和节能控制装置。

4）绿色建筑的施工应符合国家、江苏省有关施工验收规程的要求。


6. 节能详图（以下节点详图具体做法还应符合10J121要求）

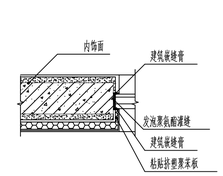

窗洞侧口构造详图

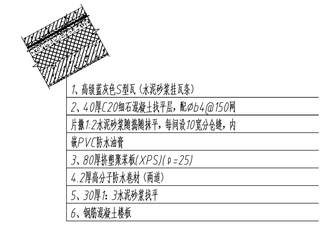


坡屋面保温构造详图

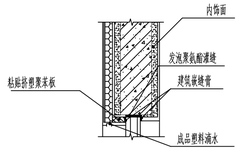

窗洞上口构造详图



平屋面保温构造详图

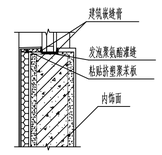


窗洞下口构造详图



架空层楼板保温构造详图



外墙（梁柱部位）保温构造详图

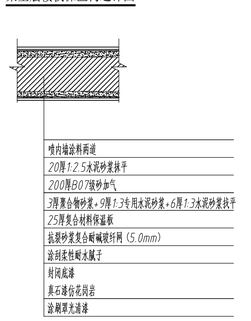

外墙（砌体墙部位）保温构造详图

备注栏

设计单位
杭州园林设计院股份有限公司
HANGZHOU LANDSCAPE ARCHITECTURE DESIGN INSTITUTE CO.,LTD
建筑、风景园林甲级：A133013139
规划乙级：城规编（142056）
市政乙级：A233013136
文物保护工程勘察设计乙级：0102SJ0002
公司地址：杭州市西湖区双龙街136号西湖世纪中心2号楼南楼
电话：0571-87051011　　传真：0571-87051002　　网址：www.hzyly.com

建设单位	江苏茂源电气有限公司
工程总称	云创中心生产综合楼
子项名称	生产综合楼
图纸名称	绿色建筑节能设计专篇

	姓名	签名
审定		
审核		
项目负责人		
专业负责人		
设计		
制图		
校对		

执业专用章


按规定加盖

出图章

未盖出图专用章无效

工号	25-14	图别	建施
图号	03	修改版次	
日期	2025.12		

弱电　电气　暖通　结构　给排水　园林　建筑　专业会签栏

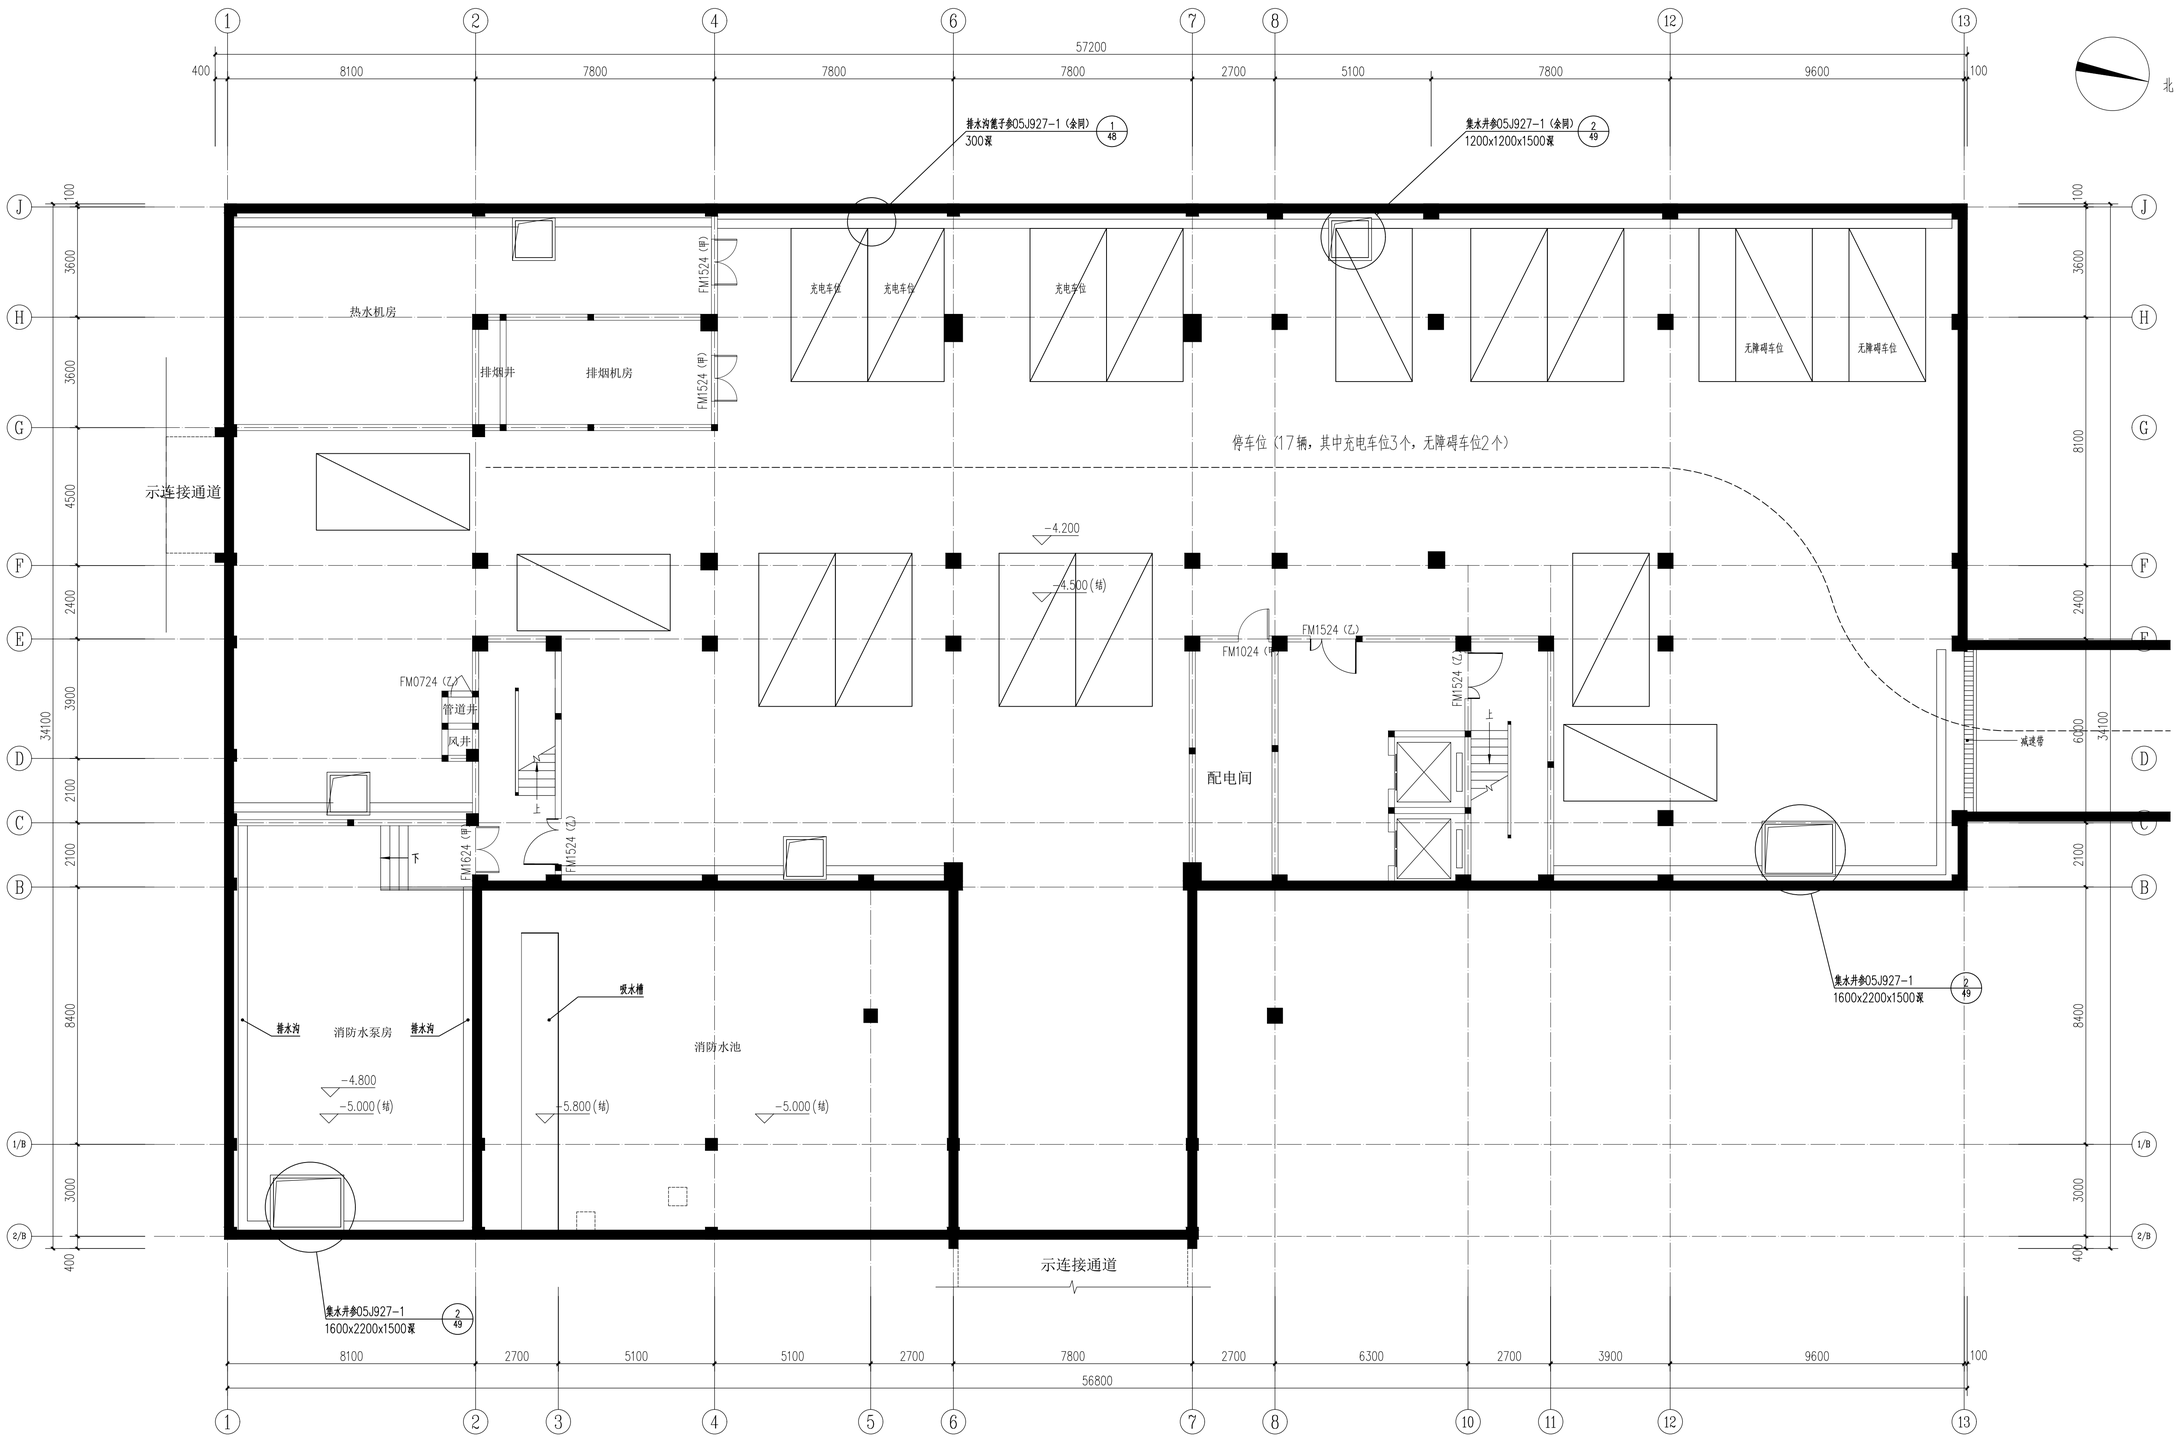

地下室平面图 1:100

地下建筑面积：1634.6平方米

1、图中标注构CZ，做法为结构图号T2中图9－7构造柱
2、图中所有门窗侧边构设边框柱，做法为结构图号T2中图9－8构造柱,门侧边框柱高度从楼面至过梁顶
3、内墙在门头过梁和同底标高部位设通长水平系梁一道，做法为结构图号T2中图9－4

备注栏

设计单位

杭州园林设计院股份有限公司
HANGZHOU LANDSCAPE ARCHITECTURE DESIGN INSTITUTE CO.,LTD
建筑、风景园林甲级:A133013139
规划乙级:城规编（1420356）
市政乙级:A233013136
文物保护工程勘察设计乙级:0102SJ0002
公司地址：杭州市西湖区双龙街138号西湖世纪中心5号楼南楼
电话：0571-87031011　　传真：0571-87031002　　网址：www.hzyly.com

建设单位	江苏茂源电气有限公司
工程总称	云创中心生产综合楼
子项名称	生产综合楼
图纸名称	地下室平面图

	姓 名	签 名
审 定		
审 核		
项目负责人		
专业负责人		
设 计		
制 图		
校 对		

执业专用章

按规定加盖

出图章

未盖出图专用章无效

工号	25-14	图别	建施
图号	04	修改版次	
日期	2025.12		

防烟分区	餐厅		长边长度34.2m
分区面积	400	m^2	
空间净高	3.45	m	
清晰高度	2.4	m	最小清晰高度1.6+0.1x3.45=1.95
储烟仓厚度	1.05	m	不小于3.45x0.2=0.69
所需有效开窗面积	8	m^2	
实际有效开窗面积	9.2	m^2	
自然排烟窗（口）有效面积按			GB51251-2017
计算，应位于储烟仓内，距室内任一点≤ 30m。			

防烟分区	厨房		长边长度22.3m
分区面积	318	m^2	
空间净高	5	m	
清晰高度	2.4	m	最小清晰高度1.6+0.1x5=2.1
储烟仓厚度	2.6	m	不小于5x0.2=1
所需有效开窗面积	6.36	m^2	
实际有效开窗面积	6.54	m^2	
自然排烟窗（口）有效面积按			GB51251-2017
计算，应位于储烟仓内，距室内任一点≤ 30m。			

1#卫生间详建施-16

1#垂梯详建施-17

铝合金防雨百叶 1600X600贴聚底

铝合金防雨百叶 700X400贴聚底

铝合金防雨百叶（带滤网） 700X400贴聚底

铝合金防雨百叶 1600X400贴聚底

200高混凝土门槛

地下室坡线

主库迁间

凉菜间

素菜

食堂

女卫

男卫

保洁

消控室

门厅

配电间

弱电井

管道井

风井

烟井

空调井

电梯厅

检测间

耗材库

副食库

主食库

男更衣

女更衣

冷藏库

保洁间

传菜梯

排水沟参05J927-1 2/46

05J909 一 SW8 花岗岩面层台阶（余同）

-0.150（室外地坪）

±0.000

-0.300

-0.015

-0.005

1:12

北

地暖范围：结构标高低于建筑标高120mm

降板范围：结构标高低于建筑标高400mm

1、图中标注均为GZ，做法为结构图号T2中图9－7构造柱

2、图中所有门窗侧边均设边框柱，做法为结构图号T2中图9－8构造柱,门侧边框柱高度从楼面至过梁顶，窗侧边框柱高度从窗台压顶至过梁顶

3、外墙在窗台部位设通长混凝土带一道，做法为b*h=200*120，主筋3Φ10，分布筋Φ6@200,外墙在窗头过梁相同底标高部位设通长水平系梁一道，做法为结构图号T2中图9－4,内墙在门头过梁相同底标高部位设通长水平系梁一道，做法为结构图号T2中图9－4

4、在食堂、卫生间，含堂男女更衣室楼面增加四处卧水一道，周边墙面上翻30厘米高。（卧止渗漏影响车库顶棚岩棉板、岩棉板吸水后重量增加掉落）

一层平面图 1:100

建筑面积：1119.5平方米

总建筑面积：5074.12平方米

地上总建筑面积：3439.52平方米

防烟分区	大厅		长边长度13.1m 有喷淋，热释放率2.5MW
分区面积	95	m^2	
空间净高	8	m	
清晰高度	2.4	m	最小清晰高度1.6+0.1x8=2.4
储烟仓厚度	5.6	m	不小于8x0.2=1.6
所需有效开窗面积	36.04	m^2	依据GB51251－2017－4.6.3－其他公共建筑：9.6x10^4/3600/0.74=36.04平下部门窗自然排风 补风面积：19.19m2
实际有效开窗面积	38.3	m^2	
自然排烟窗（口）有效面积按			GB51251－2017
计算，应位于储烟仓内，距室内任一点≤ 30m。			

备注栏

设计单位

杭州园林设计院股份有限公司

HANGZHOU LANDSCAPE ARCHITECTURE DESIGN INSTITUTE CO, LTD

建筑、风景园林甲级:A133013139

规划乙级:城规编（142056）

市政乙级:A233013136

文物保护工程勘察设计乙级:0102SJ0002

公司地址：杭州市西湖区双龙街130号西城世纪中心5号楼南楼

电话：0571-87631011 传真：0571-87631092 网址：www.hzyly.com

建设单位	江苏茂源电气有限公司
工程总称	云创中心生产综合楼
子项名称	生产综合楼
图纸名称	一层平面图

	姓 名	签 名
审 定		
审 核		
项目负责人		
专业负责人		
设 计		
制 图		
校 对		

执业专用章

按规定加盖

出图章


未盖出图专用章无效


工号	25-14	图别	建施
图号	05	修改版次	
日期	2025.12		

防烟分区	走廊3-3		走廊宽2.2m；长轴长度46.9m 局部宽4.0m(7.35m长)； 平均宽度：(2.2x39.55+4x7.35)/46.9=2.48m
分区面积	125	m^2	
空间净高	3.0	m	
设计储烟高度	1.5	m	最小储烟高度 3/2=1.5m
储烟仓厚度	1.5	m	H-Hs=3x0.2=0.6
所需有效开窗面积	4	m^2	走廊两端每处宜至少分设2个开启面积不小于2平方米的自然排烟窗(口)，且两个排烟窗(口)之间的水平距离不宜小于走廊长度的1/3
实际有效开窗面积	4.41	m^2	1.5x1.5m,高度以上开启扇开窗面积
自动喷水灭火系统设置场所			GB51251-2017
计算：后位于储烟仓内，距室内任一点≤30m。			

3#卫生间详建施-16

4#卫生间详建施-16

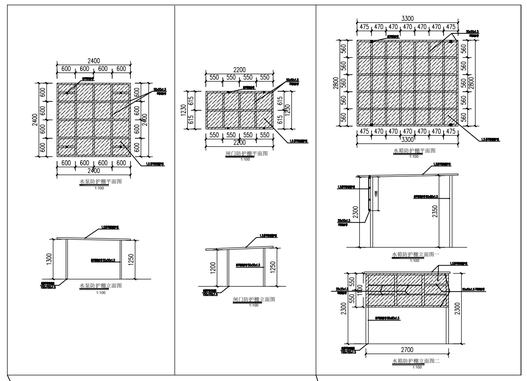

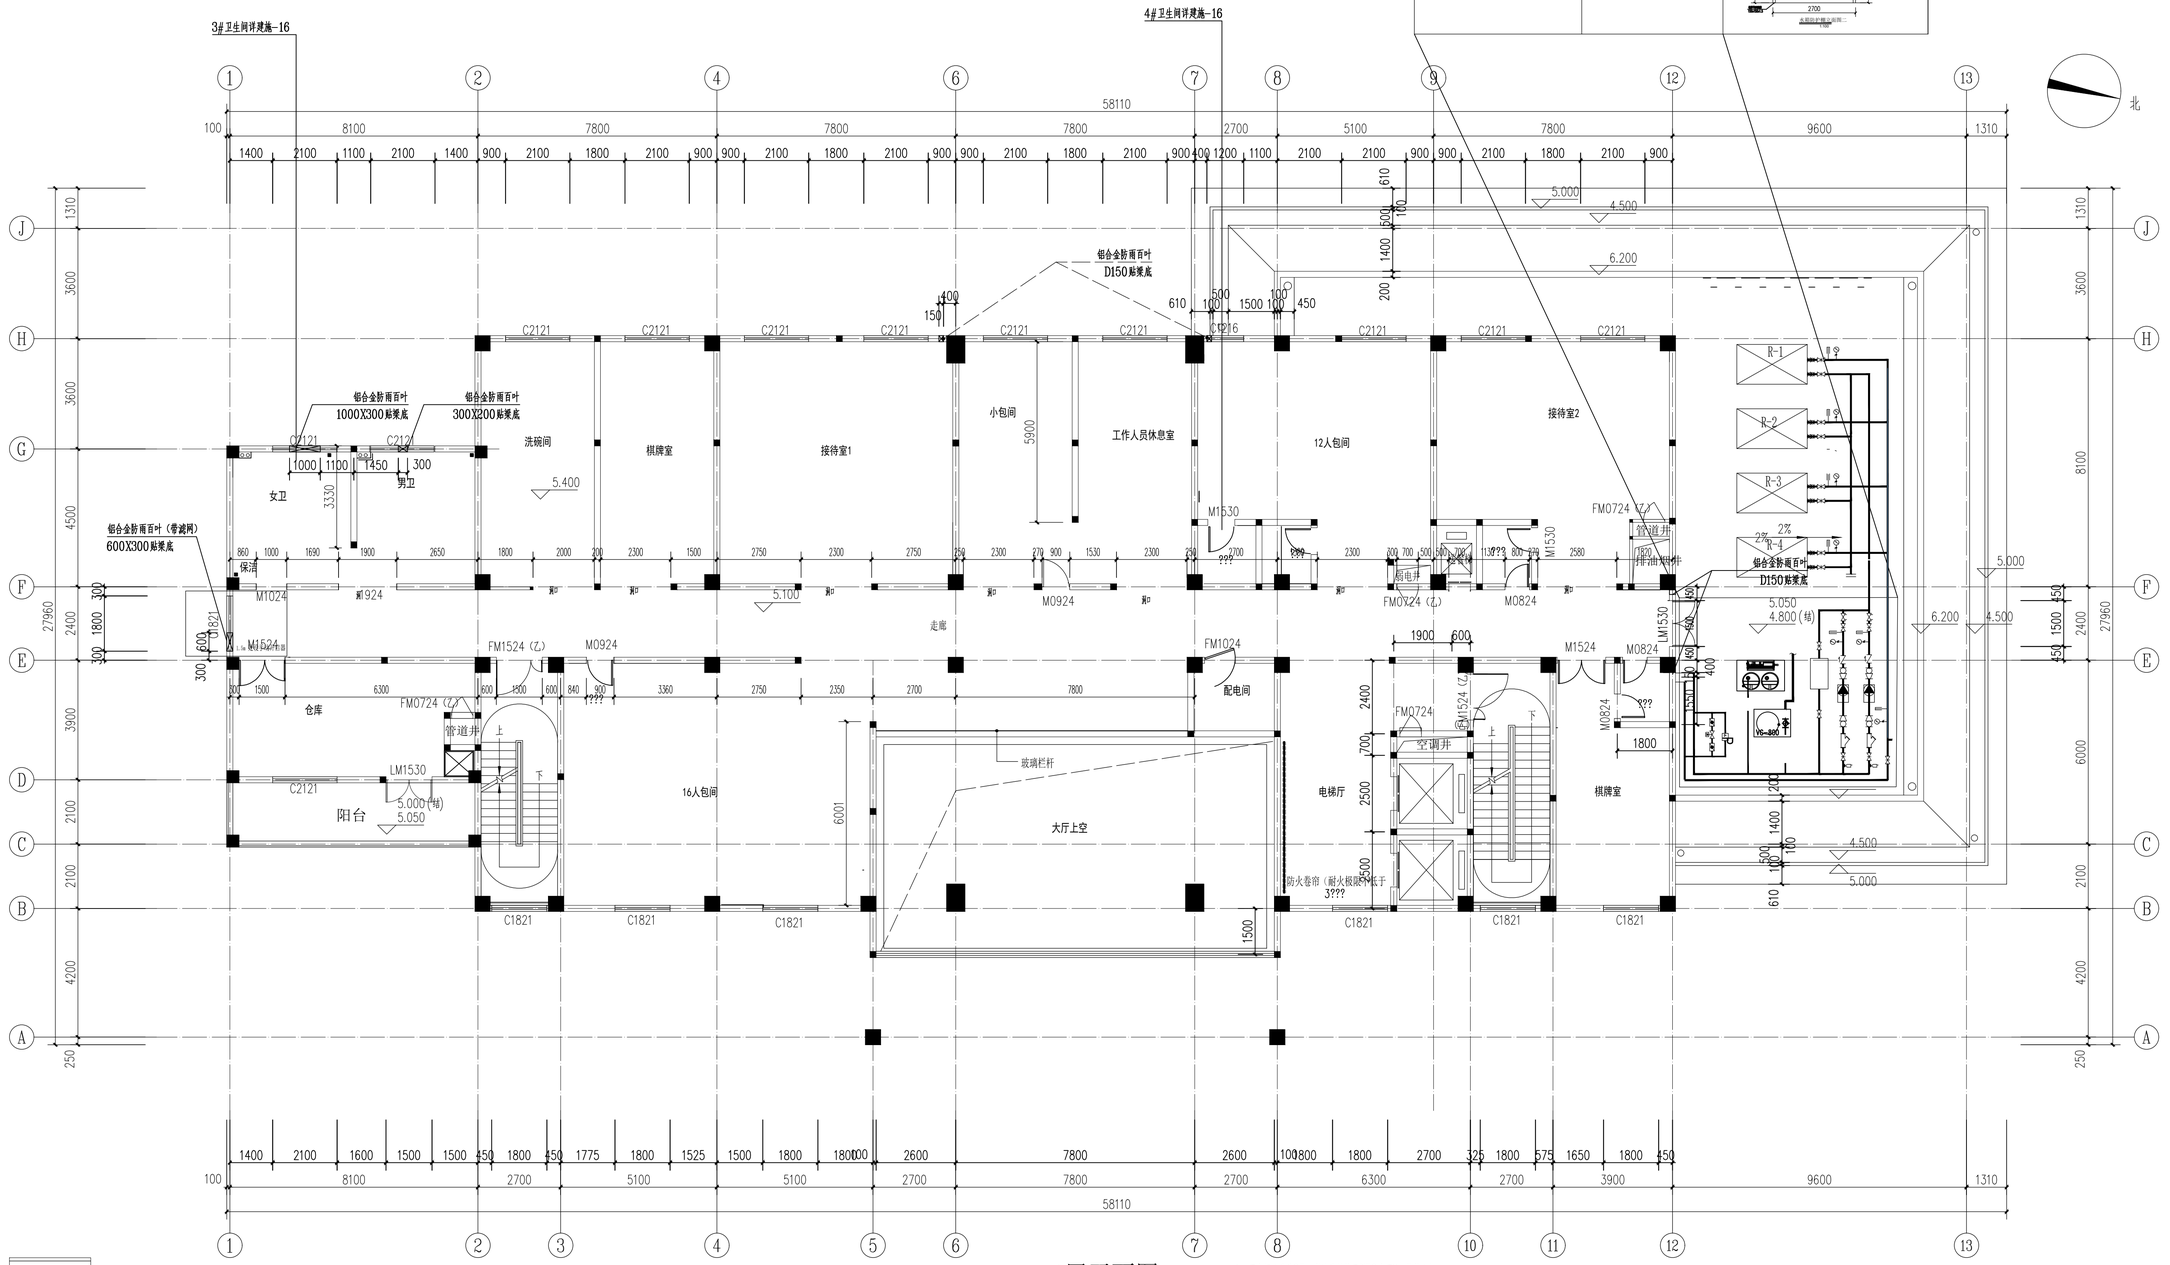

地暖范围：结构标高低于建筑标高120mm

降板范围：结构标高低于建筑标高400mm

二层平面图 1:100

建筑面积：846.1平方米

1、图中标注构为GZ，做法为结构图号T2中图9－7构造柱

2、图中所有门窗侧边构造柱框柱，做法为结构图号T2中图9－8构造柱,门侧边框柱高度从楼面至过梁顶，窗侧边框柱高度从窗台压顶至过梁顶

3、外墙在窗台部位设通长混凝土带一道，做法为b*h=200*120，主筋3?C10，分布筋?C6@200,外墙在窗头过梁相同底标高部位设通长水平系梁一道，做法为结构图号T2中图9－4,内墙在门头过梁相同底标高部位设通长水平系梁一道，做法为结构图号T2中图9－4

备注栏

设计单位

杭州园林设计院股份有限公司
HANGZHOU LANDSCAPE ARCHITECTURE DESIGN INSTITUTE CO.,LTD
建筑、风景园林甲级(A133013139
规划乙级:城规编(1620156)
市政乙级:X233013136
文物保护工程勘察设计乙级:0102SJ0002
公司地址：杭州市西湖区双龙巷38号西湖世纪中心5号楼南楼
电话：0571-87031011　　传真：0571-87031002　　网址：www.hzyly.com

建设单位	江苏茂源电气有限公司	
工程总称	云创中心生产综合楼	
子项名称	生产综合楼	
图纸名称	二层平面图	
	姓 名	签 名
审 定		
审 核		
项目负责人		
专业负责人		
设 计		
制 图		
校 对		

执业专用章

按规定加盖

出图章


未盖出图专用章无效

工号	25-14	图别	建施
图号	06	修改版次	
日期	2025.12		

专业会签栏：园林　建筑　结构　给排水　电气　弱电

防火分区二

防烟分区	走道		走道宽2.2m；长度长度38.9m
分区面积	85	m²	
空间净高	3.0	m	
设计清晰高度	1.5	m	最小清晰高度 3/2=1.5m
储烟仓厚度	1.5	m	不小于3x0.2=0.6
所需有效开窗面积	4	m²	走道两端均设置长不小于2 平台有可开启外窗可开启外窗洞面积长大于走道面积的2/3
实际有效开窗面积	4.41	m²	1.50m高设门上设置开窗净面
自然排烟窗（口）有效面积计算。应位于储烟仓内，距室内任一点≤ 30m。			GB51251-2017

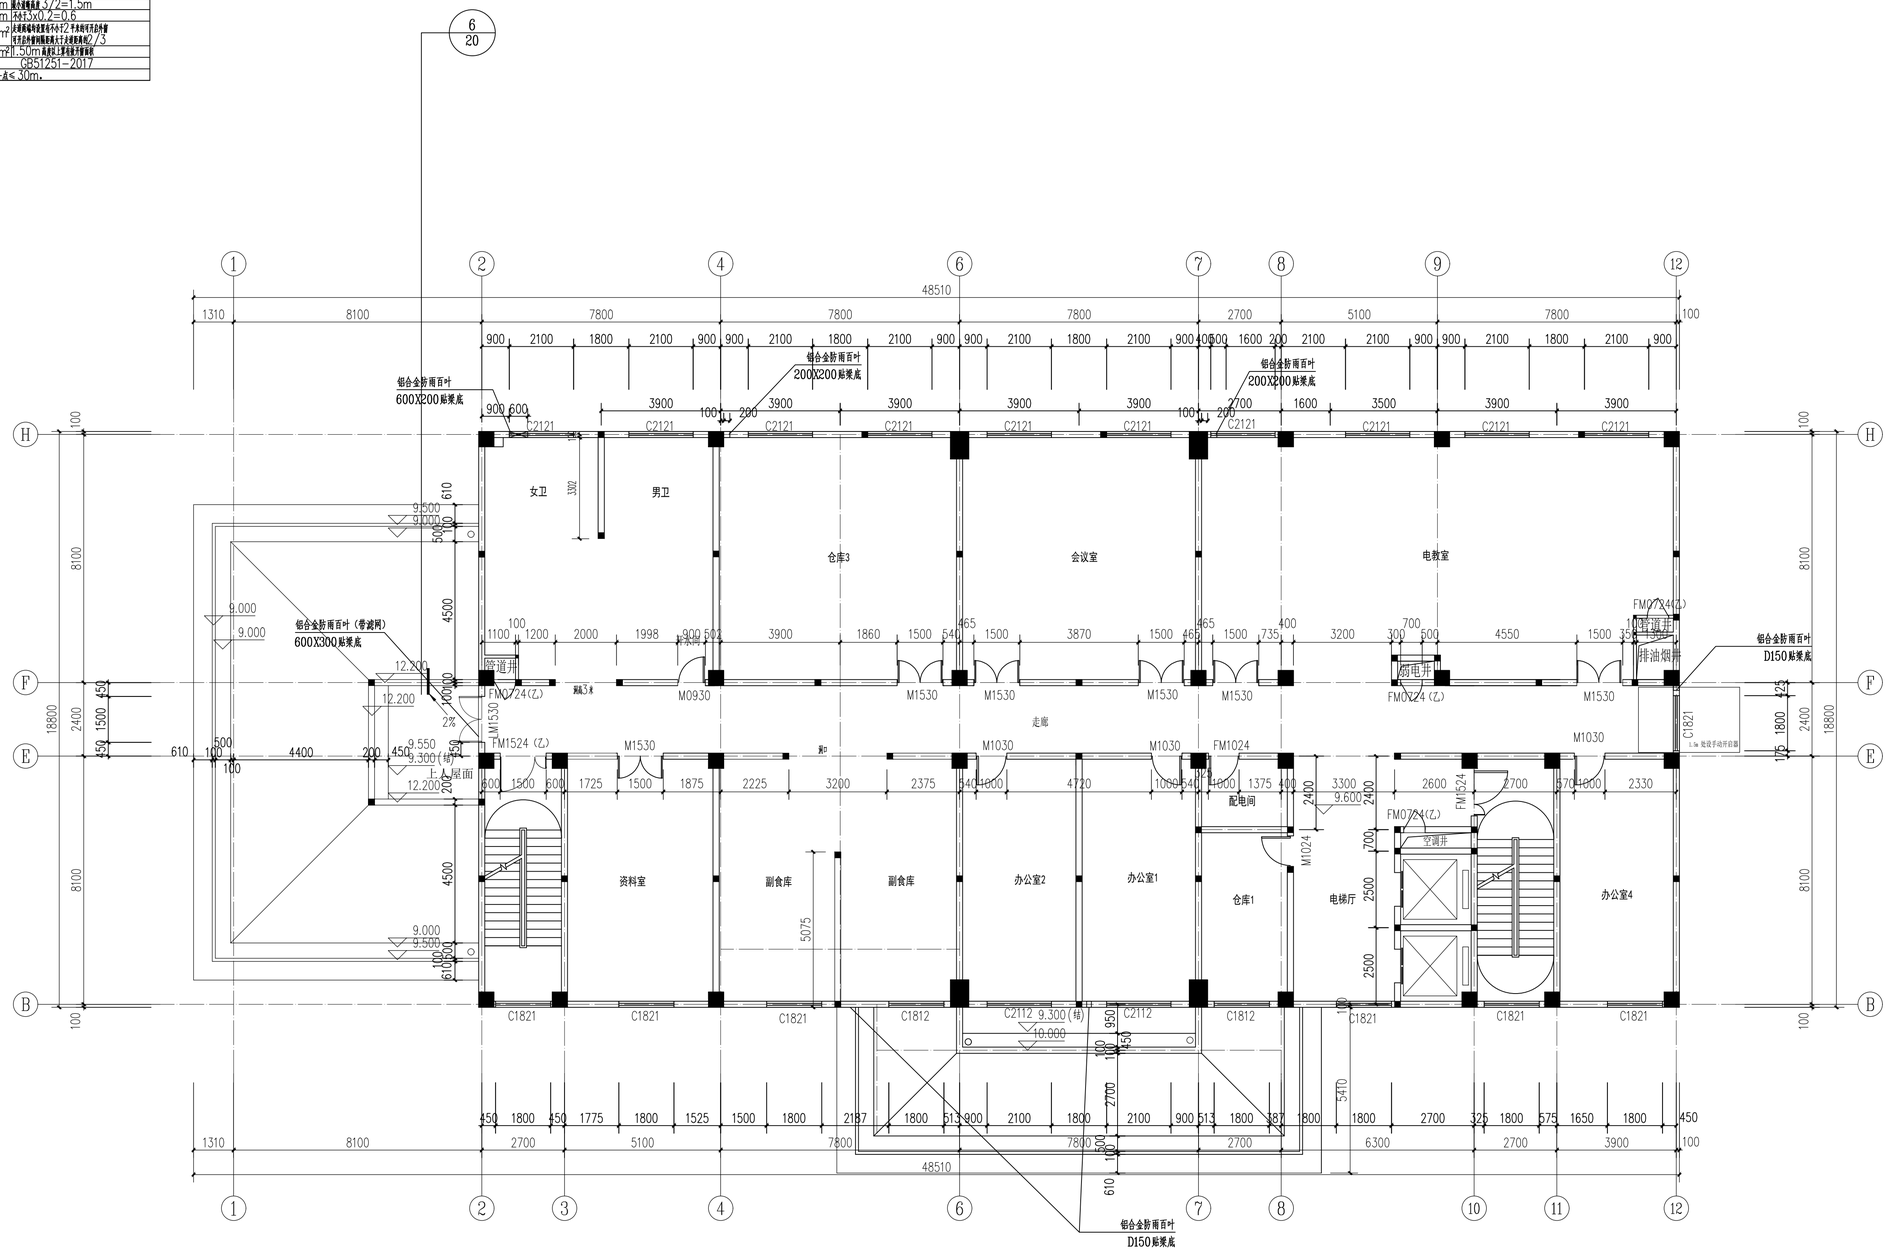

地暖范围：结构标高低于建筑标高120mm

降板范围：结构标高低于建筑标高100mm

三层平面图 1:100

建筑面积：736.96平方米

1、图中标注均为GZ，做法为结构图号T2中图9－7构造柱
2、图中所有门窗侧边均设边框柱，做法为结构图号T2中图9－8构造柱,门侧边框柱高度从楼面至过梁顶，窗侧边框柱高度从窗台压顶至过梁顶
3、外墙在窗台部位设通长混凝土带一道，做法为*h＝200*120，主筋3?C10，分布筋?C6@200,外墙在窗头过梁相同底标高部位设通长水平系梁一道，做法为结构图号T2中图9－4,内墙在门头过梁相同底标高部位设通长水平系梁一道，做法为结构图号T2中图9－4

备注栏

设计单位

杭州园林设计院股份有限公司
HANGZHOU LANDSCAPE ARCHITECTURE DESIGN INSTITUTE CO, LTD
建筑、风景园林甲级:A133013139
规划乙级:城规编（142056）
市政乙级:A233013136
文物保护工程勘察设计乙级:0102SJ0002
公司地址：杭州市西湖区双龙街138号西城世纪中心5号楼南楼
电话：0571-87631011　　传真：0571-87631092　　网址：www.hzyly.com

建设单位	江苏茂源电气有限公司
工程总称	云创中心生产综合楼
子项名称	生产综合楼
图纸名称	三层平面图

	姓 名	签 名
审 定		
审 核		
项目负责人		
专业负责人		
设 计		
制 图		
校 对		

执业专用章

按规定加盖

出图章


未盖出图专用章无效

工号	25-14	图别	建施
图号	07	修改版次	
日期	2025.12		

防火分区二

防烟分区	净高H		安全长度18.4m
分区面积	29.5	m^2	
空间净高	4.4	m	
清晰高度	2.2	m	最小清晰高度 1.6+0.1x4.4=2.04
储烟仓厚度	2.2	m	4.4-4.4x0.2=0.88
所需有效开窗面积	5.86	m^2	
实际有效开窗面积	5.92	m^2	
自然排烟窗（口）有效面积比			GB51251-2017
计算：应位于储烟仓内，距室内任一点≤ 30m。			

防烟分区	走廊		安全长度23m
分区面积	53	m^2	
空间净高	4.4	m	
清晰高度	2.2	m	最小清晰高度 4.4/2=2.2m
储烟仓厚度	2.2	m	4.4-4.4x0.2=0.88
所需有效开窗面积	4	m^2	走廊两端每外设置长不小于2平方米可开启外窗，可开启外窗到最近防火门走道距离不超过2/3
实际有效开窗面积	4.66	m^2	
自然排烟窗（口）有效面积比			GB51251-2017
计算：应位于储烟仓内，距室内任一点≤ 30m。			

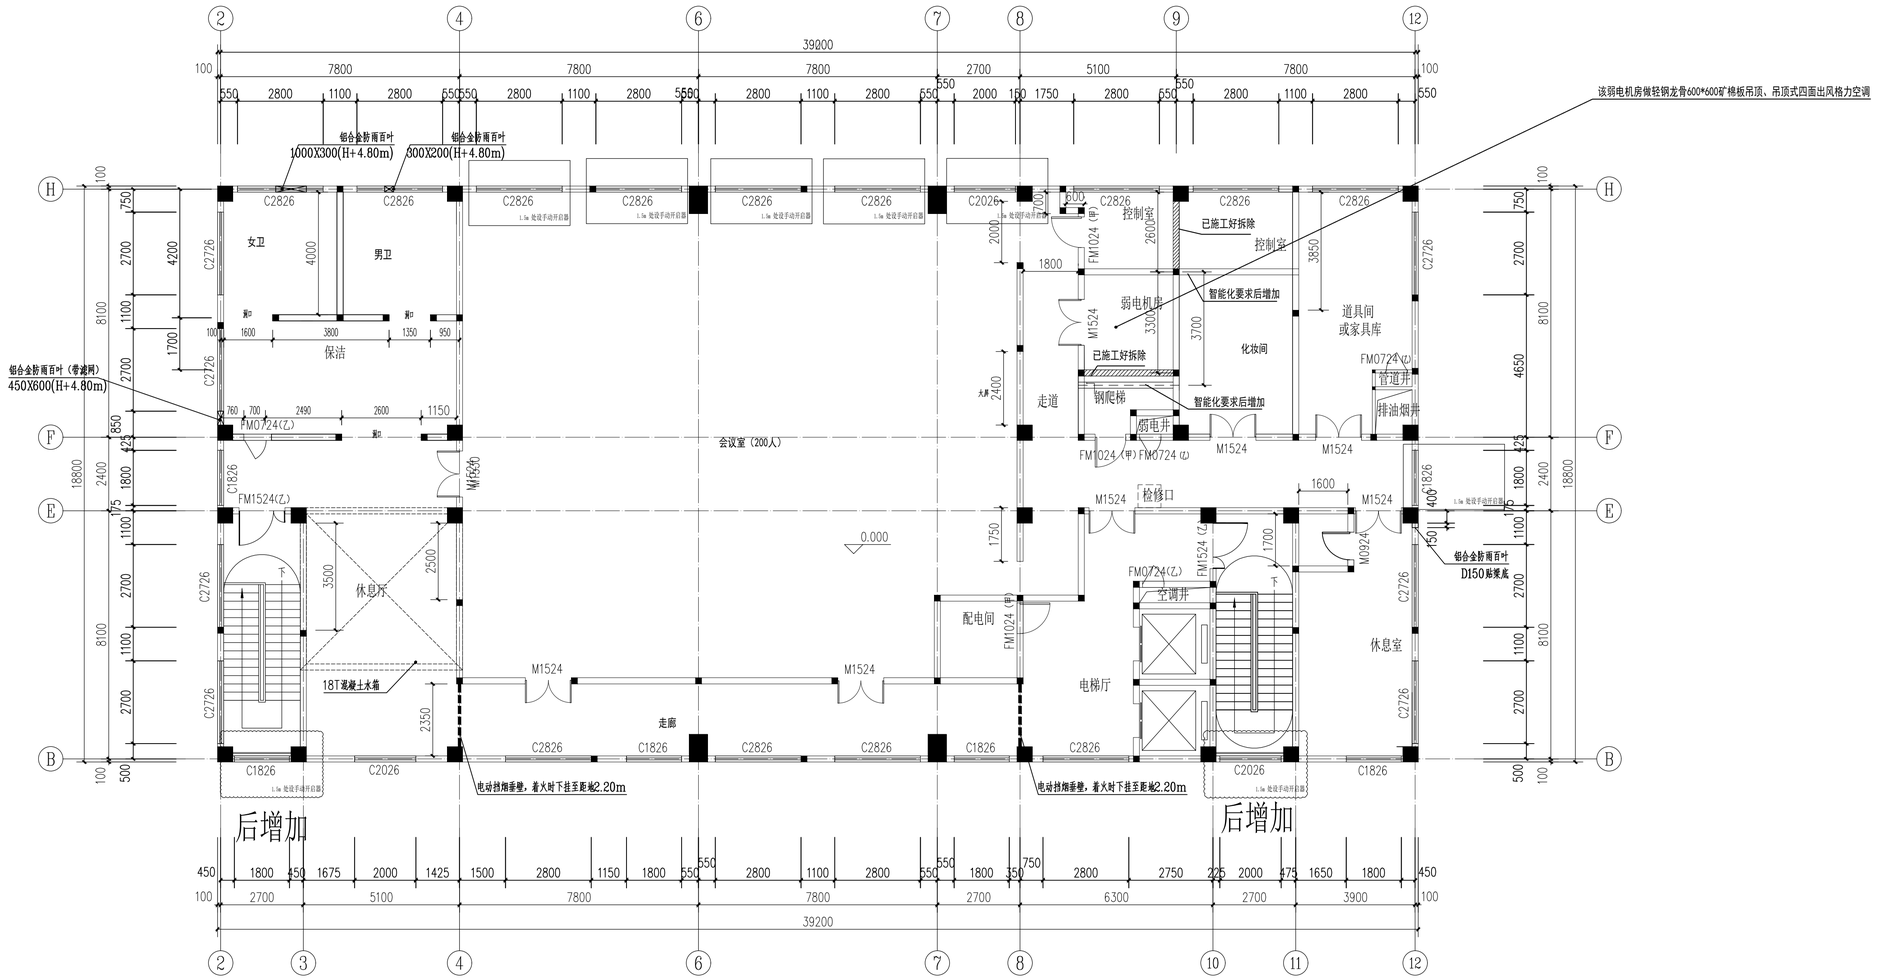

地暖范围：结构标高低于建筑标高120mm

降板范围：结构标高低于建筑标高400mm

四层平面图 1:100

建筑面积：736.96平方米

1、图中标注均为GZ，做法为结构图号T2中图9-7构造柱
2、图中所有门窗侧边均设边框柱，做法为结构图号T2中图9-8构造柱,门侧边框柱高度从楼面至过梁顶，窗侧边框柱高度从窗台压顶至过梁顶
3、外墙在窗台部位设通长混凝土带一道，做法为b*h=200*120，主筋3?C10，分布筋?C6@200,外墙在窗头过梁相同底标高部位设通长水平系梁一道，做法为结构图号T2中图9-4,内墙在门头过梁相同底标高部位和+14.98米部位设通长水平系梁一道，做法为结构图号T2中图9-4

备注栏

设计单位

杭州园林设计院股份有限公司
HANGZHOU LANDSCAPE ARCHITECTURE DESIGN INSTITUTE CO, LTD
建筑、风景园林甲级:A133013139
规划乙级:城规编（142056）
市政乙级:A233013139
文物保护工程勘察设计乙级:0102SJ0002
公司地址：杭州市西湖区双龙街138号西湖世纪中心5号楼南楼
电话：0571-87031011　　传真：0571-87031092　　网址：www.hzyly.com

建设单位	江苏茂源电气有限公司
工程总称	云创中心生产综合楼
子项名称	生产综合楼
图纸名称	四层平面图

	姓 名	签 名
审 定		
审 核		
项目负责人		
专业负责人		
设 计		
制 图		
校 对		

执业专用章


按规定加盖

出图章

未盖出图专用章无效

工号	25-14	图别	建施
图号	08	修改版次	
日期	2025.12		

专业会签栏：弱电 / 电气 / 暖通 / 结构 / 给排水 / 园林 / 建筑

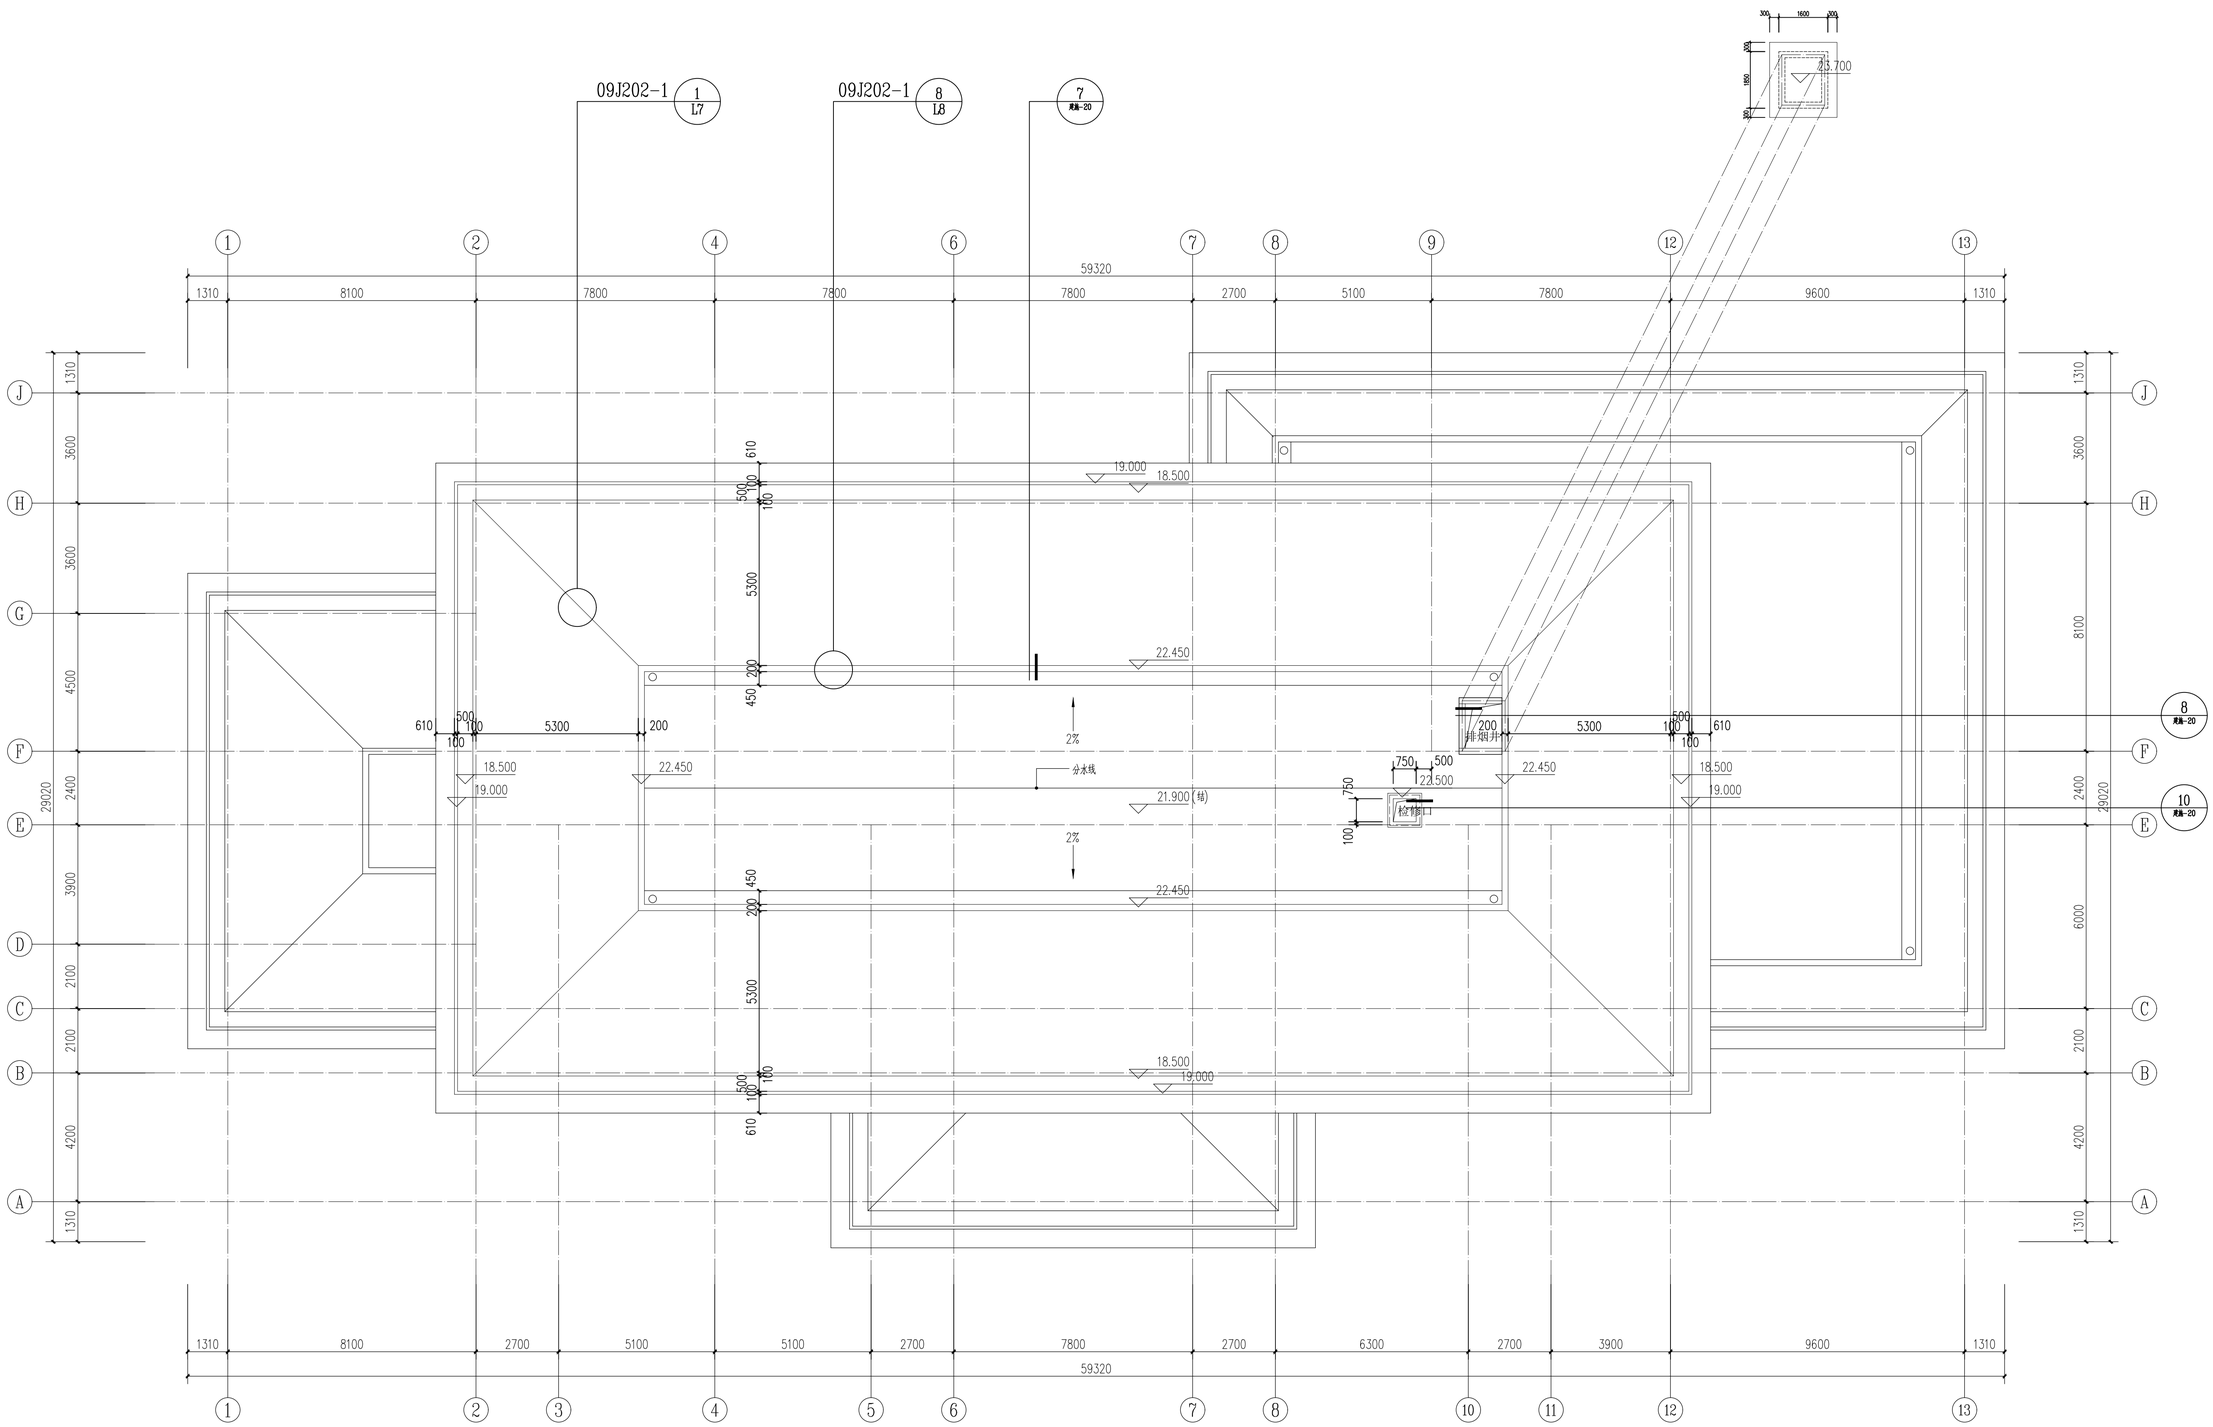

屋顶平面图 1:100

北

备注栏

设计单位

杭州园林设计院股份有限公司
HANGZHOU LANDSCAPE ARCHITECTURE DESIGN INSTITUTE CO.,LTD
建筑、风景园林甲级:A133013139
规划乙级:城规编(142056)
市政乙级:A233013136
文物保护工程勘察设计乙级:0102SJ00002
公司地址:杭州市西湖区双龙街136号西溪世纪中心2号楼南楼
电话:0571-87031011 传真:0571-87031002 网址:www.hzyls.com

建设单位	江苏茂源电气有限公司
工程总称	云创中心生产综合楼
子项名称	生产综合楼
图纸名称	屋顶平面图

	姓 名	签 名
审 定		
审 核		
项目负责人		
专业负责人		
设 计		
制 图		
校 对		

执业专用章

按规定加盖

出图章

未盖出图专用章无效

工号	25-14	图别	建施
图号	09	修改版次	
日期	2025.12		

专业会签栏

园林	建筑
结构	给排水
电气	暖通
	弱电


专业会签栏

园林 建筑

结构 给排水

电气 暖通

弱电

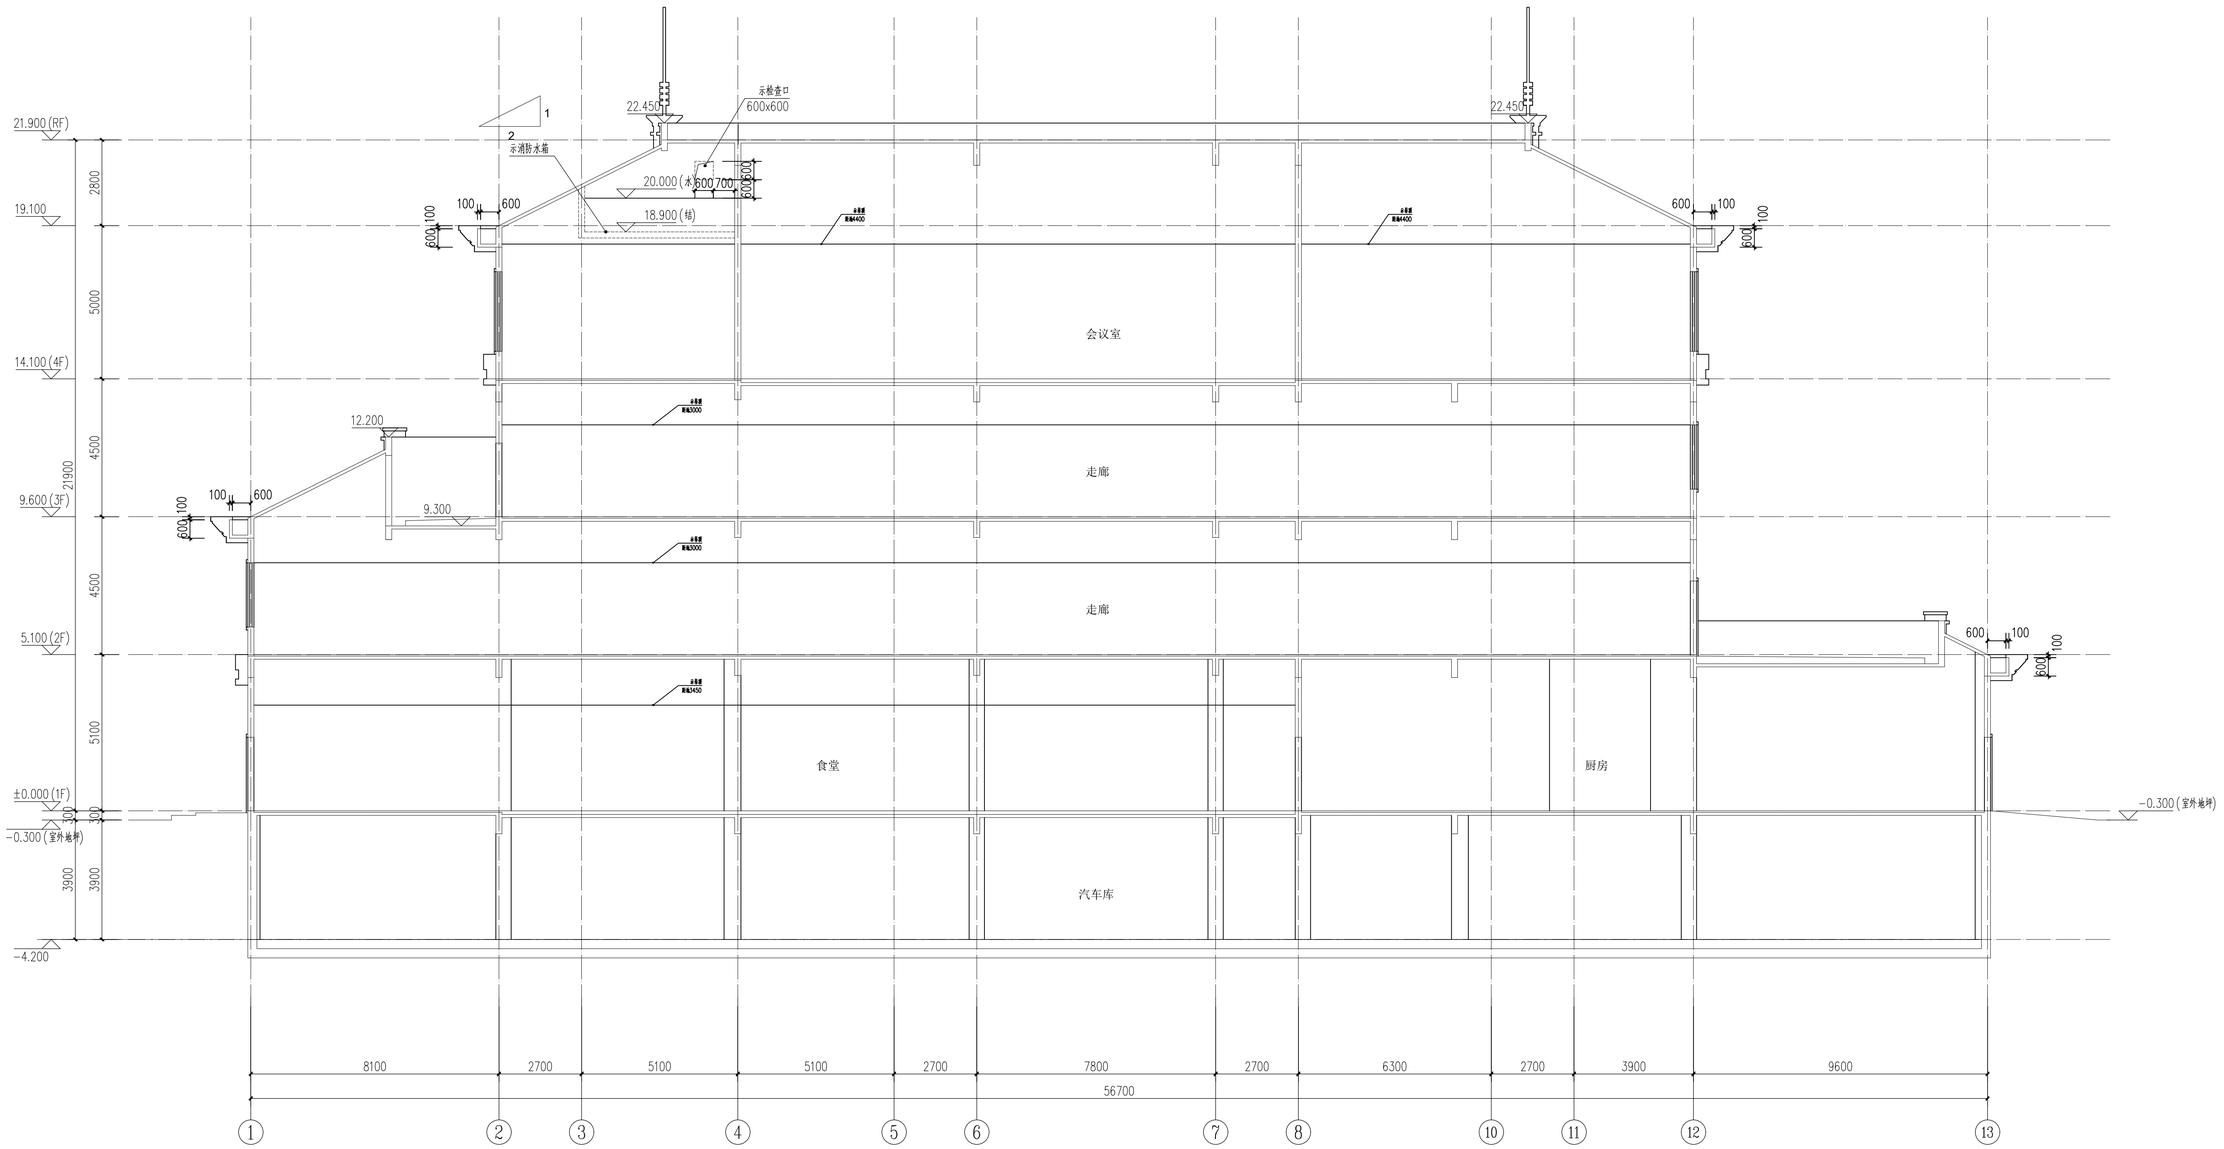

1-1剖面图 1:100

备注栏

设计单位

杭州园林设计院股份有限公司

HANGZHOU LANDSCAPE ARCHITECTURE DESIGN INSTITUTE CO.,LTD

建筑、风景园林甲级:A133013139

规划乙级:城规编(142056)

市政乙级:A233013136

文物保护工程勘察设计乙级:0102SJ00002

公司地址:杭州市西湖区双龙街36号西溪世纪中心2号楼南楼

电话:0571-87631011 传真:0571-87631002 网址:www.hzyls.com

建设单位	江苏茂源电气有限公司
工程总称	云创中心生产综合楼
子项名称	生产综合楼
图纸名称	1-1剖面图

	姓 名	签 名
审 定		
审 核		
项目负责人		
专业负责人		
设 计		
制 图		
校 对		

执业专用章


按规定加盖

出图章

未盖出图专用章无效

工号	25-14	图别	建施
图号	10	修改版次	
日期	2025.12		

专业会签栏 | 园林 建筑 | 结构 给排水 | 电气 暖通 | 弱电

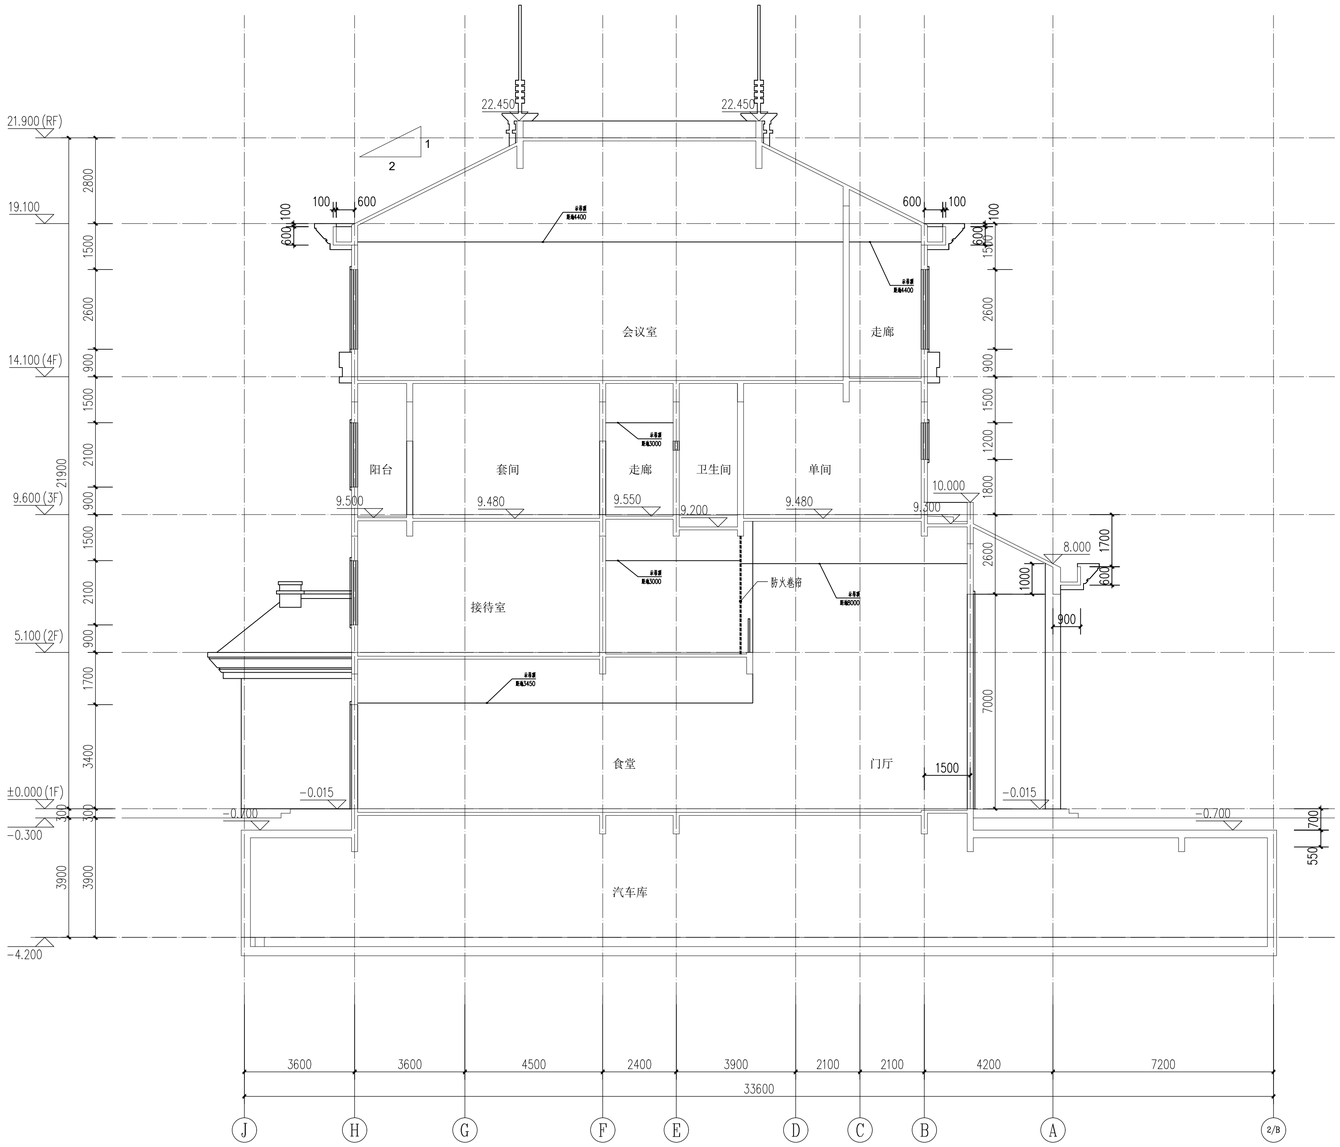

2-2剖面图 1:100

备注栏

设计单位

杭州园林设计院股份有限公司
HANGZHOU LANDSCAPE ARCHITECTURE DESIGN INSTITUTE CO.,LTD
建筑、风景园林甲级:A133013139
规划乙级:城规编(142056)
市政乙级:A233013136
文物保护工程勘察设计乙级:0102SJ0002
公司地址:杭州市西湖区双龙街369号西湖世纪中心2号楼南楼
电话:0571-87031011 传真:0571-87031002 网址:www.hzyly.com

建设单位	江苏茂源电气有限公司
工程总称	云创中心生产综合楼
子项名称	生产综合楼
图纸名称	2-2剖面图

	姓 名	签 名
审 定		
审 核		
项目负责人		
专业负责人		
设 计		
制 图		
校 对		

执业专用章

按规定加盖

出图章

未盖出图专用章无效

工号	25-14	图别	建施
图号	10-2	修改版次	
日期	2025.12		



1-13轴立面图 1:100

备注栏

设计单位

杭州园林设计院股份有限公司
HANGZHOU LANDSCAPE ARCHITECTURE DESIGN INSTITUTE CO.,LTD
建筑、风景园林甲级:A133013139
规划乙级:城规编（142056）
市政乙级:A233013136
文物保护工程勘察设计乙级:0102SJ0002
公司地址：杭州市西湖区双龙街136号西溪世纪中心5号楼南楼
电话：0571-87031011　　传真：0571-87031092　　网址：www.hzyls.com

建设单位	江苏茂源电气有限公司
工程总称	云创中心生产综合楼
子项名称	生产综合楼
图纸名称	立面图1

	姓 名	签 名
审 定		
审 核		
项目负责人		
专业负责人		
设 计		
制 图		
校 对		

执业专用章

按规定加盖

出图章

未盖出图专用章无效

工号	25-14	图别	建施
图号	11	修改版次	
日期	2025.12		

专业会签栏

园林	建筑
结构	给排水
电气	暖通
	弱电

专业会签栏 | 建筑 | 园林 | 给排水 | 结构 | 暖通 | 电气 | 强电 | 弱电



13-1轴立面图 1:100

备注栏

设计单位

杭州园林设计院股份有限公司
HANGZHOU LANDSCAPE ARCHITECTURE DESIGN INSTITUTE CO.,LTD
建筑、风景园林甲级:A133013139
规划乙级:城规编（142056）
市政乙级:A233013136
文物保护工程勘察设计乙级:0102SJ0002
公司地址：杭州市西湖区双龙街130号西溪世纪中心5号楼南楼
电话：0571-87031011　　传真：0571-87031082　　网址：www.hzyly.com

建设单位	江苏茂源电气有限公司	
工程总称	云创中心生产综合楼	
子项名称	生产综合楼	
图纸名称	立面图2	
	姓 名	签 名
审 定		
审 核		
项目负责人		
专业负责人		
设 计		
制 图		
校 对		


执业专用章

按规定加盖

出图章

未盖出图专用章无效

工号	25-14	图别	建施
图号	12	修改版次	
日期	2025.12		

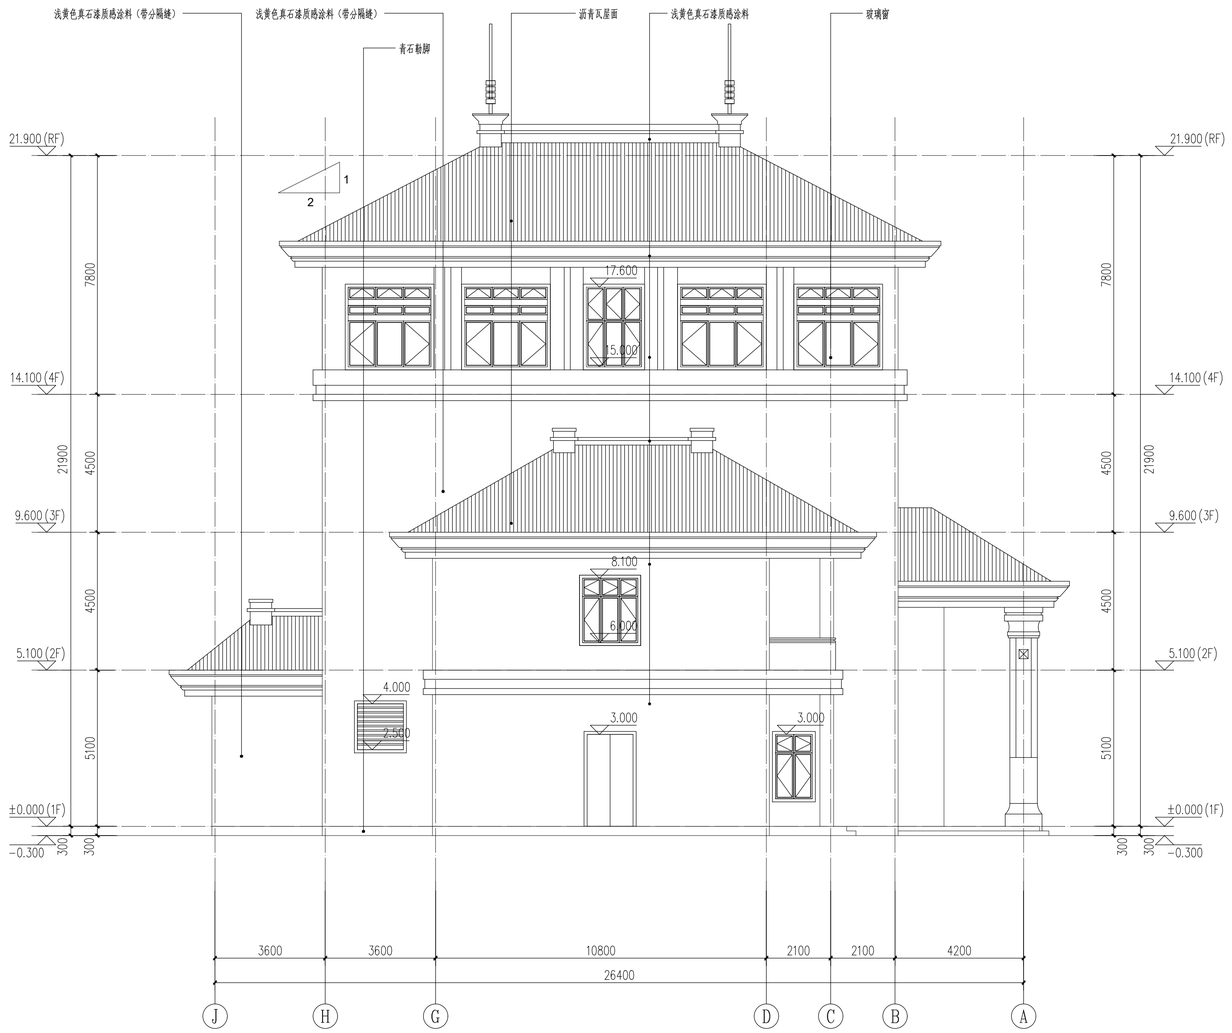

J-A轴立面图 1:100

备注栏

设计单位

杭州园林设计院股份有限公司
HANGZHOU LANDSCAPE ARCHITECTURE DESIGN INSTITUTE CO.,LTD
建筑、风景园林甲级:A133013139
规划乙级:城规编（142056）
市政乙级:A233013136
文物保护工程勘察设计乙级:0102SJ0002
公司地址：杭州市西湖区双龙街136号西溪世纪中心5号楼南楼
电话：0571-87631011　　传真：0571-87631082　　网址：www.hzyly.com

建设单位	江苏茂源电气有限公司
工程总称	云创中心生产综合楼
子项名称	生产综合楼
图纸名称	立面图3

	姓 名	签 名
审 定		
审 核		
项目负责人		
专业负责人		
设 计		
制 图		
校 对		

执业专用章

按规定加盖


出图章

未盖出图专用章无效

工号	25-14	图别	建施
图号	13	修改版次	
日期	2025.12		

专业会签栏

园林	建筑
结构	给排水
电气	暖通
	弱电

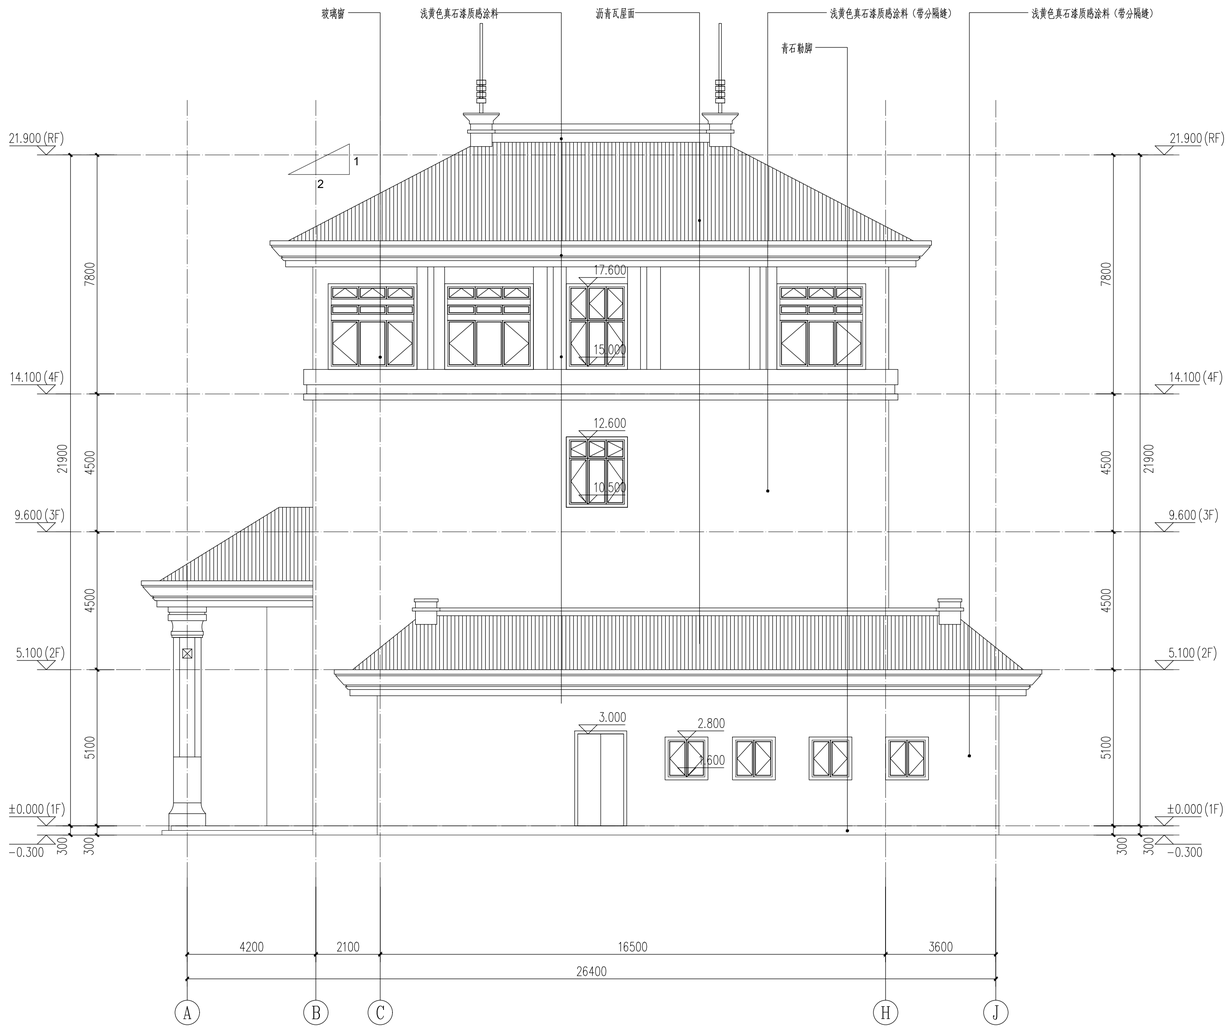

A-J轴立面图 1:100

备注栏

设计单位

杭州园林设计院股份有限公司
HANGZHOU LANDSCAPE ARCHITECTURE DESIGN INSTITUTE CO.,LTD
建筑、风景园林甲级:A133013139
规划乙级:城规编（140056）
市政乙级:A233013136
文物保护工程勘察设计乙级:0102SJ0002
公司地址：杭州市西湖区双龙街58号西溪创业中心5号楼南楼
电话：0571-87031011　　传真：0571-87031002　　网址：www.hzyly.com

建设单位	江苏茂源电气有限公司
工程总称	云创中心生产综合楼
子项名称	生产综合楼
图纸名称	立面图4

	姓 名	签 名
审 定		
审 核		
项目负责人		
专业负责人		
设 计		
制 图		
校 对		


执业专用章

按规定加盖


出图章

未盖出图专用章无效

工号	25-14	图别	建施
图号	14	修改版次	
日期	2025.12		

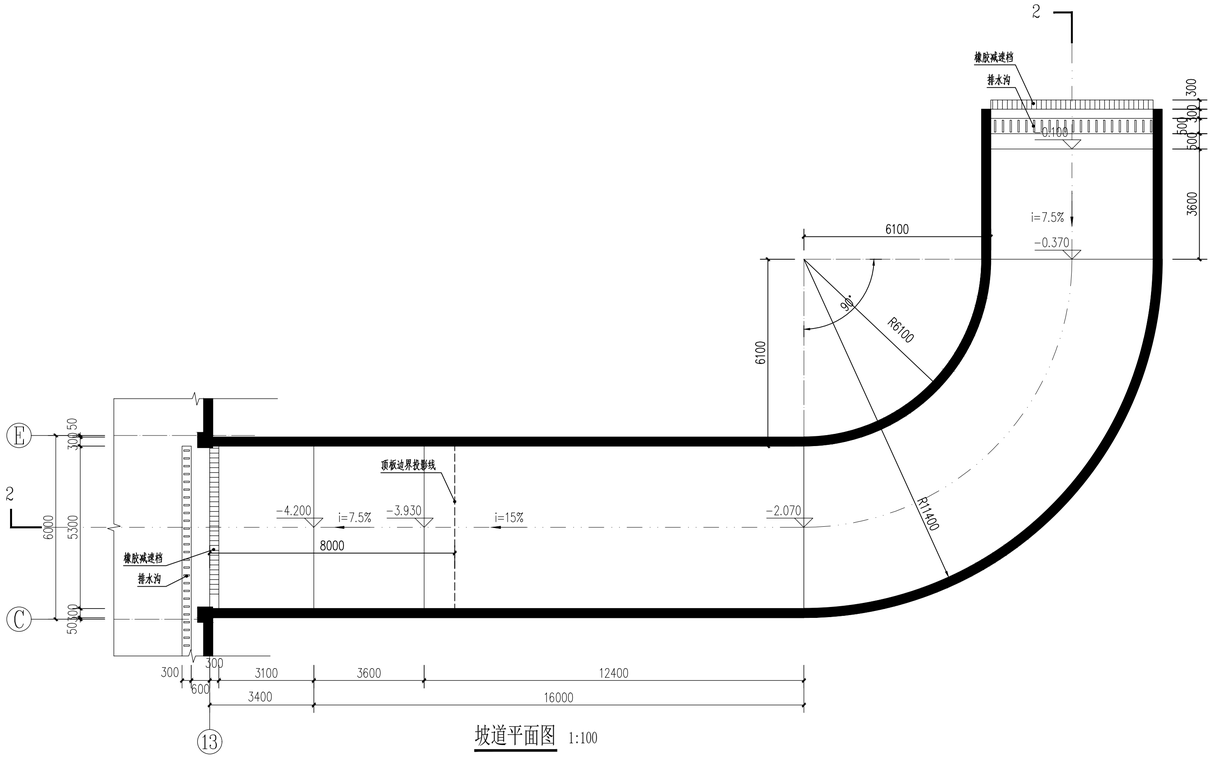

坡道平面图 1:100

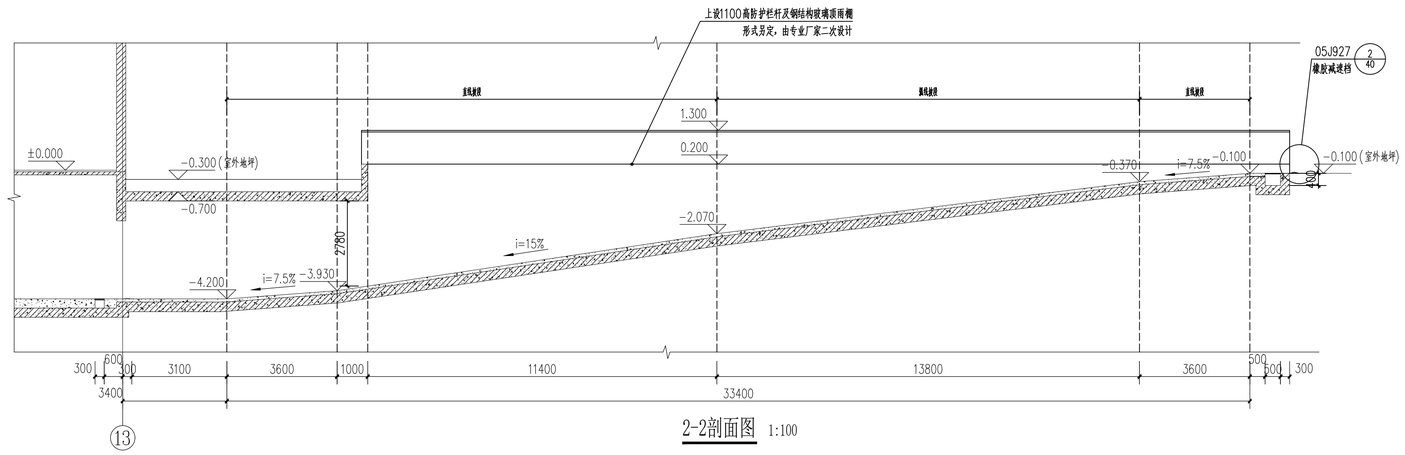

2-2剖面图 1:100

备注栏

设计单位

杭州园林设计院股份有限公司
HANGZHOU LANDSCAPE ARCHITECTURE DESIGN INSTITUTE CO.,LTD
建筑、风景园林甲级:A133013139
规划乙级:城规编（142056）
市政乙级:A233013136
文物保护工程勘察设计乙级:0102SJ0002
公司地址：杭州市西湖区双龙街138号西溪世纪中心5号楼南楼
电话：0571-87031011　　传真：0571-87031082　　网址：www.hzyly.com

建设单位	江苏茂源电气有限公司		
工程总称	云创中心生产综合楼		
子项名称	生产综合楼		
图纸名称	坡道详图		
	姓 名	签 名	
审 定			
审 核			
项目负责人			
专业负责人			
设 计			
制 图			
校 对			

执业专用章

按规定加盖


出图章

未盖出图专用章无效

工号	25-14	图别	建施
图号	15	修改版次	
日期	2025.12		


专业会签栏

园林	建筑
结构	给排水
电气	暖通
	弱电

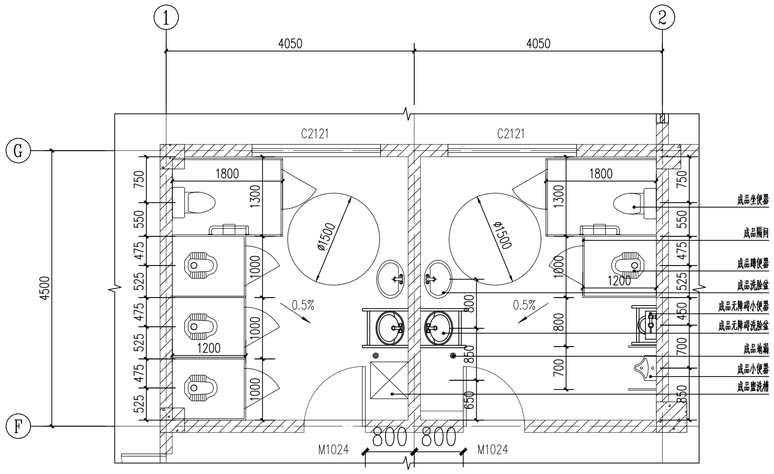


1#卫生间大样 1:50

卫生间地面标高低于同层楼面15mm

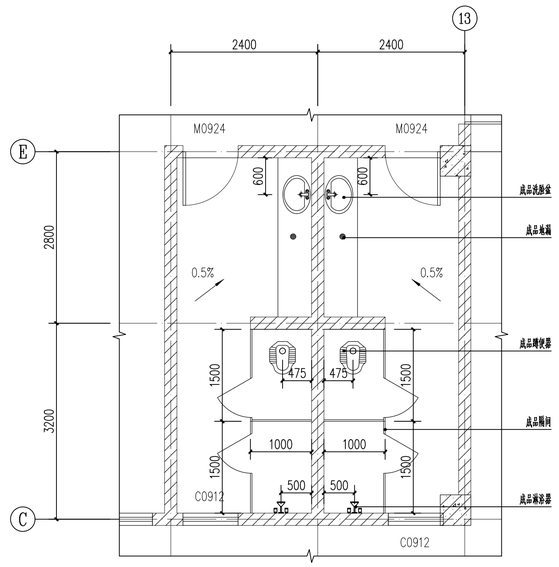


2#卫生间大样 1:50

卫生间地面标高低于同层楼面50mm

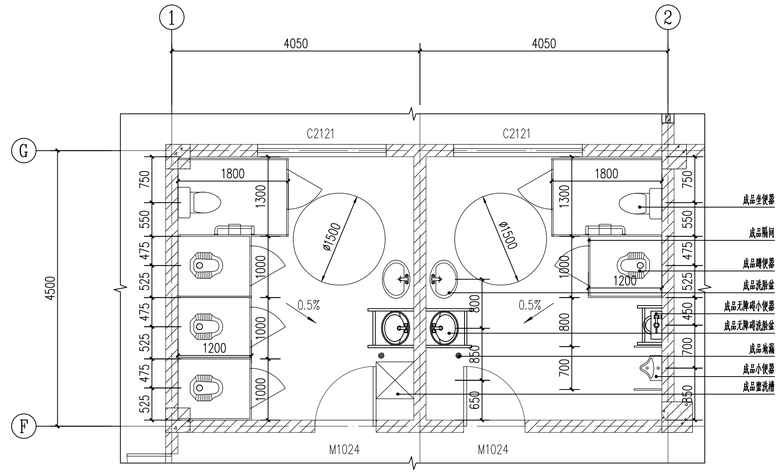


3#卫生间大样 1:50

卫生间地面标高低于同层楼面50mm

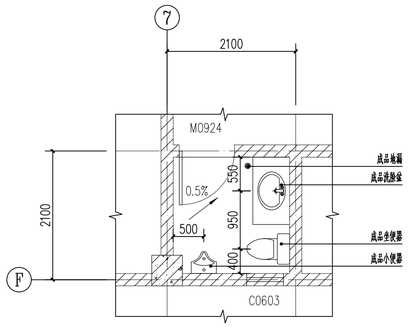


4#卫生间大样 1:50

卫生间地面标高低于同层楼面50mm

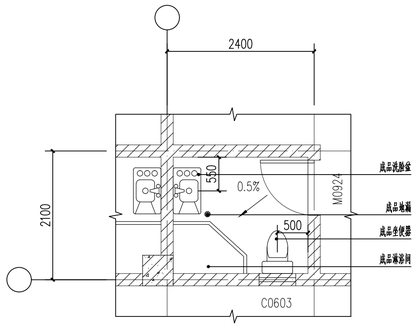


5#卫生间大样 1:50

卫生间地面标高低于同层楼面15mm

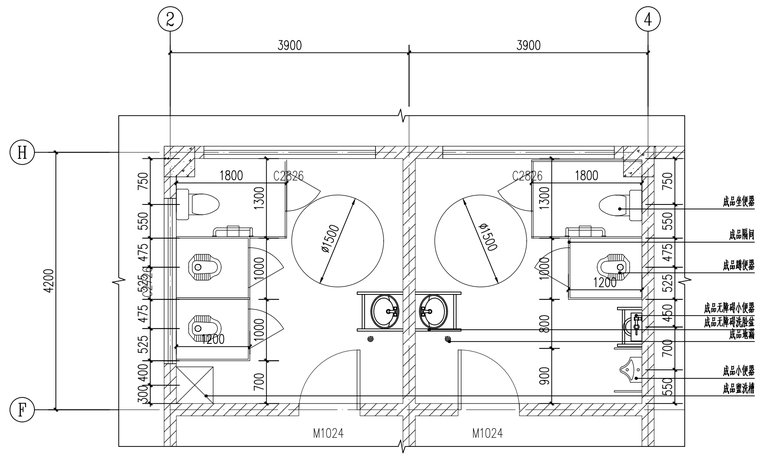

6#卫生间大样 1:50

卫生间地面标高低于同层楼面50mm

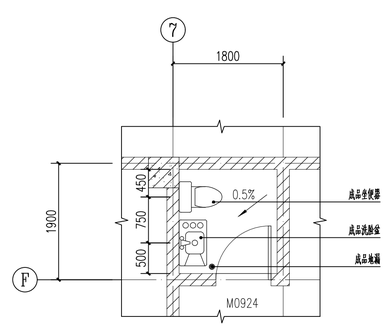

7#卫生间大样 1:50

卫生间地面标高低于同层楼面50mm

备注栏

设计单位

杭州园林设计院股份有限公司

HANGZHOU LANDSCAPE ARCHITECTURE DESIGN INSTITUTE CO.,LTD

建筑、风景园林甲级:A133013139

规划乙级:城规编(142056)

市政乙级:A233013136

文物保护工程勘察设计乙级:0102SJ0002

公司地址:杭州市西湖区双龙街138号西溪世纪中心5号楼南楼

电话:0571-87631011 传真:0571-87631092 网址:www.hzyly.com

建设单位 江苏茂源电气有限公司

工程总称	云创中心生产综合楼
子项名称	生产综合楼
图纸名称	卫生间大样

	姓 名	签 名
审 定		
审 核		
项目负责人		
专业负责人		
设 计		
制 图		
校 对		

执业专用章

按规定加盖

出图章


未盖出图专用章无效

工号	25-14	图别	建施
图号	16	修改版次	
日期	2025.12		


专业会签栏

园林	建筑
结构	给排水
电气	暖通
	弱电


专业会签栏 | 建筑 | 园林 | 给排水 | 结构 | 暖通 | 电气 | 弱电

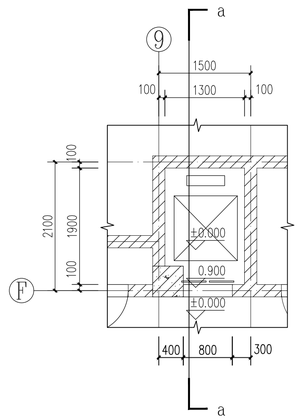


1#食梯井0.000标高平面图 1:50

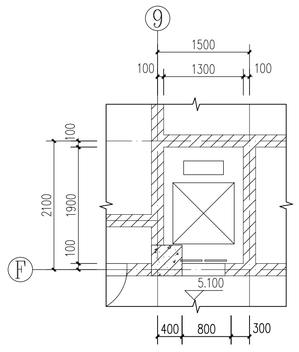


1#食梯井5.100标高平面图 1:50

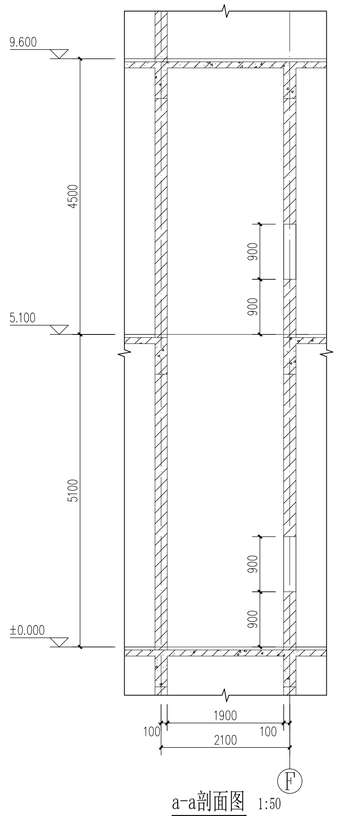


a-a剖面图 1:50

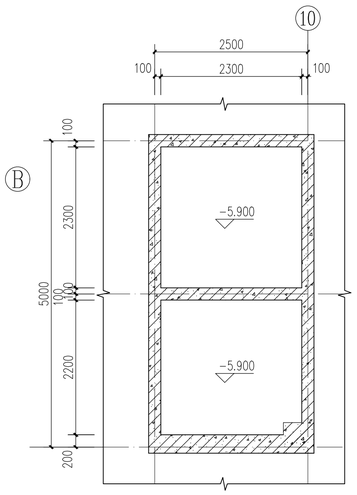


电梯井-5.900标高平面图 1:50

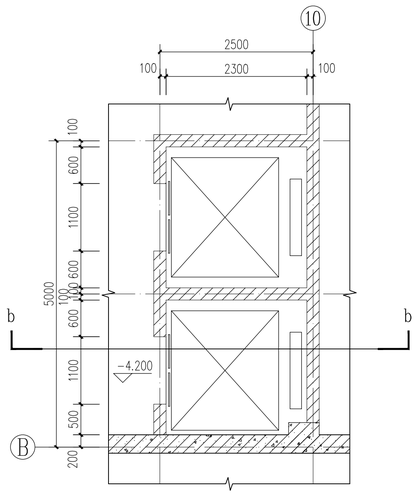

电梯井-4.200标高平面图 1:50

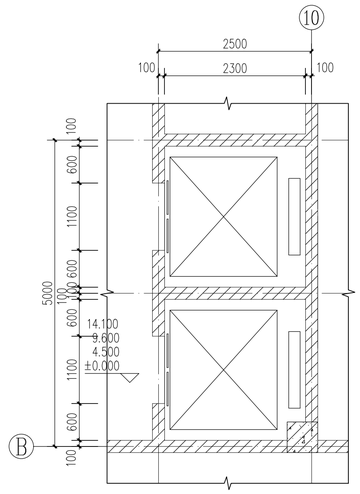

电梯井标准层平面图 1:50

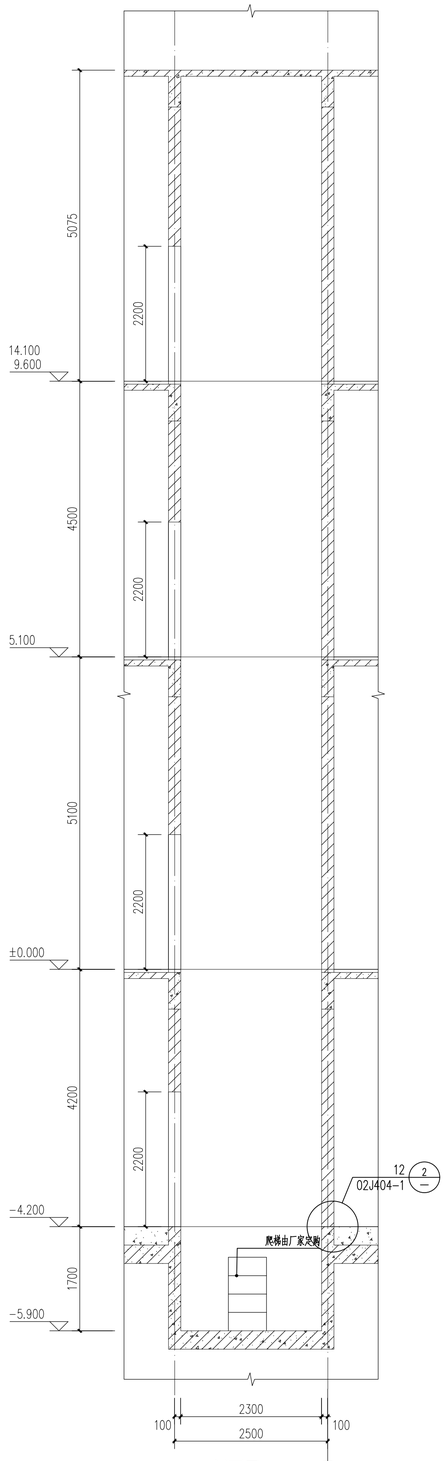

b-b剖面图 1:50

备注栏

设计单位

杭州园林设计院股份有限公司
HANGZHOU LANDSCAPE ARCHITECTURE DESIGN INSTITUTE CO.LTD
建筑、风景园林甲级:A133013139
规划乙级:城规编(142056)
市政乙级:A233013136
文物保护工程勘察设计乙级:0102SJ00002
公司地址:杭州市西湖区双龙街38号西城世纪中心2号楼南楼
电话:0571-87031011 传真:0571-87031002 网址:www.hzylc.com

建设单位	江苏茂源电气有限公司
工程总称	云创中心生产综合楼
子项名称	生产综合楼
图纸名称	电梯井详图

	姓 名	签 名
审 定		
审 核		
项目负责人		
专业负责人		
设 计		
制 图		
校 对		

执业专用章


按规定加盖

出图章


未盖出图专用章无效

工号	25-14	图别	建施
图号	17	修改版次	
日期	2025.12		


专业会签栏 | 建筑 | 园林 | 给排水 | 结构 | 暖通 | 电气 | 弱电

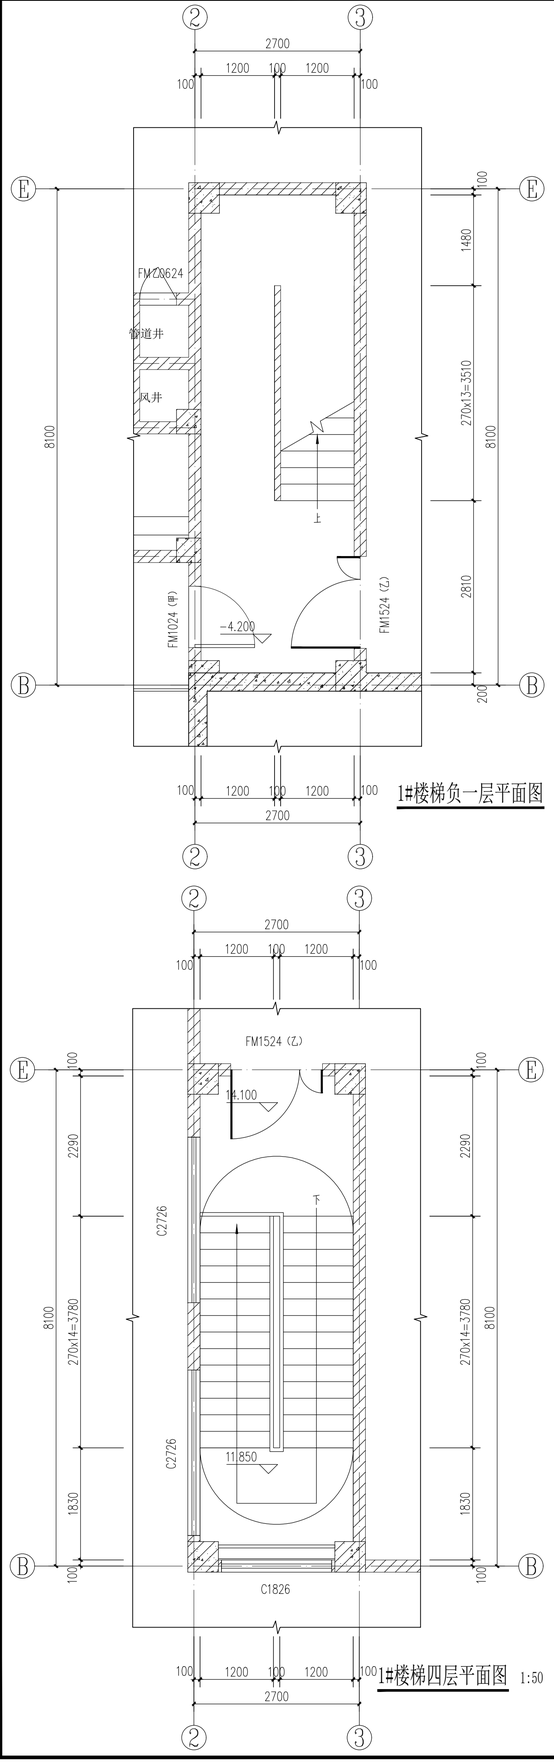


1#楼梯负一层平面图 1:50

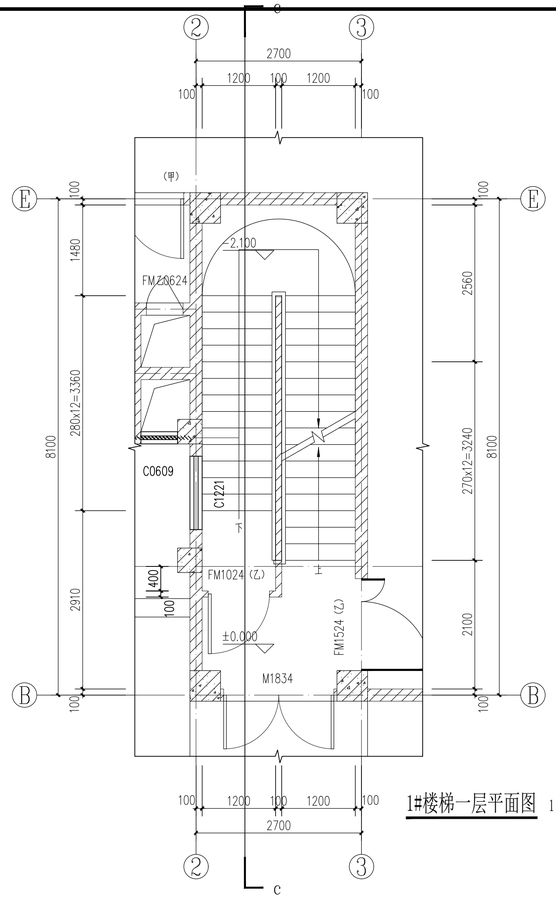

1#楼梯一层平面图 1:50

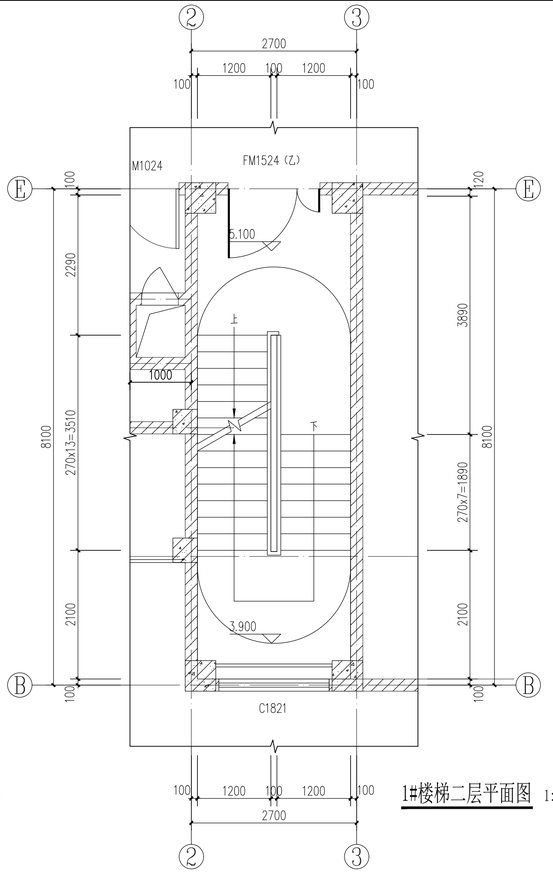


1#楼梯二层平面图 1:50

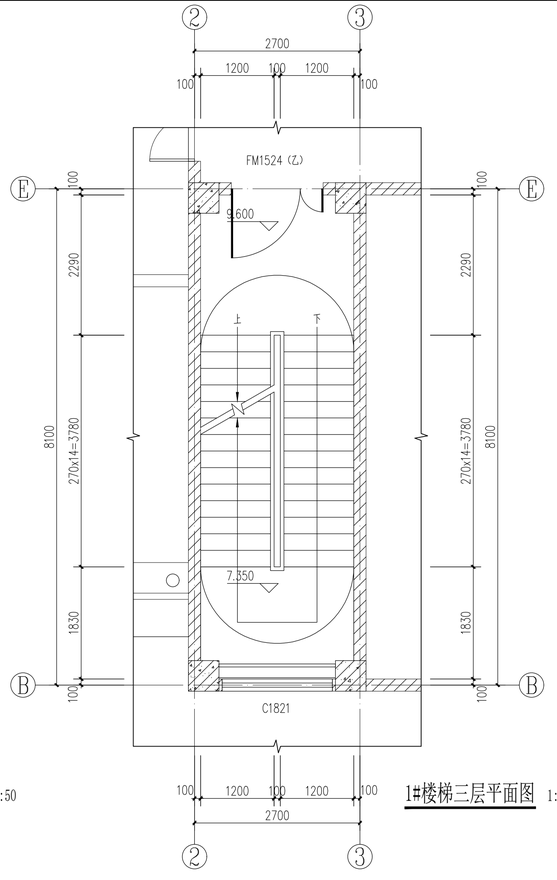

1#楼梯三层平面图 1:50

1#楼梯四层平面图 1:50

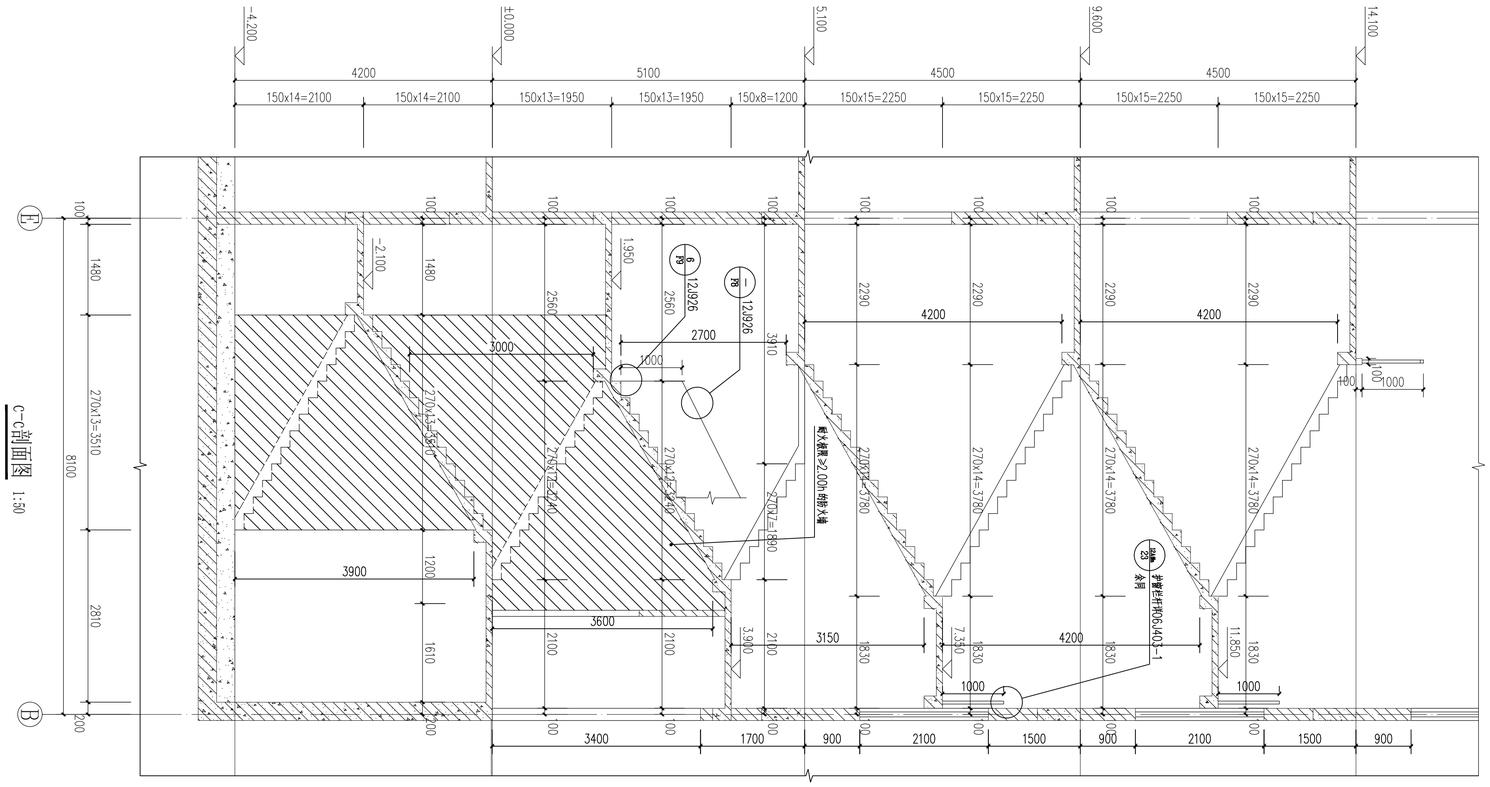

c-c剖面图 1:50

备注栏

设计单位

杭州园林设计院股份有限公司
HANGZHOU LANDSCAPE ARCHITECTURE DESIGN INSTITUTE CO.,LTD
建筑、风景园林甲级:A133013139
规划乙级:城规编(142056)
市政乙级:A233013136
文物保护工程勘察设计乙级:0102SJ0002
公司地址:杭州市西湖区双龙街136号西溪世纪中心5号楼南楼
电话:0571-87031011 传真:0571-87031082 网址:www.hzyls.com

建设单位	江苏茂源电气有限公司
工程总称	云创中心生产综合楼
子项名称	生产综合楼
图纸名称	1#楼梯详图

	姓 名	签 名
审 定		
审 核		
项目负责人		
专业负责人		
设 计		
制 图		
校 对		


执业专用章

按规定加盖


出图章

未盖出图专用章无效


工号	25-14	图别	建施
图号	18	修改版次	
日期	2025.12		

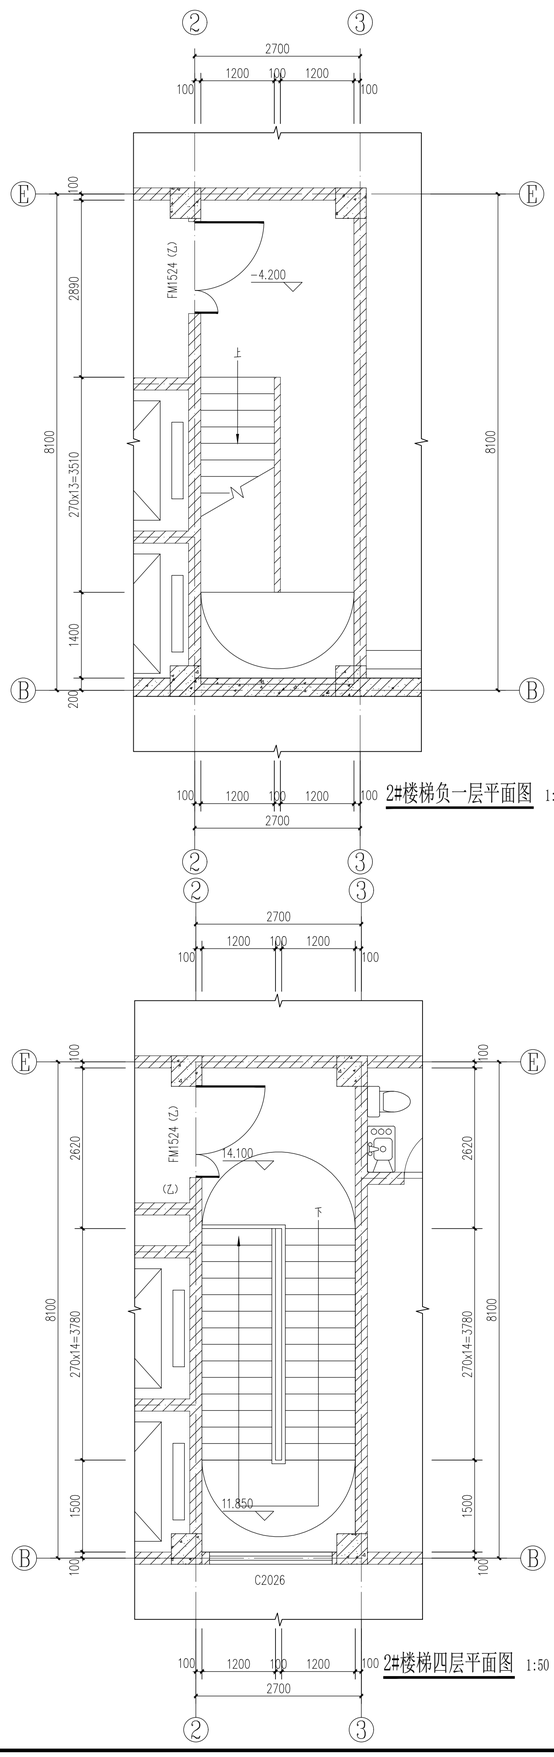


2#楼梯负一层平面图 1:50

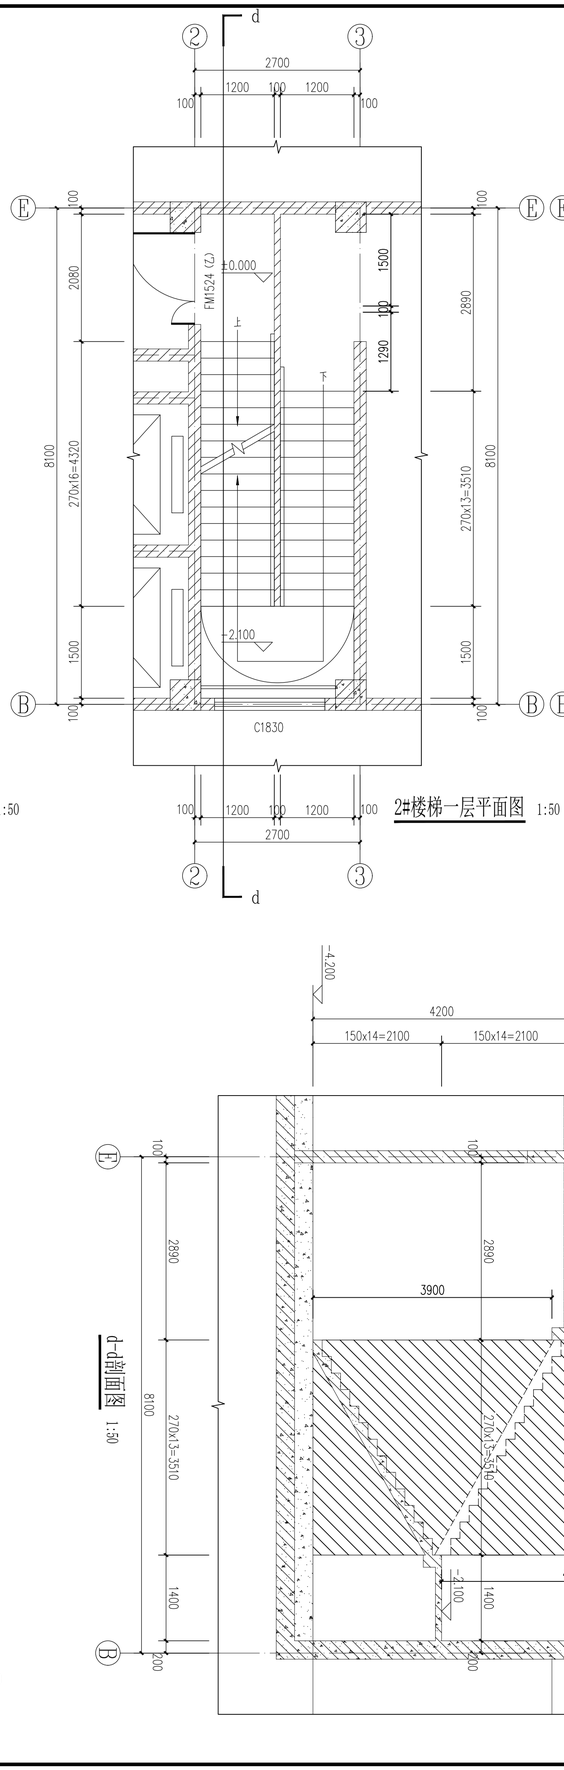

2#楼梯一层平面图 1:50

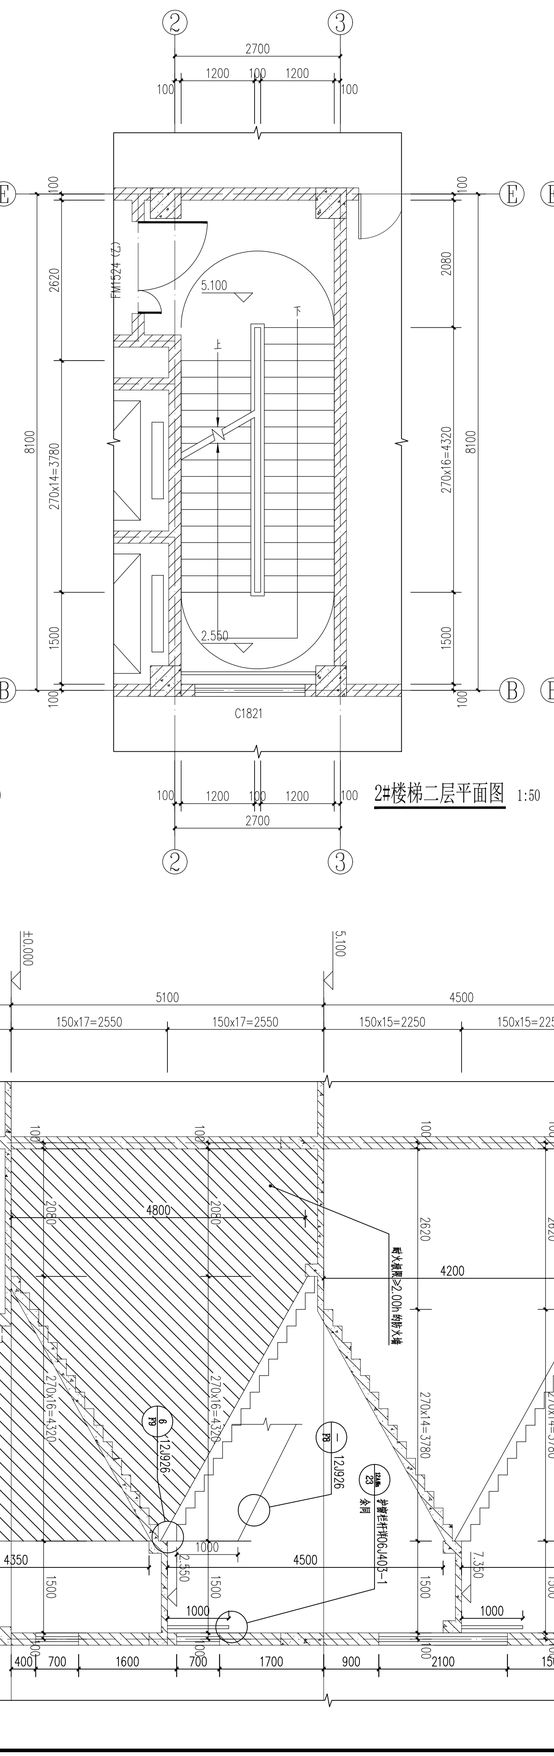


2#楼梯二层平面图 1:50

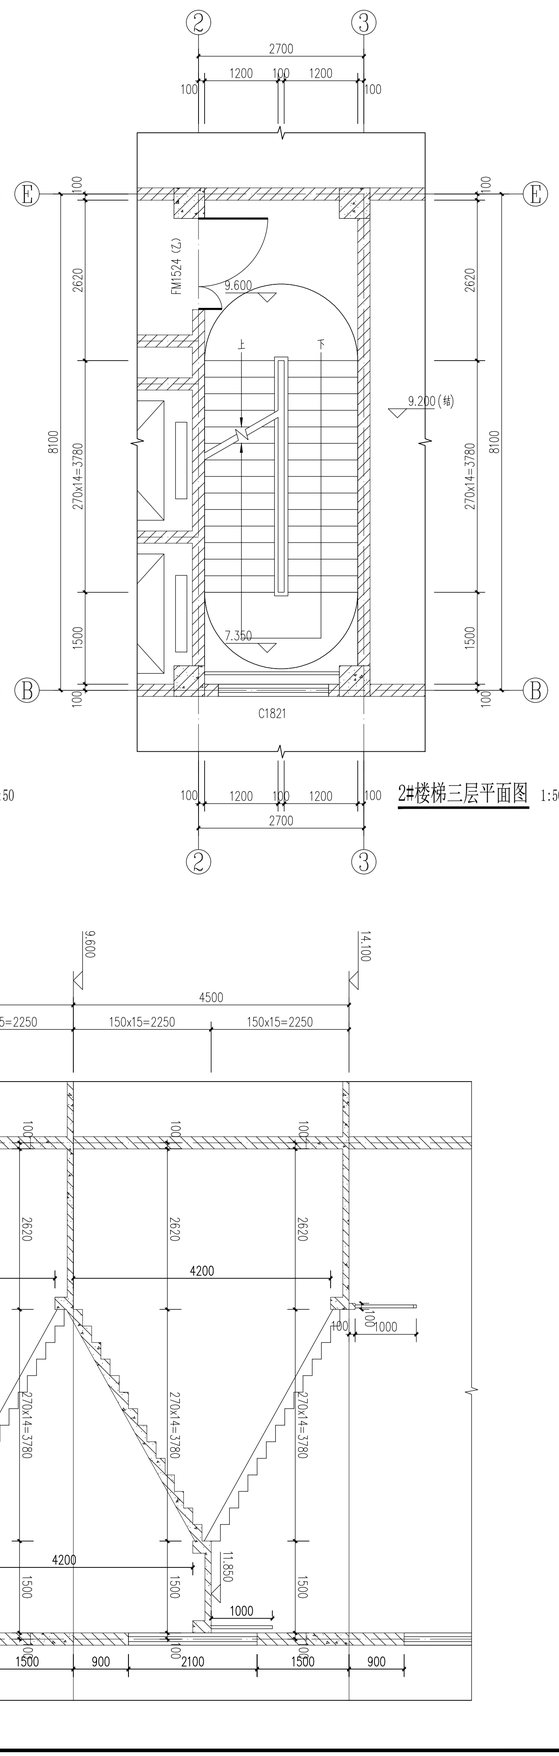

2#楼梯三层平面图 1:50

2#楼梯四层平面图 1:50

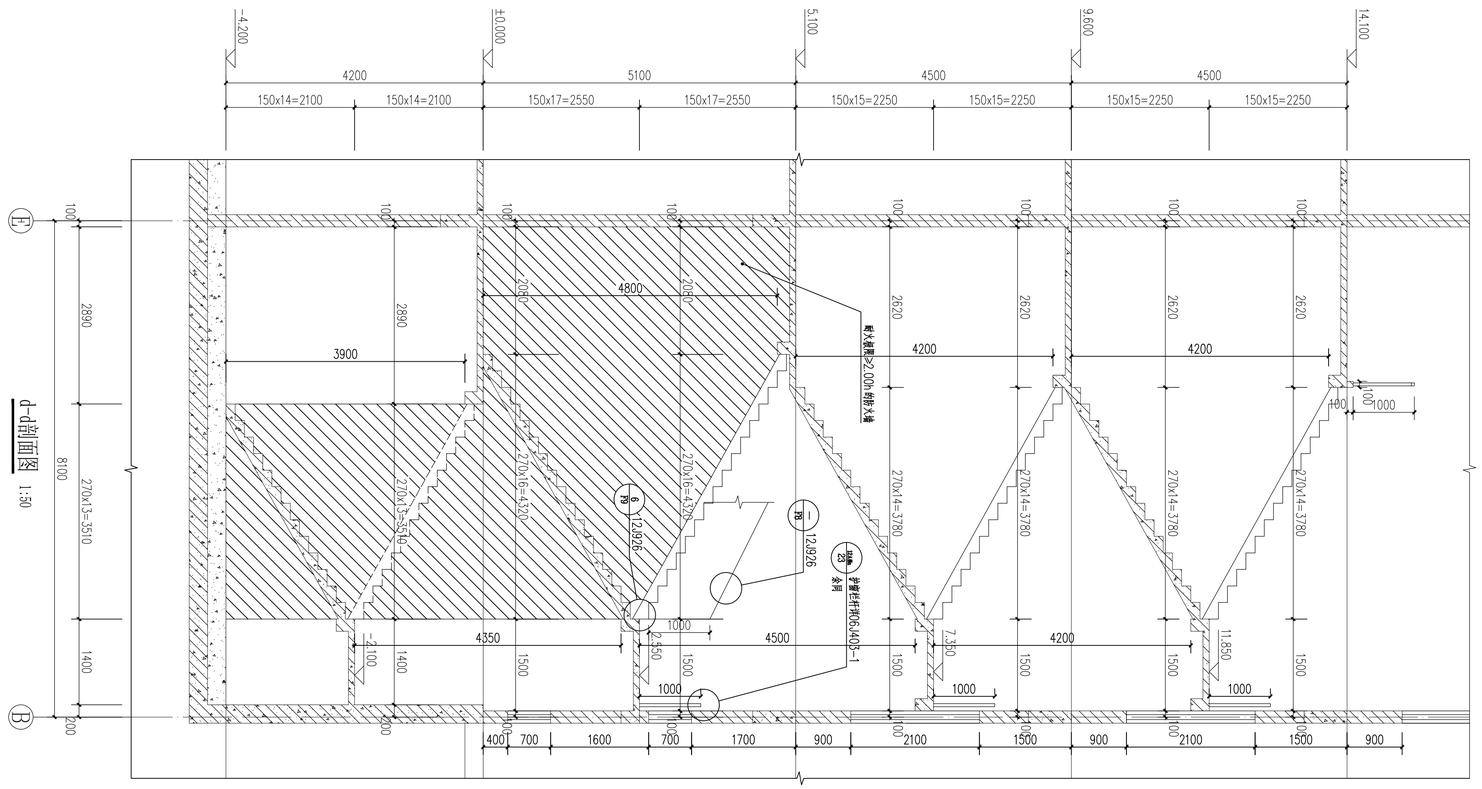

d-d剖面图 1:50

备注栏

设计单位

杭州园林设计院股份有限公司
HANGZHOU LANDSCAPE ARCHITECTURE DESIGN INSTITUTE CO.,LTD
建筑、风景园林甲级:A133013139
规划乙级:城规编(142056)
市政乙级:A233013136
文物保护工程勘察设计乙级:0102S3000Q
公司地址:杭州市西湖区双龙街38号西湖世纪中心2号楼南楼
电话:0571-87031011 传真:0571-87031002 网址:www.hzylc.com

建设单位	江苏茂源电气有限公司
工程总称	云创中心生产综合楼
子项名称	生产综合楼
图纸名称	2#楼梯详图

	姓 名	签 名
审 定		
审 核		
项目负责人		
专业负责人		
设 计		
制 图		
校 对		

执业专用章

按规定加盖


出图章


未盖出图专用章无效


工号	25-14	图别	建施
图号	19	修改版次	
日期	2025.12		


专业会签栏


园林	建筑
结构	给排水
电气	暖通
	弱电

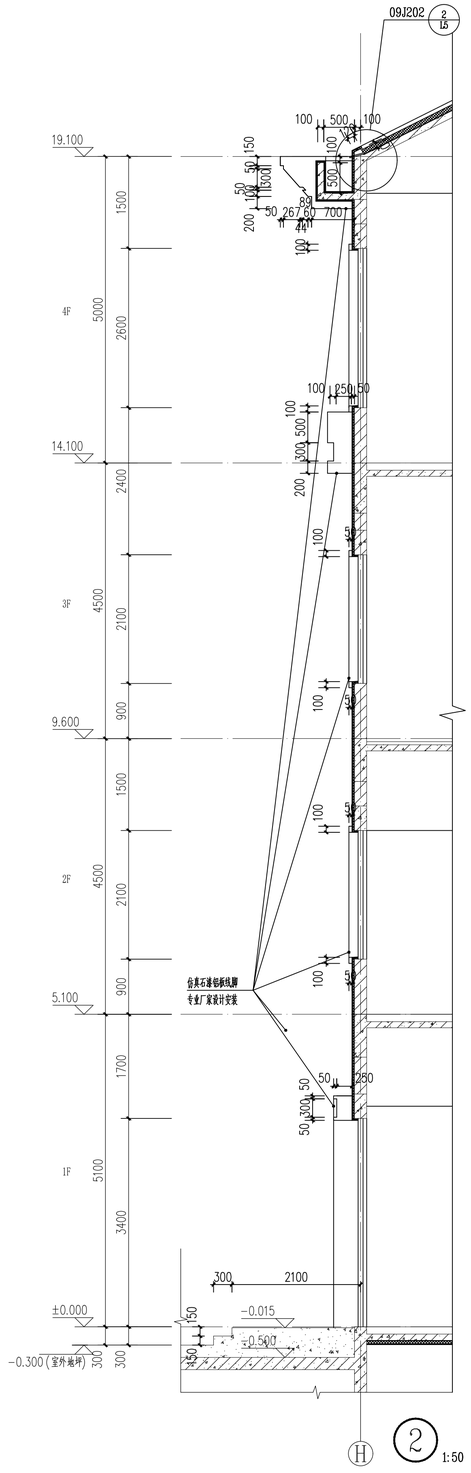


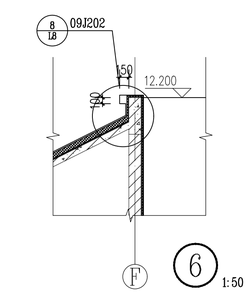


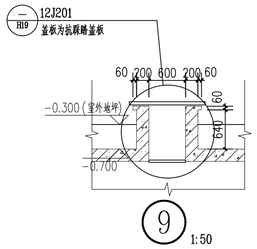


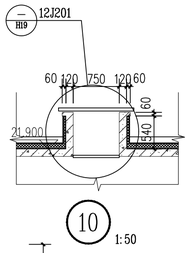


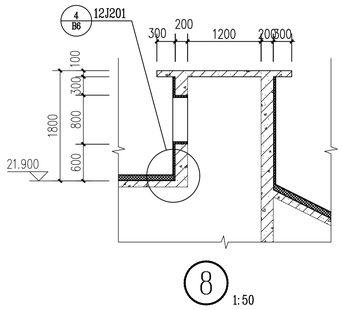


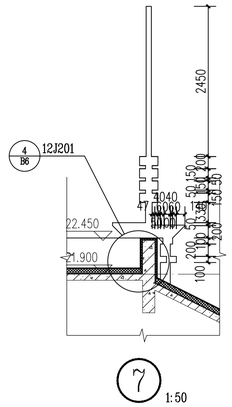

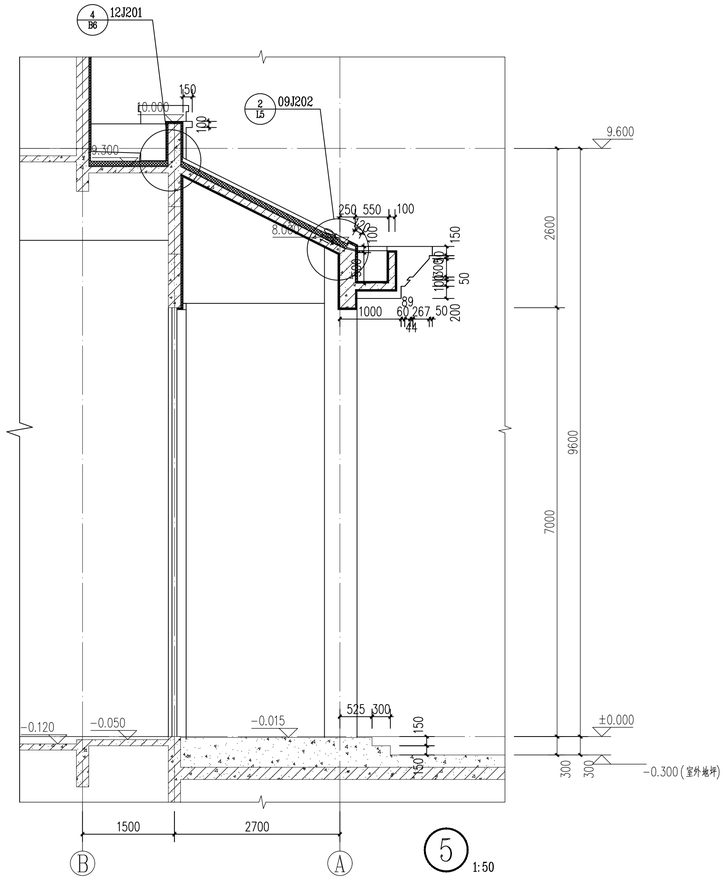

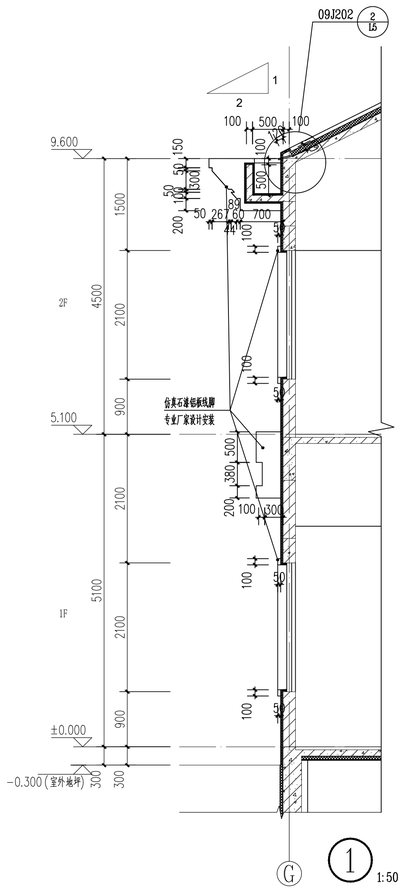

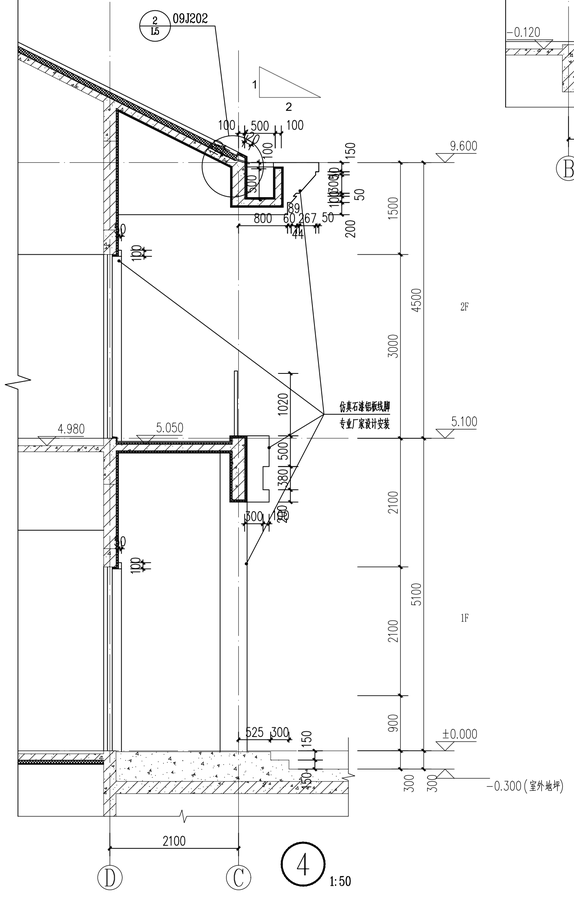

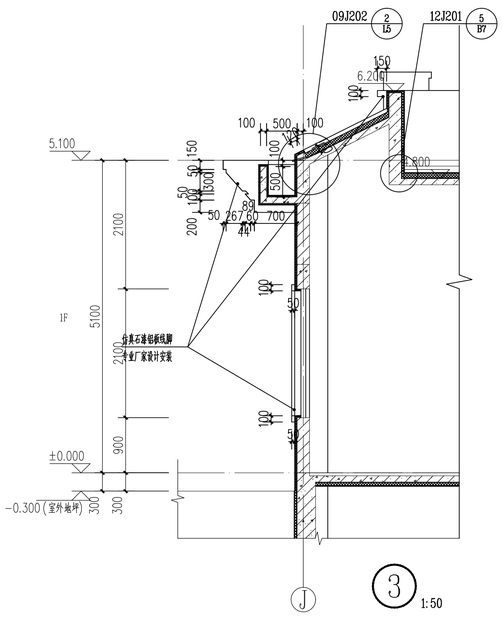

备注栏

设计单位
杭州园林设计院股份有限公司
HANGZHOU LANDSCAPE ARCHITECTURE DESIGN INSTITUTE CO.,LTD
建筑、风景园林甲级:A133013139
规划乙级:城规编(142056)
市政乙级:A233013136
文物保护工程勘察设计乙级:0102SJ0002
公司地址:杭州市西湖区双龙街138号西溪世纪中心5号楼南楼
电话:0571-87031011 传真:0571-87031002 网址:www.hzyly.com

建设单位	江苏茂源电气有限公司
工程总称	云创中心生产综合楼
子项名称	生产综合楼
图纸名称	墙身大样

	姓 名	签 名
审 定		
审 核		
项目负责人		
专业负责人		
设 计		
制 图		
校 对		

执业专用章

按规定加盖

出图章


未盖出图专用章无效

工号	25-14	图别	建施
图号	20	修改版次	
日期	2025.12		

门窗表

类别	设计编号	洞口尺寸(mm) 宽度	洞口尺寸(mm) 高度	数量	图集名称	页次	选用型号	备注
普通门	M0924	900	2400	15				
	M1024	1000	2400	30				
	M1224	1200	2400	2				
	M1524	1500	2400	10				
铝合金门	LM1024	1000	2400	1				
	LM1530	1500	3000	6				
	LM1834	1800	3400	1				
	LM2034	2000	3400	1				
铝推拉门	LTM3024	3000	2400	6				
甲级防火门	FM1024（甲）	1000	2400	10				
	FM1524（甲）	1500	2400	3				
乙级防火门	FM0724（乙）	700	2400	16				
	FM1024（乙）	1000	2400	2				
	FM1524（乙）	1500	2400	11				
幕墙	MQ1	13000	7000	1				隐框玻璃幕墙，开启窗为平推窗，1.5m处设手动开启器
普通窗	C0603	600	300	9				
	C0912	900	1200	2				
	C1212	1200	1200	7				
	C1216	1200	1600	1				
	C1221	1200	2100	1				
	C1807	1800	700	1				
	C1812	1800	1200	2				
	C1821	1800	2100	14				1.5m处设手动开启器
	C1826	1800	2600	6				1.5m处设手动开启器
	C1830	1800	3000	4				1.5m处设手动开启器
	C2026	2000	2600	3				1.5m处设手动开启器
	C2112	2100	1200	2				
	C2121	2100	2100	29				
	C2130	2100	3000	5				1.5m处设手动开启器
	C2726	2700	2600	7				1.5m处设手动开启器
	C2826	2800	2600	13				1.5m处设手动开启器
百叶窗	BYC0609	600	900	1				
	BYC1515	1500	1500	1				

注：1. 各种型号门窗的数量应与工程现场实际核对，本图所注皆为洞口尺寸，门窗制作时均需扣去部分装饰厚度。
2. 单块面积大于1.5㎡的玻璃采用安全玻璃。
3. 落地玻璃门窗上设明显防碰撞标志。
4. 所有门窗均由施工单位提供制作设计图，经设计单位认可后方可制作安装。

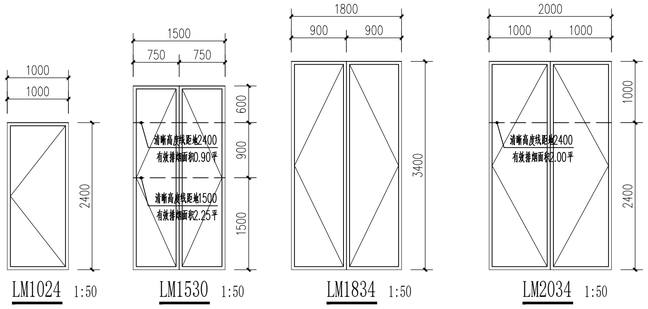


LM1024 1:50


LM1530 1:50

LM1834 1:50


LM2034 1:50

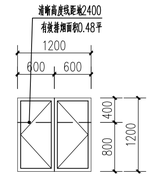


C1212 1:100

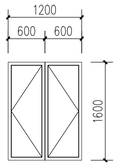


C1216 1:100

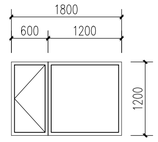


C1812 1:100

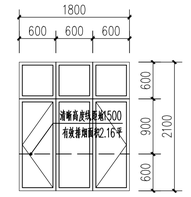


C1821 1:100

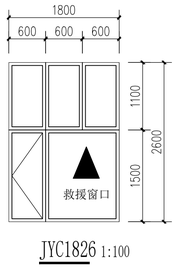


JYC1826 1:100

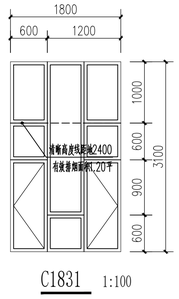


C1831 1:100

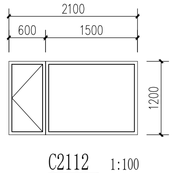


C2112 1:100

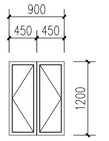


C0912 1:100

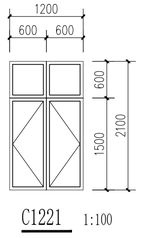


C1221 1:100

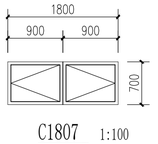


C1807 1:100

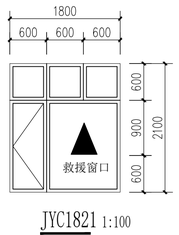


JYC1821 1:100

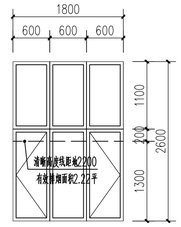


C1826 1:100

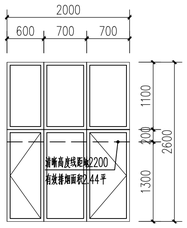


C2026 1:100

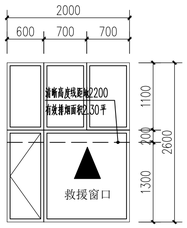


JYC2026 1:100

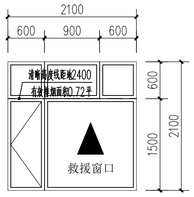


JYC2121 1:100

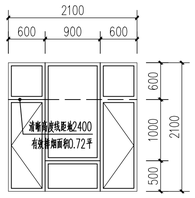


C2121 1:100

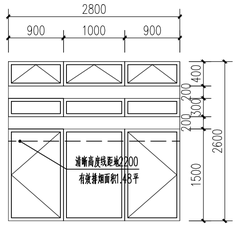


C2826 1:100

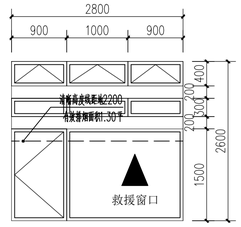


JYC2826 1:100

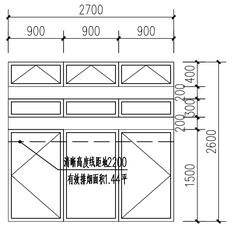


C2726 1:100

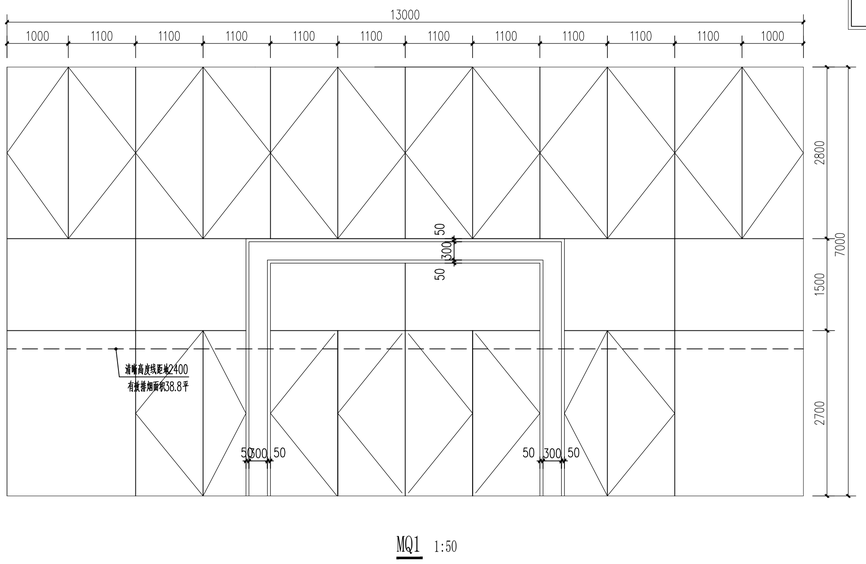


MQ1 1:50

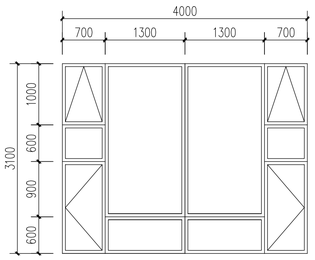


C4031 1:100

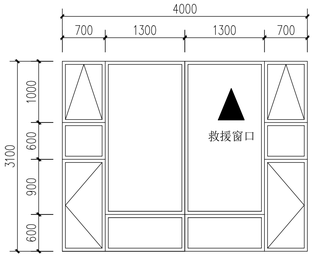


JYC4031 1:100

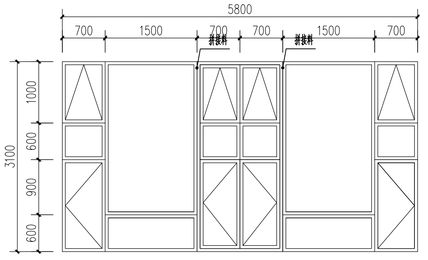


C5831 1:100

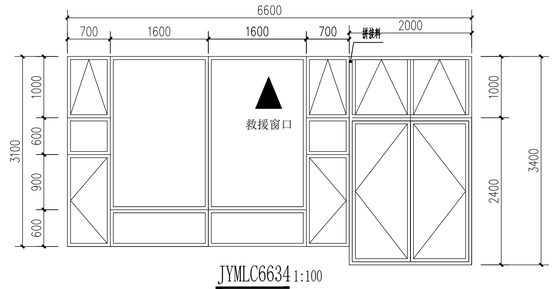

JYMLC6634 1:100

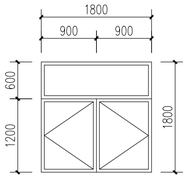

C1818 1:100

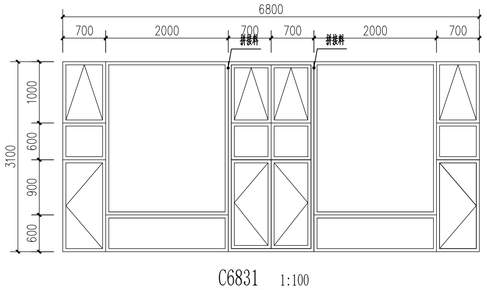

C6831 1:100

备注栏

设计单位

杭州园林设计院股份有限公司
HANGZHOU LANDSCAPE ARCHITECTURE DESIGN INSTITUTE CO.,LTD
建筑、风景园林甲级:A133013139
预划乙级:城规编（1420356）
市政乙级:A233013136
文物保护工程勘察设计乙级:0102SJ0002
公司地址：杭州市西湖区双龙街138号西湖世纪中心5号楼南楼
电话：0571-87031011　　传真：0571-87031002　　网址：www.hzyly.com

建设单位	江苏茂源电气有限公司
工程总称	云创中心生产综合楼
子项名称	生产综合楼
图纸名称	门窗大样

	姓 名	签 名
审 定		
审 核		
项目负责人		
专业负责人		
设 计		
制 图		
校 对		

执业专用章

按规定加盖

出图章

未盖出图专用章无效

工号	25-14	图别	建施
图号	21	修改版次	
日期	2025.12		

专业会签栏：建筑　园林　结构　给排水　电气　暖通　弱电