# 杭州园林设计院股份有限公司

## 图 纸 目 录

| 建设单位 | 江苏茂源电气有限公司 | 工程编号 | 25-14 |
|---|---|---|---|
| 工程名称 | 云创中心生产综合楼 | 图纸编号 | 结施 |
| 子项名称 | 生产综合楼 | 目录页码 | 共2页 第1页 |

| 图别图号 | 图名 | | 备注 |
|---|---|---|---|
| 结施 T1 | 结构设计总说明一 | A2+ | |
| 结施 T2 | 结构设计总说明二 | A2+ | |
| 结施 T3 | 危险性较大分部分项工程说明（结构专篇） | A2 | |
| 结施 T4 | 江苏省民用建筑施工图绿色设计专篇（结构） | A2 | |
| 结施 01 | 桩位布置平面图 | A1+ | |
| 结施 02 | 承台、底板结构平面图 | A1+ | |
| 结施 03 | 负一层墙、柱配筋平面图 | A1+ | |
| 结施 04 | 一层柱配筋平面图 | A1 | |
| 结施 05 | 二层柱配筋平面图 | A1 | |
| 结施 06 | 三层柱配筋平面图 | A1 | |
| 结施 07 | 四层柱配筋平面图 | A1 | |
| 结施 08 | 一层梁配筋平面图1 | A1 | |
| 结施 09 | 一层梁配筋平面图2 | A1 | |
| 结施 10 | 一层结构布置平面图 | A1 | |
| 结施 11 | 二层梁配筋平面图1 | A1 | |
| 结施 12 | 二层梁配筋平面图2 | A1 | |
| 结施 13 | 二层结构布置平面图 | A1 | |
| 结施 14 | 三层梁配筋平面图1 | A1 | |
| 结施 15 | 三层梁配筋平面图2 | A1 | |
| 结施 16 | 三层结构布置平面图 | A1 | |
| 结施 17 | 四层梁配筋平面图1 | A1 | |
| 结施 18 | 四层梁配筋平面图2 | A1 | |

备注：详图比例以图纸所写为准

工程负责 朱 君 工种负责 高 欣

校对 罗孝敏 制表人 高 欣 完成日期 2025 年12月

# 杭州园林设计院股份有限公司

## 图 纸 目 录

| | | | |
|---|---|---|---|
| 建设单位 | 江苏茂源电气有限公司 | 工程编号 | 25-14 |
| 工程名称 | 云创中心生产综合楼 | 图纸编号 | 结施 |
| 子项名称 | 生产综合楼 | 目录页码 | 共2页 第2页 |

| 图别图号 | 图名 | | 备注 |
|---|---|---|---|
| 结施 19 | 四层结构布置平面图 | A1 | |
| 结施 20 | 屋面梁配筋平面图1 | A1 | |
| 结施 21 | 屋面梁配筋平面图2 | A1 | |
| 结施 22 | 屋面结构布置平面图 | A1 | |
| 结施 23 | 1#楼梯结构 | A1 | |
| 结施 24 | 2#楼梯结构 | A1 | |
| | | | |
| | | | |
备注：详图比例以图纸所写为准

工程负责 朱 君 工种负责 高 欣

校对 罗孝敏 制表人 高 欣 完成日期 2025 年12月

# 结构设计总说明

## 一、工程概况：

1、本工程建造于江苏省东台市，其概况如下：

本工程为多个多层建筑单体，地上一～四层，地下一层。

2、本工程结构设计的性质和等级：

| 结构性质 | 结构体系 | 结构设计 | | | 基础设计 | | |
|---|---|---|---|---|---|---|---|
| | | 使用年限 | 安全等级 | 耐久等级 | 类别 | 设计等级 | 安全等级 |
| 多层建筑 | 钢筋混凝土框架结构 | 50年 | 二级 | 一级 | 桩基础 | 乙级 | 二级 |

3、本工程抗震设计的类别和等级：

| 建筑抗震设防类别 | 抗震设防烈度 | 场地土类型 | 设计地震分组 | 场地类别 | 特征周期Tg(S) | 抗震等级 |
|---|---|---|---|---|---|---|
| | | | | | | 框架柱、梁、墙 |
| 丙类 | 7度 | 0.10g | 第二组 | IV类 | 0.75S | 三级（除注明） |

4、本工程设计主要依据：

1）国家有关规范规程及行业标准：

1）建筑结构可靠性设计统一标准(GB50068－2018)；
2）建筑结构荷载规范（GB 50009－2012）；
3）混凝土结构设计规范（GB 50010－2010)(2015版)；
4）建筑抗震设防分类标准(GB50223－2008)；
5）建筑抗震设计规范 （GB 50011－2010)(2016版)；
6）建筑地基基础设计规范（GB 50007－2011）；
7）建筑桩基技术规范(JGJ94－2008)；
8）砌体结构设计规范(GB50003－2011)；
9）《中国地震动参数区划图》(GB 18306－2015)；
10）建筑边坡工程技术规范(GB50330－2002)；
11）混凝土结构耐久性设计标准(GB/T50476－2019)；

注：其他未列项目见国家及当地现行标准、规范及规程

2）本工程已批准的初步设计文件；

3）江苏科泰岩土工程有限公司提供的《江苏茂源电气有限公司生产综合楼岩土工程勘察报告》（详细勘察），工程编号：DT2025008

4）甲方提供的有关工艺设计资料。

5、本工程主要使用荷载（标准值，kN/m??）：

| 雪载（办公、餐厅等） | 雪载（厨房，多功能厅） | 上人屋面（露台） | 不上人屋面 | 阳台、走廊 |
|---|---|---|---|---|
| 2.5 | 4.0 | 2.5 | 0.5 | 2.5 |
| 楼梯间 | 设备间 | 地面附加荷载 | 基本风压 | 基本雪压 |
| 3.5 | 7.0 | B类 | 0.40 | 0.30 |

注：1）在使用过程中，未经结构复核认许另行增加，不得随意增加荷载及加砌任何墙体，不得改变结构的用途和使用环境。

2）施工荷载：一般楼、屋面应≤上述使用荷载且宜≤2.0kN/m??，同时在砼强度未达到100%前，商品≤砼相应强度时的允许荷载，支撑也不宜过早拆除。

3）设计屋面板、檐口、钢结构檩、雨篷施工或检修集中荷载应≤1.0KN，楼梯、看台、阳台和上人屋面等的栏杆顶部水平荷载≤1.0KN/m。

6、本工程结构整体计算采用北京盈建科软件股份有限公司编制的盈建科建筑结构计算软件YJK－A（版本号为YJK－A[1.9.3]）；基础计算采用上述软件系统中的YJK－F（版本号为YJK－F[1.9.3]；

7、标高：本工程的室内设计标高±0.000相当于绝对高程见总平体。

8、本工程图纸中尺寸未注明者为以毫米（mm）为单位，标高以米（m）为单位。

9、施工图应经有关审图机构审查，获通过并经过施工图会审（或技术交底）后，方可施工。

## 二、材料：

1、混凝土：除注明者外，结构各部分的现浇混凝土强度等级采用如下：

| 结构部位或层次 | 墙、柱 | 梁、板 | 备注 |
|---|---|---|---|
| 基础垫层 | C20 | | |
| 基础及上部 | C30 | C30 | 地下室外墙、盥洗及有抗渗防水要求P6抗渗等级 |
| 构造柱、圈梁、过梁 | C25 | | |

注：所用混凝土为商品混凝土，应采取可靠措施防止混凝土收缩裂缝。

2、砂浆性能对人等级为二级，实际达到的耐久极限根据标h，第1.5h，柱2.5h

3、钢筋采用：HPB300钢(?,fy=270N/mm??)、HRB400钢(?,fy=360N/mm??)，

钢筋的强度标准值应具有不小于95%的保证率。抗震等级为一、二、三级的框架和斜撑构件（含楼梯），

其纵向受力钢筋采用普通钢筋时，钢筋的抗拉强度实测值与屈服强度实测值的比值不应小于1.25；

钢筋的屈服强度实测值与强度标准值的比值不应大于1.3；且钢筋在最大拉力下的总伸长率实测值不应小于9%。

在施工中，当需要以强度等级较高的钢筋替代原设计中的纵向受力钢筋时，应按照钢筋受拉承载力设计值相等的原则换算，并应满足最小配筋率要求。

4、钢筋的焊接应符合《钢筋焊接及验收规程》(JGJ18－2012)。

5、型件：型件采用Q235B；吊钩、吊环采用HPB300钢筋，不得采用冷加工钢筋，所有外露铁件均要求刷红丹两度、调合漆一道。

6、填充墙砌块种类采用砖（砌块容重单位为kN/m ）：

| 砌体部位 | 砌 块 名 称 | 砌块强度等级 | 砂浆类型 | 砂浆强度等级 | 砌块允许容重限值 |
|---|---|---|---|---|---|
| ±0.000以下 | 砼实心砖 | MU20 | 水泥砂浆 | M10 | 18.0 |
| ±0.000以上 | 加气砼砌块 | A5 | 专用砂浆 | M5 | 容度等级B07 |

注：煤采用预拌砂浆，要求详见《预拌砂浆》(GB/T 25181－2010)。

7、耐久性要求：

1）本工程构件耐久性的环境类别详下表 ；

| 构件部位 | 与具有腐蚀性的地下水直接接触的构件 | 其余构件 |
|---|---|---|
| 环境类别 | 五 | － |

2）在一、二类环境中，设计使用年限为50年的结构混凝土耐久性的基本要求详下表；

| 环境类别 | | 最大水灰比 | 最低混凝土强度等级 | 最大氯离子含量（%） | 最大碱含量（kg/m?3） |
|---|---|---|---|---|---|
| 一 | | 0.60 | C20 | 0.3 | 不限制 |
| 二 | a | 0.55 | C25 | 0.2 | 3.0 |
| | b | 0.50(0.55) | C30(C25) | 0.15 | 3.0 |

注：（1）氯离子含量系指其占胶凝材料总量的百分比；

（2）预应力构件混凝土中的最大氯离子含量为0.06％；

最低混凝土强度等级宜按表中规定提高两个等级；

（3）素混凝土构件的水胶比及最低强度等级的要求可适当放松；

（4）当有可靠工程经验时，二类环境中的最低混凝土强度等级可降低一个等级；

（5）处于严寒和寒冷地区二b，三a环境中的砼应使用引气剂，并可采用括号中的数字；

（6）当使用非碱活性骨料时，对混凝土中的碱含量可不作限制。

3）在一、二类环境中，混凝土结构在设计还用年限内商应遵守下列规定：

（1）建立定期检测、维修制度；

（2）设计中可更换混凝土构件应按规定更换；

（3）构件表面的防护层，应按规定维护和更换；

（4）结构出现可见的耐久性缺陷时，应及时进行处理。

3）在五类环境中，设计使用年限为50年的结构混凝土耐久性的基本要求：

A．最小水泥用量300Kg/m，最大水灰比0.50，最大氯离子含量0.10.

B．保护层厚度：0.000以下梁、柱35mm，基础50mm．

C．与土壤接触面，柱素面防护：防锈油漆二层，厚度100um；

D．基础表面防护：垫层采用C20素混凝土，厚度100mm；基础面和外底子础2遍，沥青胶泥涂层厚度300um．

E．混凝土外露的预埋件应采用防腐油漆层防护，固化后涂层厚度300um．

## 三、地基基础与地下室：

1、本工程基础设计参江苏科泰岩土工程有限公司提供的《江苏茂源电气有限公司生产综合楼岩土工程勘察报告》

基础采用桩基础，桩基应通过现场静载荷试验确定单桩承载力，具体要求详见单体桩基及基础说明

基坑土方开挖应严格按设计要求进行，不得超挖。基坑周边堆载不得超过设计规定。土方开挖完成后应立即施工垫层，对基坑进行封闭，防止水浸和暴露，并应及时进行地下结构施工。

对于地下室基坑，开挖前需根据开挖深度，地质情况，场地周边情况等确定开挖方案，确保基坑边坡稳定及周边建筑物安全。

本工程地下室抗浮设计水位－0.500(3.700)。施工期间，应采取适当的降水措施，地下水位不得高于－3.500(相对标高)，待主体结构及覆土完成后才可以停止降水。

地下室外墙与基坑侧壁间隙回填土前，应清除积水，清除虚土和建筑垃圾，填土应采用级配砂石或其它材料（报设计同意）分层夯实，其压实系数>0.94。

2、基槽（坑）开挖到底后，应进行基槽（坑）检验。当发现地质条件与勘察报告和设计文件不一致，或遇到异常情况时，应结合地质条件提出处理意见。

3、基坑开挖应根据设计要求进行监测，实施动态设计和信息化施工。

4、本工程场地内地基的液化等级：无。

5、基底采用100厚C20素混凝土垫层，各结构出基础边100。

6、墙、柱纵筋在基础中的锚固和构造要求参国标图集16G101－3。

## 四、钢筋混凝土结构的一般规定：

1、纵向受拉钢筋的最小锚固长度(Lae)按图集(16G101－1)采用，聚锚固长度不足时，另加附加锚固措施，详见16G101－1 P57。

2、钢筋的最小搭接长度如下：

1）、钢筋绑扎搭接长度图集(16G101－1)采用

注：a）不同直径的钢筋搭接时，就?LE?就_?aE?值按较小的直径计算。

b）非抗震结构的钢筋锚固或搭接长度取值同四级抗震结构。

对普通楼层梁，如未注明，当钢筋直径≤22时，可采用绑扎搭接，但须以优先采用机械连接和等强对接焊。

受拉钢筋的直径>22mm及受压钢筋的直径>25mm不应采用绑扎搭接接头。

2）、钢筋接头位置及接头数量：

a）接头位置宜设置在受力较小处，宜避开梁端柱端，在同一根钢筋上应尽量少设接头。

b）受力钢筋接头的位置应相互错开，当采用绑扎的搭接接头时，搭接接头连接区段的长度为1.3倍搭接长度当采用焊接接头和机械接头时其连接区段长度为35d(d为纵向受力钢筋的较大直径)且不小于500。位于同一连接区段内的受拉钢筋搭接接头的面积百分率应符合下表。

| 连接区段内受力钢筋接头面积的搭布百分率(%) | | |
|---|---|---|
| 接头形式 | 受拉区 | 受压区 |
| 板、梁、(柱)绑扎搭接接头 | ≤25(50) | ≤50 |
| 焊接接头或机械搭压接头 | <50 | 不限 |

3、梁、柱箍筋及拉筋的弯钩构造要求及箍筋形式见图4－1。

4、在绑扎骨架中的钢筋搭接接头长度范围内，箍筋间距≤100，且≤5d(d为受力钢筋直径)。

5、受力钢筋的砼保护层厚度不应小于钢筋的公称直径，最外层钢筋保护层厚度应符合下表要求。

| 环境类别 | 板、墙 | 梁、柱 |
|---|---|---|
| 室内正常环境及无侵蚀性静水浸没环境等一类环境 | 15 | 20 |
| 室内潮湿、非严寒和非寒冷地区露天环境等二a类环境 | 20 | 25 |

混凝土强度等级不大于C25时，表中保护层厚度数值应增加5mm．

注：a）基础中纵向受力钢筋的保护层厚度不应小于40mm；当无垫层时不应小于70mm．

b）当水面部分保护层厚度大于50mm时应对保护层采取有效的防裂构造措施。

c）地下工程迎水面钢筋的保护层厚度不应小于50mm．

d）对有防火要求的建筑物，其保护层厚度应符合国家有关标准的要求。

e）对于其它环境类别的混凝土保护层，除另行说明外，应按现行国家规范和规定执行。

6、梁、柱钢筋接头应优先采用机械连接或等强对接焊，施工时应符合有关规范规定。

7、当柱（墙）砼强度等级高于梁板不超过一级(5MPa)时，节点核心区可按梁板的砼强度等级同时浇筑。

当柱（墙）砼强度等级高于梁板超过一级时，可先柱后梁浇筑，浇时结合斜面应做成毛面（图4－2）。

8、本工程钢筋砼结构部位的表示方法和构造要求，均采用国标(16G101－1)《混凝土结构施工图平面整体表示方法制图规则和构造详图》及其修正备注： 凡本说明及施工图中未明确的要求或构造等，可参见此国标图集，并满足其中有关的规定和构造要求。

9、钢筋混凝土构造柱的施工，应先砌墙后浇构造柱。

10、冬季施工时应采取防冻措施。

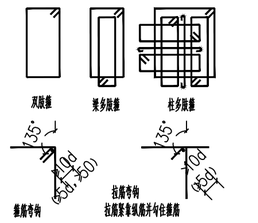



图4－1 箍筋、拉筋的弯钩及箍筋形式

拉号内值用于非框架梁，基础梁等

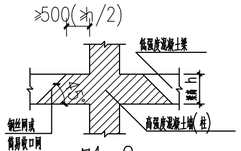



图4－2

当梁、墙（柱）混凝土等级不同时，应先墙（柱）后梁浇筑，应注续说清，不得添加施工缝。

备注栏

设计单位

杭州园林设计院股份有限公司
HANGZHOU LANDSCAPE ARCHITECTURE DESIGN INSTITUTE CO.,LTD
建筑、风景园林甲级：A133013139
规划乙级：城规编（142056）
市政乙级：A233013136
文物保护工程勘察设计乙级：0102SJ0002
公司地址：杭州市西湖区双龙街138号西城时代中心2号楼南楼
电话：0571-87021011 传真：0571-87021092 网址：www.hzyly.com

建设单位：江苏茂源电气有限公司

工程总称：云创中心生产综合楼

子项名称：

图纸名称：结构设计总说明一

| | 姓 名 | 签 名 |
|---|---|---|
| 审 定 | 张永龙 | |
| 审 核 | 郑 文 | |
| 项目负责人 | 朱 君 | |
| 专业负责人 | 高 欣 | |
| 设 计 | 高 欣 | |
| 制 图 | 高 欣 | |
| 校 对 | 罗孝敏 | |

执业专用章

按规定加盖

出图章

未盖出图专用章无效

| 工号 | 25-14 | 图别 | 结施 |
|---|---|---|---|
| 图号 | T1 | 修改版次 | |
| 日期 | 2025.12 | | |

五、板：

1、在梁、屋面板中，板面筋一般可在跨中搭接，端部板面筋进入支座的长度不小于La；板底筋应伸至支座中心线，且≥5d。板面通长筋需搭接时可在跨中错开搭接，对屋面板的板面通长筋，搭接长度应≥36d，且≥300，错开距离宜≥500。

2、板内双向配筋除注明外，均将短向钢筋（或按构造）放在外层，当板底与梁底平时，板的下部钢筋伸入梁内保弯折后置于梁的下部纵向钢筋之上。

3、板上开洞应尽量预留，当其边长≤300时，板中钢筋可绕过孔洞；当洞边长在300～500时，按（图5－1）板底加筋处理，洞口每侧加筋截面积不少于被切断钢筋之半，且补强钢筋≥2?12；当为圆孔时，应在洞边上下各另加?10；洞口加强筋尽可能贴伸到附近支座上。

4、当有管道开时，其板内钢筋位应按图设置，并按板上开洞规定处理，待管道设备安装完毕后，再用经返层浇筑，混凝土强度等级同各楼层，板厚度见各平面图标注。

5、板上有隔墙而板下无梁时，需在板底另加钢筋4?14(240左右押隔墙)或4?12(120左右押隔墙)，并锚入支座（梁、柱等）。

6、现浇挑檐、雨篷等外露构件的伸缩缝间距应≤12m，缝宽20，缝做宜用油膏或其他防水嵌措施处理。

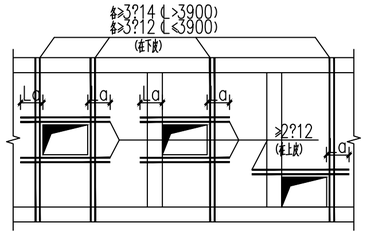



图5－1　板上开洞（洞长边为300～500）

六、梁：

1、梁的设计和构造要求见有关施工图及国标设计图集(16G101－1第54～68页)。

框架梁梁端箍筋加密区长度和加密区箍筋的最大间距及最小肢距：

| 抗震等级 | 箍筋加密区长度 | 箍筋最大间距 | 箍筋最大肢距 |
|---|---|---|---|
| 一 | 2h,500 | h/4,6d,100 | ≤Nmax(200;20d) |
| 二 | 1.5h,500 | h/4,8d,100 | ≤Nmax(200;20d) |
| 三 | 1.5h,500 | h/4,8d,150 | ≤Nmax(250;20d) |
| 四 | 1.5h,500 | h/4,8d,150 | ≤300 |
| 注 | 取较小值,h为梁截面高 | 取较小值,d为梁箍筋直径 | 取较小值,d为梁箍筋直径<br>无满足时可另加单肢箍 |

当施工图中对此未注明或未满足时，应按此要求加密箍筋间距或肢距。

2、梁纵筋的搭接（是绕梁外）：

1)、梁面筋可在离支座处1／3跨长处或跨中附近搭接；对框架梁，当贯通筋的直径d>22时，应采用机械连接或等强对接焊。

梁底筋一般在支座处锚固搭接。

2)、梁上部纵筋水平净距应≥30，且≥1.5d(d为纵筋最大直径)；　梁下部纵筋水平净距应≥25，且≥d；当梁下部纵筋多于二层时，则二层以上纵筋的水平中距应比下面二层的中距增大一倍。

3)、相交梁弯高时梁纵筋应使其相跨向放在下层，长跨向放在上层。

3、当主次梁相交而在主梁上未注明吊筋和加箍筋，应在主梁上设置加密箍每侧不少于3个。当两相似梁相交（倒T字形升格梁）而未注明加箍筋，应同时在二梁上设置加密箍每侧不少于3个，间距50(见图6－1)。

4、当施工图中仅画出梁断面而未注明梁端筋的处理时，则关上、下钢筋均应按图交锚入支座。

5、梁竖向及水平转折处的钢筋构造见图集(16G101－1)第91页，竖向折梁钢筋构造(一)，S=2h，箍筋加密为@100。

6、底、面纵筋注写两种直径时，除通长筋外其最大直径纵筋应置于第一排。

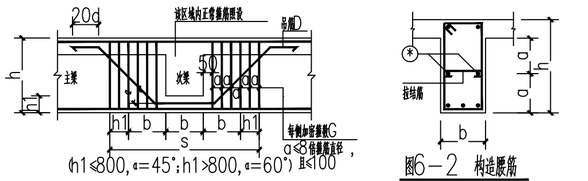



图6－1　相交梁处加密箍及吊筋

加密箍直径及肢数同该梁正弯矩箍




图6－2　构造腰筋

a≤200,è* ≥0.2%bhw且≥2?12

拉结筋的直径同箍筋，间距为非加密区箍筋间距的两倍

七、柱：

1、框架柱钢筋及截面尺寸变化时的构造要求见(16G101－1)。

2、框架柱纵向钢筋构造应满足下列要求：

1)、纵向钢筋总数为4根时，可在同一截面搭接；多于4根时，同一截面钢筋的接头数不宜多于总根数的50%。

2)、纵向钢筋的连接，下列情况下采用机械连接或等强对接焊：

a)、一、二级抗震等级在柱全长范围内；

b)、三级抗震等级底层柱；

c)、三、四级抗震等级柱纵筋直径d>22时。

3、框架柱箍筋加密区的箍筋最大间距及最小肢距：

| 抗震等级 | 箍筋最大间距 | 箍筋最大肢距 |
|---|---|---|
| 一 | 6d,100 | ≤200 |
| 二 | 8d,100 | ≤Nmax(250;20d) |
| 三 | 8d,150(柱根100) | ≤Nmax(250;20d) |
| 四 | 8d,150(柱根100) | ≤300 |
| 注 | 取较小值,d为柱纵筋最小直径 | d为柱箍筋直径时较大值至少伸至主筋隔一有箍筋及拉筋约束 |

当施工图中对此未注明或未满足时，应按此要求加密箍筋间距或肢距。

4、框架柱的其它构造要求，见国标设计图(16G101－1)。

八、填充墙及内隔墙：

1、砂砌块填充墙砌筑时砌块龄期至少28天，砌筑时应按照(JGJ/T14－2011)(12G614－1)相关工法执行。

楼梯间和人流通道的填充墙，两点采用钢丝网沙浆面层加强。

2、填充墙及内隔墙的砌筑，均应满足砌体结构的有关施工规定，当墙长不大于5m时墙顶与框架梁应采用可靠连接(图9－3)，且宜间距不大于4米的构造柱(图9－2)；墙端部无钢筋混凝土墙柱时，加设构造柱(图9－7)；>2.1m门窗洞口或不>2.1m但门窗洞口高度大于3M两侧无钢筋混凝土柱时，应加设构造柱(图9－8)。

3、对于240(120)左右厚的砌体，当砌体墙净高大于4m(3m)时，应在砌体墙高的中部或门洞顶部设置一道与砼柱或抗压砌体墙全长贯通的水平系梁(见图9－4)，系梁钢筋应锚入柱内200。

4、填充墙应沿砼柱和剪力墙设置墙身拉结筋2?6@500(或砌体皮数的倍数)，伸入砌体墙内的长度应全长拉通。

所有砌体墙在相互连接处及转角处，均应设置上述拉结筋。

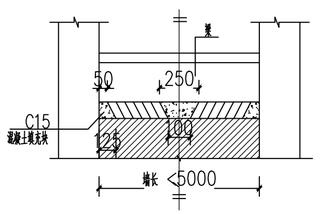



图9－1　填充墙顶与现浇梁连接

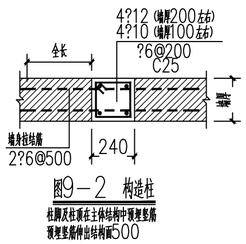



图9－2　构造柱


柱脚及柱顶在主体结构中预埋竖筋

预埋竖筋伸出结构面500

5、厕所卫生间四周墙下，先用C20素砼浇筑200高与墙身等厚的止水带，拔后再砌墙。

6、设置门、窗洞过梁时，其尺寸和配筋见下图，当门窗洞边与砼墙时，应在相应洞顶位置的砼墙上预留钢筋，以便钢筋焊接。住宅部分的窗台部位设高度为60，宽度同墙体的钢筋混凝土带，纵向钢筋不少于2?6.分布筋?4@200.施工图大样中有详细做法的按大样执行。

| Lo | ≤1200 | ≤1500 | ≤1800 | ≤2400 | ≤3000 | ≤3600 | ≤4000 |
|---|---|---|---|---|---|---|---|
| h | 120 | 150 | 180 | 180 | 240 | 300 | 350 |
| è1 | 2?8 | 2?10 | 2?10 | 2?10 | 2?10 | 2?12 | 2?12 |
| è2 | 2?12<br>(2?10) | 3?12<br>(2?12) | 3?12<br>(2?12) | 3?14<br>(2?14) | 3?14<br>(2?14) | 3?16<br>(2?16) | 3?16<br>(2?16) |

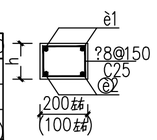


门窗过梁(GL)表　（梁长=洞净宽_o+500；当号内值用于100左右厚墙上的过梁）当不便设门窗过梁时，可参照图9－5施工。

7、当用钢筋砼作屋面女儿墙时，当≤12m设置一道伸缩缝，缝宽20，缝做宜用油膏等措施处理。

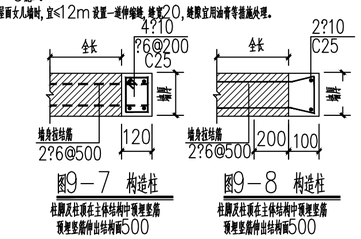



图9－7　构造柱

柱脚及柱顶在主体结构中预埋竖筋

预埋竖筋伸出结构面500

图9－8　构造柱

柱脚及柱顶在主体结构中预埋竖筋

预埋竖筋伸出结构面500

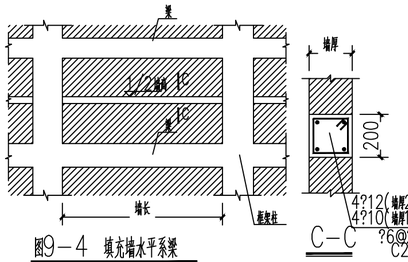



图9－4　填充墙水平系梁

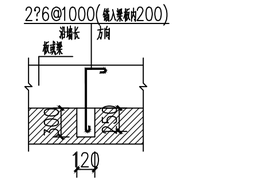



图9－3　墙顶拉结筋

九、沉降观察

1、沉降观察点设在建筑物的角点、中点及沿周边每隔12m左右处。

沉降观测点大样见图10－1；沉降观测　在施工期间每施工完一层测读一次；　主体结构封顶后每隔2个月一次；竣工后，第一年每一年度一次，以后每6个月一次，直至沉降稳定(　连续二次半年沉降量不超过2mm)为止。

如发现有大于0.2%　的不均匀沉降应立即通知设计人员，主体及竣工验收时须向我院提供完整详细的沉降观测记录。

十、其它：

1、结构施工时必须同建筑及设备工种密切配合与协调，对各工种所需求的预埋件、预留洞等，例墙体、电梯、楼梯、阳台栏杆等埋件及卫生间的预留洞等，均应按有关工种所提供的图纸预埋预留，软对五误并基实后，方可进行浇筑混凝土。钢结构部分设计施工需有相应资质的单位承担。

2、悬挑梁、板等结构上的支撑，必须在混凝土强度达到设计强度的100%时方可拆除。

3、悬挑梁、板在施工时，应采取措施(　例设置钢筋支撑等)，防止负筋下塌。

4、施工时对跨度>4m　的砼梁和所有悬挑梁、板，宜按跨度的大小取跨度的1　/1000～3/1000起拱。

5、屋面及雨篷等应设置必要的排水管(　孔)，施工完毕后必须清扫干净，保持排水畅通。

6、避雷接地做法见有关电施图。

7、施工期间不得提负荷等放置建筑材料和施工垃圾，特别注意楼板上集中负荷时对结构受力和支形的不利影响。

8、材料代用时应经过评细核算；对改变结构材料的代换，应经得设计单位同意。

9、本说明如与各施工图的要求不同时，应以各施工图为准。

10、未经技术鉴定或设计认可，不得任意改变结构主体，不得改用超过设计荷载的用途。

11、施工应遵守国家与工程所在地区现行的各有关工种的施工质量验收规范或标准。

12、所有涉及到图纸的修改一律以我院出具加盖出图专用章的设计修改通知或修改图纸为准。

13、施工图应经图审机构审查通过，并经过施工图会审(　或技术交底)后，方可施工。

十一、本工程套用图集：

1、《混凝土结构施工图平面整体表示方法制图规则和构造详图—　现浇混凝土框架、剪力墙、梁、板》(国标图集16G101－1)。

2、《混凝土结构施工图平面整体表示方法制图规则和构造详图—　现浇混凝土板式楼梯》(国标图集16G101－2)。

3、《混凝土结构施工图平面整体表示方法制图规则和构造详图—　独立基础、条形基础、筏形基础及桩基承台》(国标图集16G101－3)。

4、《框架结构填充小型空心砌块墙体结构构造》(国标图集12G614－1)。

5、《建筑物抗震构造详图》　(国标图集11G329－1)。

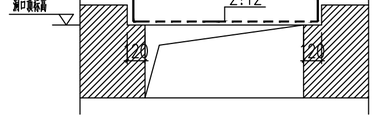



图9－5　门窗顶附加筋大样

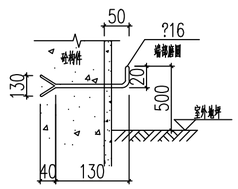



图10－1　沉降观测点

备注栏

设计单位

杭州园林设计院股份有限公司

HANGZHOU LANDSCAPE ARCHITECTURE DESIGN INSTITUTE CO.,LTD

建筑、风景园林甲级:A133013139

规划乙级:城规编(142056)

市政乙级:A233013136

文物保护工程勘察设计乙级:0102SJ0002


公司地址：杭州市拱墅区环城北路78号园林设计中心3号楼
电话：0571-87031011　　传真：0571-87031092　　网址：www.hzyly.com


建设单位　江苏茂源电气有限公司

| | |
|---|---|
| 工程总称 | 云创中心生产综合楼 |
| 子项名称 | |
| 图纸名称 | 结构设计总说明二 |

| | 姓　名 | 签　名 |
|---|---|---|
| 审　定 | 张永龙 | |
| 审　核 | 郑　文 | |
| 项目负责人 | 朱　君 | |
| 专业负责人 | 高　欣 | |
| 设　计 | 高　欣 | |
| 制　图 | 高　欣 | |
| 校　对 | 罗孝敏 | |

执业专用章

按规定加盖

出图章

未盖出图专用章无效

| | | | |
|---|---|---|---|
| 工号 | 25-14 | 图别 | 结施 |
| 图号 | T2 | 修改版次 | |
| 日期 | 2025.12 | | |

专业会签栏：结构　给排水　电气　暖通　园林　建筑

# 危险性较大分部分项工程说明（结构专篇）

一、总体要求：

1、依据住房和城乡建设部《危险性较大的分部分项工程安全管理规定》（住房城乡建设部令第37号）、中华人民共和国住房和城乡建设部办公厅《住房城乡建设部办公厅关于实施〈危险性较大的分部分项工程安全管理规定〉有关问题的通知》（建办质〔2018〕31号），本工程中涉及危大工程的重点部位和环节以及相应的保障工程周边环境安全和工程施工安全的意见详见下表“危险性较大的分部分项工程及相应意见”。

2、在工程的施工招标文件中应列出危大工程清单，要求施工单位在投标时补充完善危大工程清单并明确相应的安全管理措施。

3、施工单位应根据施工图设计图纸，并参考设计单位的提示，结合施工单位常用的施工方式，应当在危大工程施工前组织工程技术人员编制专项施工方案。对于超过一定规模危险性较大分部分项工程，详见住房和城乡建设部办公厅《住房城乡建设部办公厅关于实施〈危险性较大的分部分项工程安全管理规定〉有关问题的通知》（建办质〔2018〕31号）附件2所列工程范围的全部内容，施工单位应当组织召开专家论证会对专项施工方案进行论证。

4、根据设计单位的提示，施工单位应全面熟悉设计图纸，根据施工组织设计，对工程存在超过一定规模危险性较大分部分项工程，汇编列出所涉及的全部工程部位、节点清单，作为监理单位编制监理规划和实施细则、专家论证、安全措施备案、工程交底、质安监部门日常监督的重要依据。

二、危险性较大的分部分项工程及相应意见：

本项目中危险性较大的分部分项工程是依据中华人民共和国住房和城乡建设部办公厅《住房城乡建设部办公厅关于实施〈危险性较大的分部分项工程安全管理规定〉有关问题的通知》（建办质〔2018〕31号）、本项目的工程特点、周边环境、水文地质条件、设计文件和相关的规范规定所列，施工单位应根据施工图设计图纸，并参考设计单位的提示，并根据项目和本工程的实际情况，进一步的识别本项目中危险性较大的分部分项工程，并对所有的危险性较大的分部分项工程在施工前组织工程技术人员编制专项施工方案，对于超过一定规模危险性较大分部分项工程，施工单位应当组织召开专家论证会对专项施工方案进行论证。

危险性较大的分部分项工程及相应意见（表一）

| 危险性较大的<br>分部分项工程范围 | 对应部位与环节 | 保障工程施工安全的意见 | 保障工程周边环境安全的意见 |
|---|---|---|---|
| 基坑工程：（一）开挖深度超过3m（含3m）的基坑（槽）的土方开挖、支护、降水工程。 | 桩基和承台基础、筏板基础、<br>独立基础 | 1、施工前应进行设计交底，提示施工单位通读工程地质勘察报告及全套施工图、领会设计意图，并组织工程技术人员编制施工组织设计；<br>2、施工应认真按照设计图纸及施工规范执行；<br>3、工程参建各方应认真按照《危险性较大的分部分项工程安全管理规定》进行施工管理，施工单位应当在危大工程施工前组织工程技术人员编制专项施工方案，对于超过一定规模的危大工程，施工单位应当组织召开专家论证会对专项施工方案进行论证；<br>4、应对现场地形及现场管线进行核查，如与设计采用地形图、管线图有差异，应及时反馈业主；<br>5、施工期间，施工单位应在施工中注意将现场地质状况与地质详勘中的资料对比，如实现地质情况与设计采用地质资料不符，应及时反馈业主；<br>6、施工期间应加强稿定性监测、监控；对软大、软弱或地质情况复杂的基坑，商应建立边坡稿定信息化、动态化的监控系统，指导施工，如遇异常，应及时反馈业主；<br>7、施工程序应符合规范和各级质监、安监等部门要求；<br>8、施工中应采取切实可行的措施对风险进行控制，避免滤砌、机械伤害、起重伤害、高处坠落、物体打击、触电、火灾、坍塌、车船撞击、施工设备事故等风险事件发生；<br>9、针对不良地质（岩性及风化程度、物适带、地下水、高边坡、土洞、溶洞、液化土、软土、滑坡、泥石流等）、恶劣气候（暴风、暴雨、洪水、雷电等）、运输通行（撞击等）等危险源应有切实可行的施工技术措施和安全技术措施。 | 1、提示工程周边环境风险源（周边铁路、公路、城市道路、桥梁、建筑、管线、水体、文物、可燃物等）；<br>2、对涉及周边环境安全的风险源，施工单位应根据具体情况编制施工组织方案及专项保护方案（保护措施、监测监控、应急预案等），报有关部门审批确认；<br>3、施工中如遇异常情况，应及时反馈业主；<br>4、应查明基坑周边建（构）筑物、道路结构特征及地下管线情况。施工及拆除期间，应依据监测方案进行监测。<br>5、基坑施工应设置有效安全防护设施，防止安全事故发生；<br>6、放拔施工应采取合理的拔比，重型车辆的进出需要采取措施。基坑周边严禁超载，土方严禁超挖。施工期间有组织排水。<br>7、基坑支护结构及其施工机具不得影响地下管线、构筑物等。<br>8、施工期产生的弃土、各种建筑垃圾和生活垃圾，应制订合理的弃迹方案，并尽量避免在降雨期间开挖土石方，以防雨水冲刷造成水土流失、污染水体、堵塞排水管道。<br>9、土石方等易产生扬尘的物料运输，必须使用专用的密闭运输车，防止在运输过程中抛洒散落。设置车辆清洗设施及配备的泥沙井，车辆冲洗干净后方可驶出工地。 |
| 模板工程及支撑体系：<br>满足以下条件之一的工程为危险性较大的分部分项工程：<br>混凝土模板支撑工程：搭设高度5m及以上，或搭设跨度10m及以上，或施工总荷载（荷载效应基本组合的设计值，以下简称设计值）10kN/m^及以上，或集中线荷载（设计值）15kN/m及以上，或高度大于支撑水平投影宽度且相对独立无联系构件的混凝土模板支撑工程。<br>满足以下条件之一的工程为超过一定规模的危险性较大的分部分项工程：<br>混凝土模板支撑工程：搭设高度8m及以上，或搭设跨度18m及以上，或施工总荷载（设计值）15kN/m^及以上，或集中线荷载（设计值）20kN/m及以上。 | 楼盖模板搭设高度5m及以上； | 1、施工前应进行设计交底，提示施工单位通读工程地质勘察报告及全套施工图、领会设计意图，并组织工程技术人员编制施工组织设计；<br>2、模板支架的高宽比不宜大于 3；当高宽比大于3 时，应增设稿定性措施，并应进行支架的抗倾覆验算。<br>3、工程参建各方应认真按照《危险性较大的分部分项工程安全管理规定》进行施工管理，施工单位应当在危大工程施工前组织工程技术人员编制专项施工方案，对于超过一定规模的危大工程，施工单位应当组织召开专家论证会对专项施工方案进行论证；<br>4、应对现场地形、现场管线及周边构筑物进行核查，支撑体系应保证自身安全；<br>5、模板及支架均应进行施工图设计，经批准后方可用于施工；<br>6、支承于地基土上的模板支架，应按现行国家标准《建筑地基基础设计规范》GB50007 的有关规定对地基土进行验算；支承于混凝土结构构件上的模板支架，应按现行国家标准《混凝土结构设计规范》GB50010 的有关规定对混凝土结构构件进行验算。<br>7、模板及支撑体系材料应符合其国家或行业标准的规定，常备式定型钢构件应符合该产品相应的技术规定；<br>8、模板及支撑体系应具有足够的强度、刚度和稿定性，应能承受施工过程中所产生的各种荷载，应能抵抗在施工过程中可能发生的振动和偶然撞击。<br>9、混凝土强度必须达到规范要求，并经监理单位确认后方可拆除模板支架。模板支架拆除应从上而下逐层进行。<br>10、现浇模板拆除时混凝土应满足的强度要求。 | 1、安装和拆模应有专人指挥，并在下面标出作业区，暂停人员和车辆通过。<br>2、拆模时，应按顺序逐块拆除，避免整体塌落；拆除顶板时，应设临时支撑确保安全作业。<br>3、施工中如遇异常情况，应及时反馈业主；<br>4、模板工程及支撑体系应考虑对周边交通通行影响，不得侵入通行限界，且需征得交管或其权属部门批准后方可实施；<br>5、模板工程及支撑体系跨越需要维持正常通行（航）的道路（水域）时，对其现浇支架应采取防碰撞的安全措施，并应设置必要的交通导流标志，保证施工安全和交通安全。<br>6、支撑体系不得影响地上、地下管线、周边构筑物等。 |
| 起重吊装及起重机械安装拆卸工程：<br>（一）采用非常规起重设备、方法，且单件起吊重量在10kN及以上的起重吊装工程。采用非常规起重设备、方法，且单件起吊重量在100kN及以上的起重吊装工程为超过一定规模的危险性较大的分部分项工程。 | 采用非常规起重设备、方法，<br>且单件起吊（或一次起吊）<br>重量在10kN（100KN）<br>及以上的起重吊装工程。 | 1、工程参建各方应认真按照《危险性较大的分部分项工程安全管理规定》进行施工管理，施工单位应当在危大工程施工前组织工程技术人员编制专项施工方案，对于超过一定规模的危大工程，施工单位应当组织召开专家论证会对专项施工方案进行论证。<br>2、施工单位应了解被吊构件各项参数，选择适宜的起重设备。<br>3、应对现场地形、现场管线及周边构筑物进行核查，应保证起重吊装设备自身安全。<br>4、起重机械的安全装置、连接螺栓必须齐全有效，结构件不得开焊和开裂，连接件不得严重磨损和塑性变形，零部件不得达到报废标准。<br>5、起重机械应当按规定进行维修、维护和保养，设备管理人员应当按规定对机械设备进行检查，发现隐患及时整改。<br>6、遇大风、大雾、大雨、大雪等恶劣天气，不得使用起重机械。<br>7、两台以上塔式起重机在同一现场交叉作业时，应当制定塔式起重机防碰撞措施。任意两台塔式起重机之间的最小架设距离应符合规范要求。<br>8、起重设备及操作人员应符合国家及地方相关规范及法规要求；<br>9、施工单位应按《铁路工程基本作业施工安全技术规程》TB10301－2009第11节的规定，结合工程实际和项目特点，明确施工安全责任，制定施工安全措施，加强施工安全管理，有效预防事故发生。 | 1、识别起吊工程周边环境风险源（周边铁路、桥梁、建筑、管线、水体、文物、可燃物等）。<br>2、对涉及周边环境安全的风险源，施工单位应根据具体情况编制施工组织方案及专项保护方案（保护措施、监测监控、应急预案等），报有关部门审批确认。<br>3、起重吊装考虑对周边交通通行影响。<br>4、起重吊装承重点不得影响地下管线及构筑物等。<br>5、吊装作业时，严格控制吊车回转半径，避免触及周围建筑物或高压线。<br>6、起重吊装中应采取切实可行的措施对风险进行控制，避免机械伤害、高处坠落、物体打击、触电、坍塌、车船撞击、施工设备事故等风险事件发生。<br>7、起吊设备下方严禁站人、行车。<br>8、起重吊吊装时，起重机架设的位置不得影响沟槽边坡的稿定；起重机在架空高压输电线路附件作业时，与线路间的安全距离应符合电力管理部门的规定。<br>9、作业范围周边设置警示标志、警示带等防护隔离措施，并安排专人进行安全巡查。<br>10、施工中如遇异常情况，应及时反馈业主。 |
| （二）采用起重机械进行安装的工程。 | 采用起重机械进行安装的工程。 | | |


设计单位
杭州园林设计院股份有限公司
HANGZHOU LANDSCAPE ARCHITECTURE DESIGN INSTITUTE CO. LTD
建筑、风景园林甲级：A133013139
规划乙级：城规编（142056）
市政乙级：A232013136
文物保护工程勘察设计乙级：0102SJ0002
公司地址：杭州市西湖区双龙街136号西溪世纪中心2号楼南楼
电话：0571-87631011　传真：0571-87631092　网址：www.hzyly.com


建设单位：江苏茂源电气有限公司

| | |
|---|---|
| 工程总称 | 云创中心生产综合楼 |
| 子项名称 | |
| 图纸名称 | 危险性较大分部分项工程说明（结构专篇） |

| | 姓　名 | 签　名 |
|---|---|---|
| 审　定 | 张永龙 | |
| 审　核 | 郑　文 | |
| 项目负责人 | 朱　君 | |
| 专业负责人 | 高　欣 | |
| 设　计 | 高　欣 | |
| 制　图 | 高　欣 | |
| 校　对 | 罗孝敏 | |

执业专用章

按规定加盖

出图章

未盖出图专用章无效

| 工号 | 25-14 | 图别 | 结施 |
|---|---|---|---|
| 图号 | T3 | 修改版次 | |
| 日期 | 2025.12 | | |

专业会签栏：园林　建筑　结构　给排水　电气　暖通　弱电

# 江苏省民用建筑施工图绿色设计专篇（结构）

一、项目名称：云创中心综合楼　　子项：生产综合楼

二、项目概况：

| 所在城市 | 气候分区 | 建筑性质 | 建筑面积（㎡） | 建筑高度 | 建筑层数 | 结构设计使用年限 | 结构体系 | 基础形式 | 绿色星级目标 | 建筑类别 | 利用可再生能源种类 |
|---|---|---|---|---|---|---|---|---|---|---|---|
| 东台市 | ☑夏热冬冷<br>☐寒冷 | 办公 | 5074.12 | 22.20 | 地上：4层 | 50 | 钢筋砼框架结构 | 桩基 | 一星 | ☑甲类<br>☐乙类 | ☑太阳能光热 ☐地源热泵<br>☐太阳能光伏 ☐_____ |

三、设计依据

1.《江苏省绿色建筑设计标准》DGJ32/T173-2014

2.《绿色建筑评价标准》GB/T 50378-2014

3.《民用建筑绿色设计规范》JGJ/T229-2010

4.《江苏省民用建筑施工图绿色设计文件编制深度规定》

5. 国家、省、市现行的法律、法规、其它相关标准和规定

四、绿色设计基本要求

1.结构优化设计说明：

a.钢筋混凝土结构中混凝土和砂浆采用预制的方式。

b.本工程所有钢材均采用高强的HPB400级热轧带肋钢筋，降低了含钢量。

c.采用抗震性能较好的框架结构。

d.在进行建筑材料的选择时，尽可能选择本地区的材料，减少材料的运输距离，降低结构的成本。

2.基础优化设计说明：

a.本工程考虑基础上部结构共同作用进行协同设计；

b.计算沉降时，考虑承台，桩与土的协同作用。

3.混凝土结构部分材料选用：

1）混凝土结构或混合结构中受力普通钢筋不低于400MPa级的热轧带肋钢筋应用范围：基础，框架柱，框架梁，现浇板。

2）混凝土结构或混合结构中受力普通钢筋使用不低于400MPa级的热轧带肋钢筋占受力钢筋总量的的比例为　100%

3）混凝土竖向承重结构采用强度等级不小于C50凝土用量占竖向承重构件混凝土总量的比例为　0%

4.钢结构部分材料选用：

1）本项目中钢结构应用范围和钢结构型式：

2）钢结构构件或混合结构中钢结构部分的钢材等级为：Q235B

3）钢结构或混合结构中钢结构部分Q345上高强钢材用量占钢材总量的比例：0%

4）钢结构采用耐候结构钢:☐是　☑否

5）钢结构采用耐候型防腐涂料:☑是　☐否

5.本项目现浇混凝土应全部采用预拌混凝土，建筑砂浆应全部采用预拌砂浆。

6.可再循环、再利用材料选用：

建筑中的可再利用材料和可再循环材料用量比例为　10%

五、绿色设计一般要求

1.本项目选用的新型节能环保材料包括以下材料：轻质蒸压加气混凝土砌块。

2.本项目选用的高耐久性材料包括以下材料：混凝土。

3.本项目是否采用新型工业化建筑结构体系：☐是　☑否

4.本项目是否为改建、扩建工程：☐是　☑否

六、主要套用图集编号

《住宅太阳能热水系统选用级安装》 11CJ32.

专业会签栏：园林 建筑 结构 给排水 电气 暖通 弱电

设计单位

杭州园林设计院股份有限公司

HANGZHOU LANDSCAPE ARCHITECTURE DESIGN INSTITUTE CO.LTD

建筑、风景园林甲级:A133013139

规划乙级:城规编（142056）

市政乙级:A233013136

文物保护工程勘察设计乙级:0102SJ0002

公司地址：杭州市西湖区双龙街138号西溪世纪中心2号楼南楼

电话：0571-87631011　传真：0571-87631092　网址：www.hzyly.com

建设单位：江苏茂源电气有限公司

| | |
|---|---|
| 工程总称 | 云创中心生产综合楼 |
| 子项名称 | |
| 图纸名称 | 江苏省民用建筑施工图绿色设计专篇（结构 |

| | 姓　名 | 签　名 |
|---|---|---|
| 审　定 | 张永龙 | |
| 审　核 | 郑　文 | |
| 项目负责人 | 朱　君 | |
| 专业负责人 | 高　欣 | |
| 设　计 | 高　欣 | |
| 制　图 | 高　欣 | |
| 校　对 | 罗孝敏 | |


执业专用章


按规定加盖

出图章

未盖出图专用章无效

| | | | |
|---|---|---|---|
| 工号 | 25-14 | 图别 | 结施 |
| 图号 | T4 | 修改版次 | |
| 日期 | 2025.12 | | |

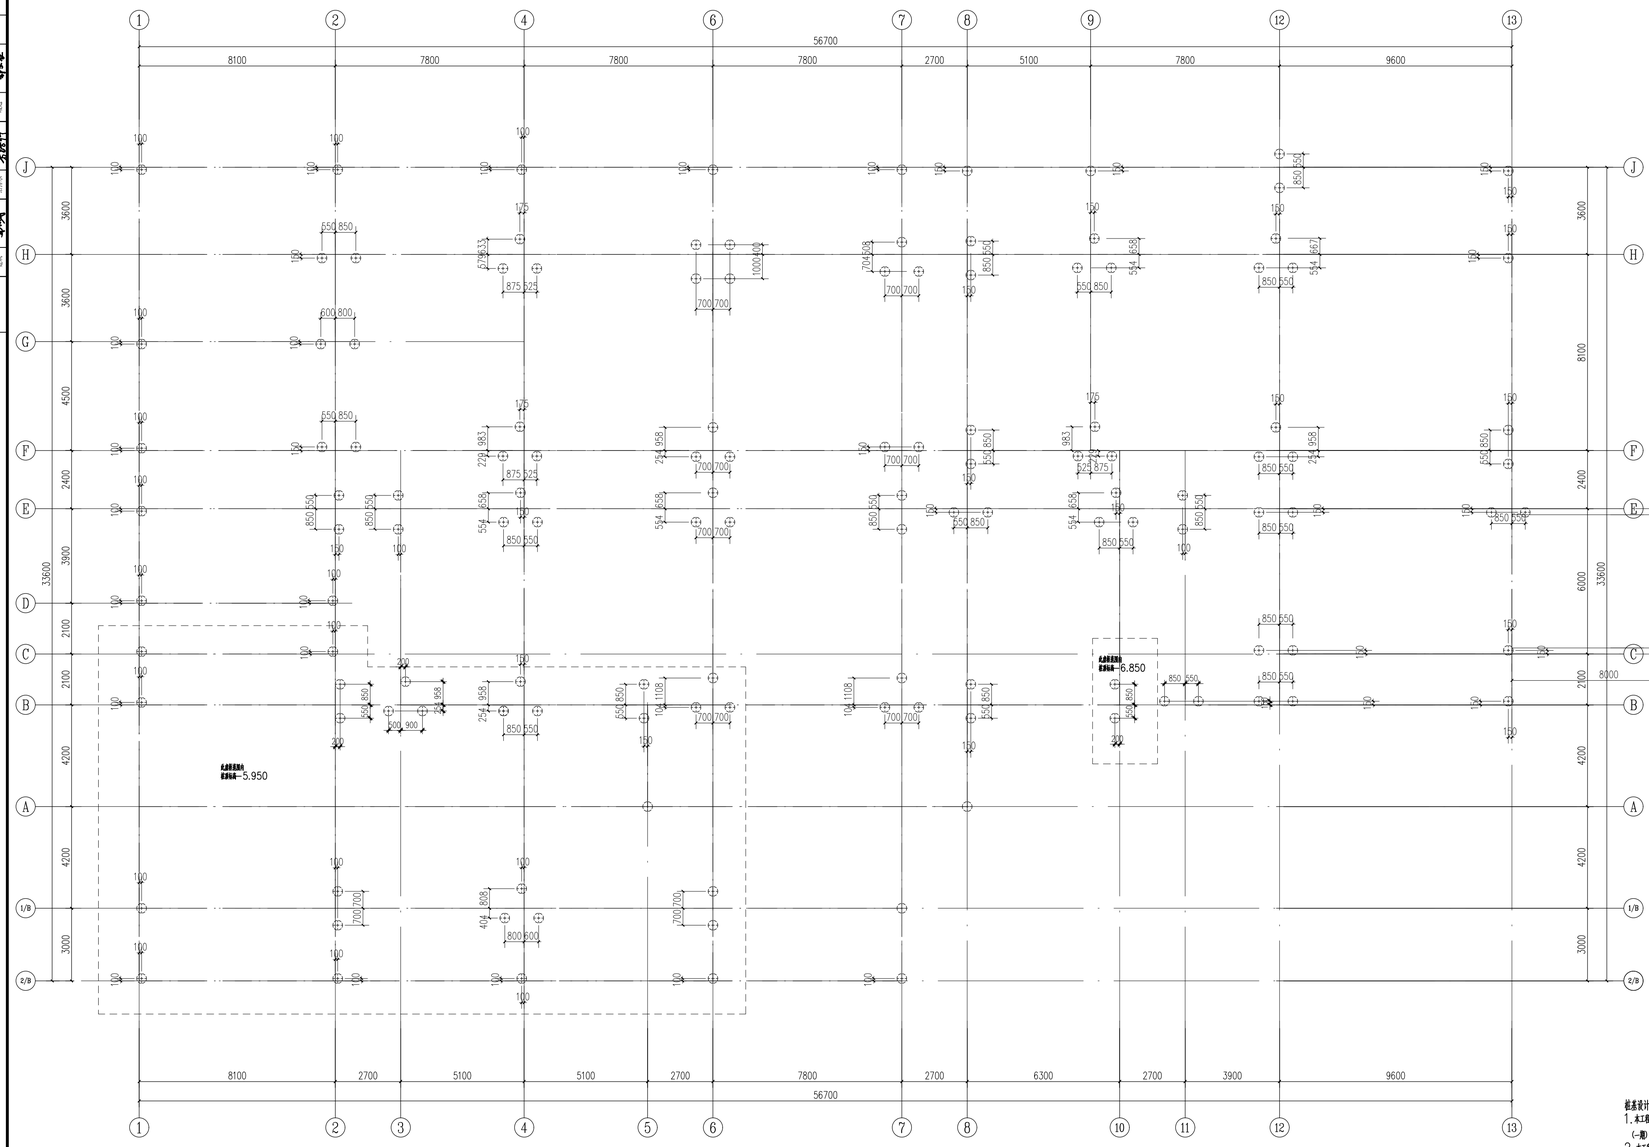

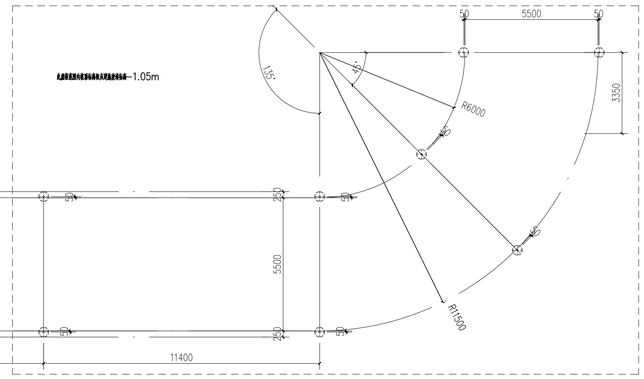
# 桩位布置平面图 1:100

1. 本种株土0.000=4.200
2. 本种体采用预应力混凝土管桩，以便①层粉砂为桩端持力层
   桩型（静过桥外）：PHC-400(100)AB-C80-9.8.8A(出：A型桩尖类型)。
3. 单桩承载力特征值=1100KN，桩顶标高（静过桥外）-5.450，桩入承台50mm。
4. 桩基施工宜打入桩，以可桩力控制为主，桩长控制为辅。
5. 参地勘报告3～6地质剖面图。
6. 其余未注明事项见桩基说明。

## 桩基设计说明

1. 本工程根据浙江苏科岩土工程有限公司提供的《江苏茂源电气有限公司乐清园区工程建筑工程岩土详细设计项目（一期）工程岩土工程勘察报告》，基础采用预应力混凝土管桩。
2. 本工程地基基础设计等级为乙级，桩基设计等级为乙级。
3. 未注明定位尺寸的桩基均居轴线中。
4. 钢制管桩桩身焊接、接桩，桩与承台连接（采用机压桩法（静压）与承台连接焊接，桩进H=3.5M）等要求参照江苏省标图集《预应力混凝土管桩》（苏G03-2012）
5. 工程桩施工前需进行静载荷试桩确定单桩竖向抗压极限承载力标准值（②倍特征值）是否满足设计要求。
6. 桩基检测要求：
   1）静载荷试验（单桩竖向抗压）：试桩数量应不少于桩总数的1%，且不少于3根（总桩数不超过50根2根）；
      静载荷试验验证单桩竖向抗压承载力加载值为2倍特征值。
   2）桩基完整性检测：本工程100%的桩基础采用低应变检测。
7. 施工时应特别注意桩基保护，并发现与地质报告特点差异较大时，应及时通知勘察和设计单位进行分析处理。
8. 本工程设计未详之处与现行国家现行施工验收规范执行。


设计单位
杭州园林设计院股份有限公司
HANGZHOU LANDSCAPE ARCHITECTURE DESIGN INSTITUTE CO.,LTD
建筑、风景园林甲级：A133013139
规划乙级：城规编（142056）
市政乙级：S133013139
文物保护工程勘察设计乙级：0102SJ0002
公司地址：杭州市西湖区有恩路138号西湖世纪中心2号楼6楼
电话：0571-85263012　传真：0571-85263102　网址：www.hzla.cn


| | |
|---|---|
| 建设单位 | 江苏茂源电气有限公司 |
| 工程总称 | 云创中心生产综合楼 |
| 子项名称 | 生产综合楼 |
| 图纸名称 | 桩位布置平面图 |

| | 姓名 | 签名 |
|---|---|---|
| 审定 | 张永龙 | |
| 审核 | 郑文 | |
| 项目负责人 | 朱君 | |
| 专业负责人 | 高欣 | |
| 设计 | 高欣 | |
| 制图 | 高欣 | |
| 校对 | 罗孝敏 | |


执业专用章


按规定加盖

出图章

未盖出图专用章无效

| | | | |
|---|---|---|---|
| 工号 | 23-14 | 图别 | 结施 |
| 图号 | 01 | 修改版次 | |
| 日期 | 2025.12 | | |

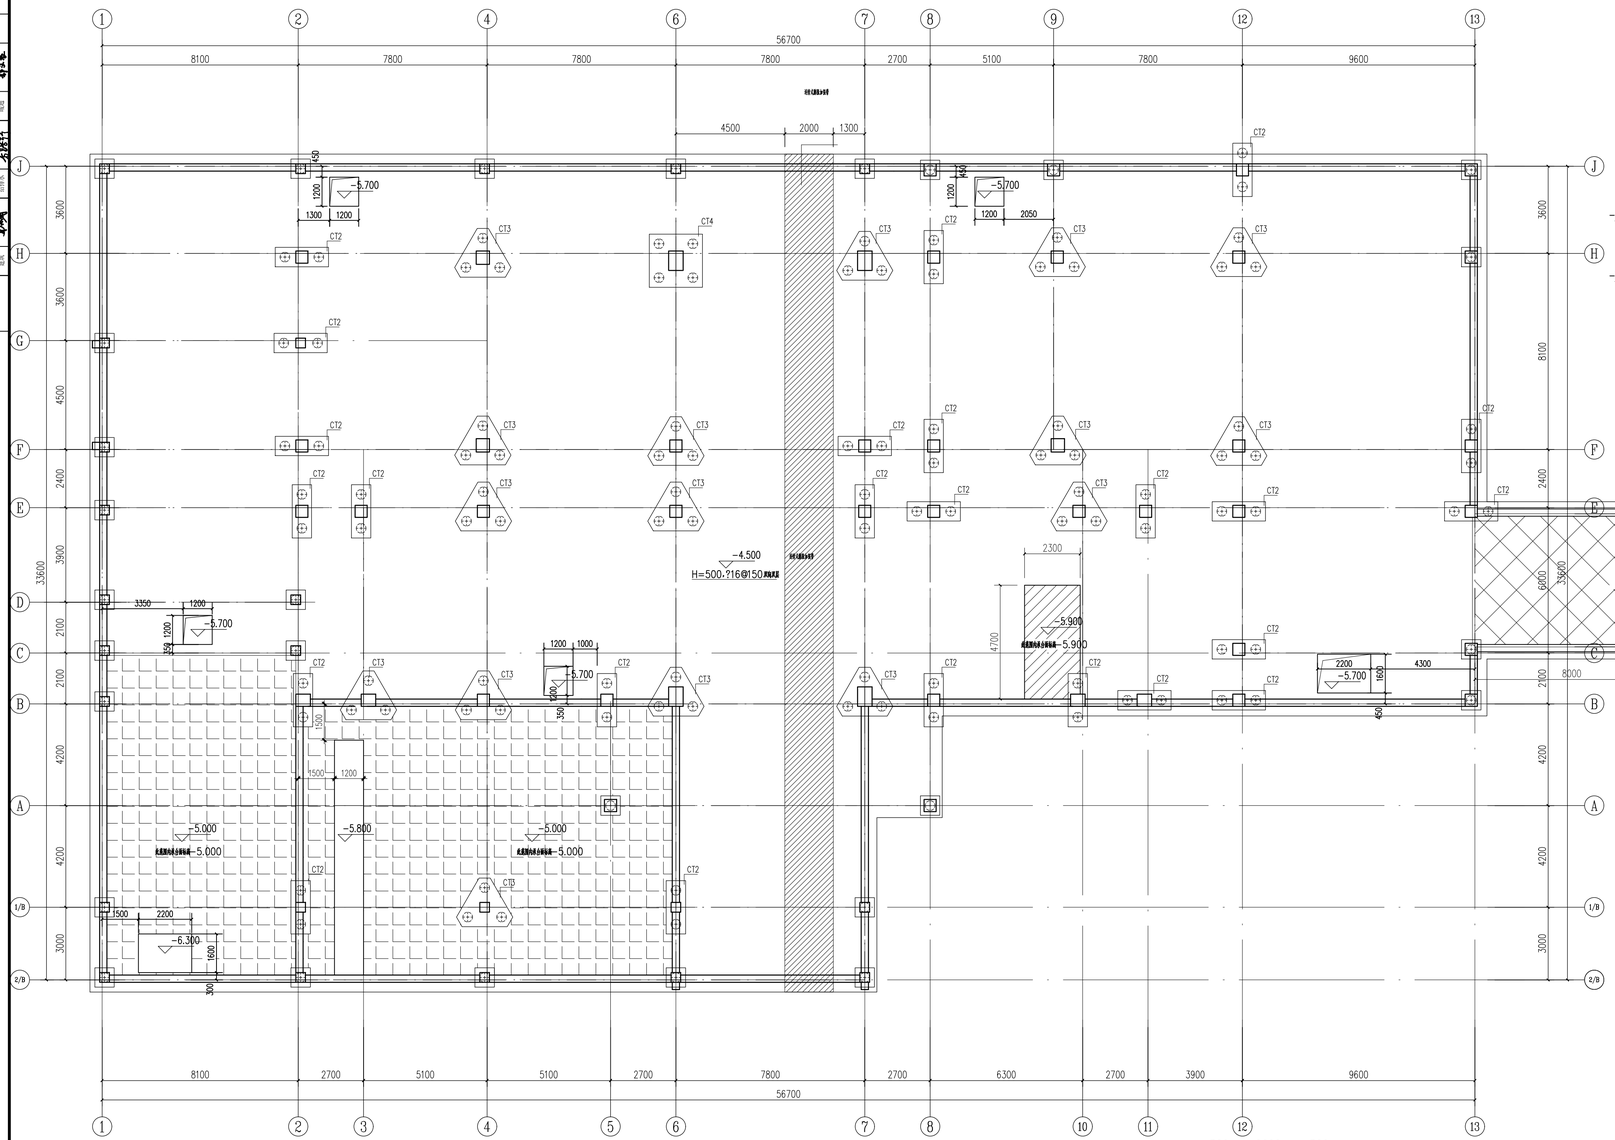


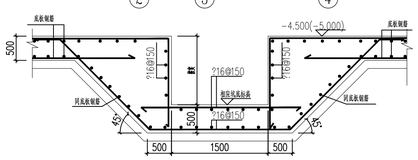

基坑构造

## 承台、底板结构平面图 1:100


1. 图中未注明门 桩承台号为CT1，未注明承台面标高—4.500。
2. 承台定位以轴位为基准，承台与桩相对关系见承台详图。
3. 图中未注明承厚与为500，未注明钢筋配?16@150,其构其层未注明底板承面标高—4.500；基下室底板设置辅助为500mm。
4. 集水井（坑）、电梯基坑构造见详图。
5. 本图纸标注相关钢筋构造详图参见国家现现标注实计图集(16G101-3)。
6. 底板承厚度长钢筋，在承台处不露筋，底部通长钢筋在承台处截断。
7. 底板面主筋筑面标高用C20非混凝土填充，留置集水坑位置。
8. 施工时配合水电图纸，点做对集水坑 电梯井 管水沟位置。

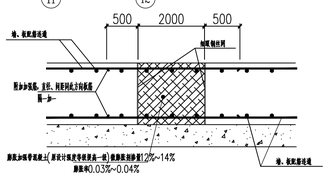


地下室连续式膨胀加强带

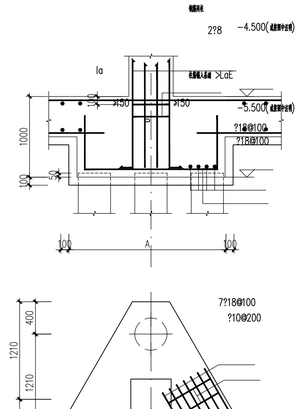


CT3

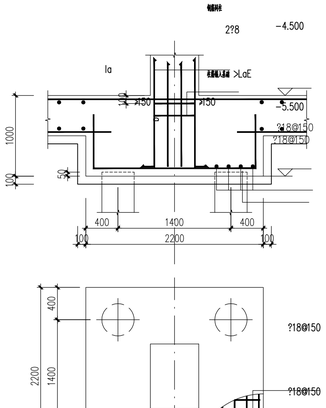


CT4

备注栏

设计单位
杭州园林设计院股份有限公司
HANGZHOU LANDSCAPE ARCHITECTURE DESIGN INSTITUTE CO.,LTD
建筑、风景园林甲级（A133031139
规划乙级（城规编（142056）
市政乙级（A233013136
文物保护工程勘察设计乙级（0102SJ00002
公司地址：杭州市西湖区求是路28号西湖世纪中心27楼电梯
电话：0571-87021011 传真：0571-87021002 网址：www.hzyly.com

| | |
|---|---|
| 建设单位 | 江苏茂源电气有限公司 |
| 工程名称 | 云创中心生产综合楼 |
| 子项名称 | 生产综合楼 |
| 图纸名称 | 承台、底板结构平面图 |

| | 姓 名 | 签 名 |
|---|---|---|
| 审 定 | 张永龙 | |
| 审 核 | 郑 文 | |
| 项目负责人 | 朱 君 | |
| 专业负责人 | 高 欣 | |
| 设 计 | 高 欣 | |
| 制 图 | 高 欣 | |
| 校 对 | 罗孝敏 | |


执业专用章


按规定加盖

出图章

未盖出图专用章无效


| | | | |
|---|---|---|---|
| 工号 | 25-14 | 图别 | 结施 |
| 图号 | 02 | 修改版次 | |
| 日期 | 2025.12 | | |

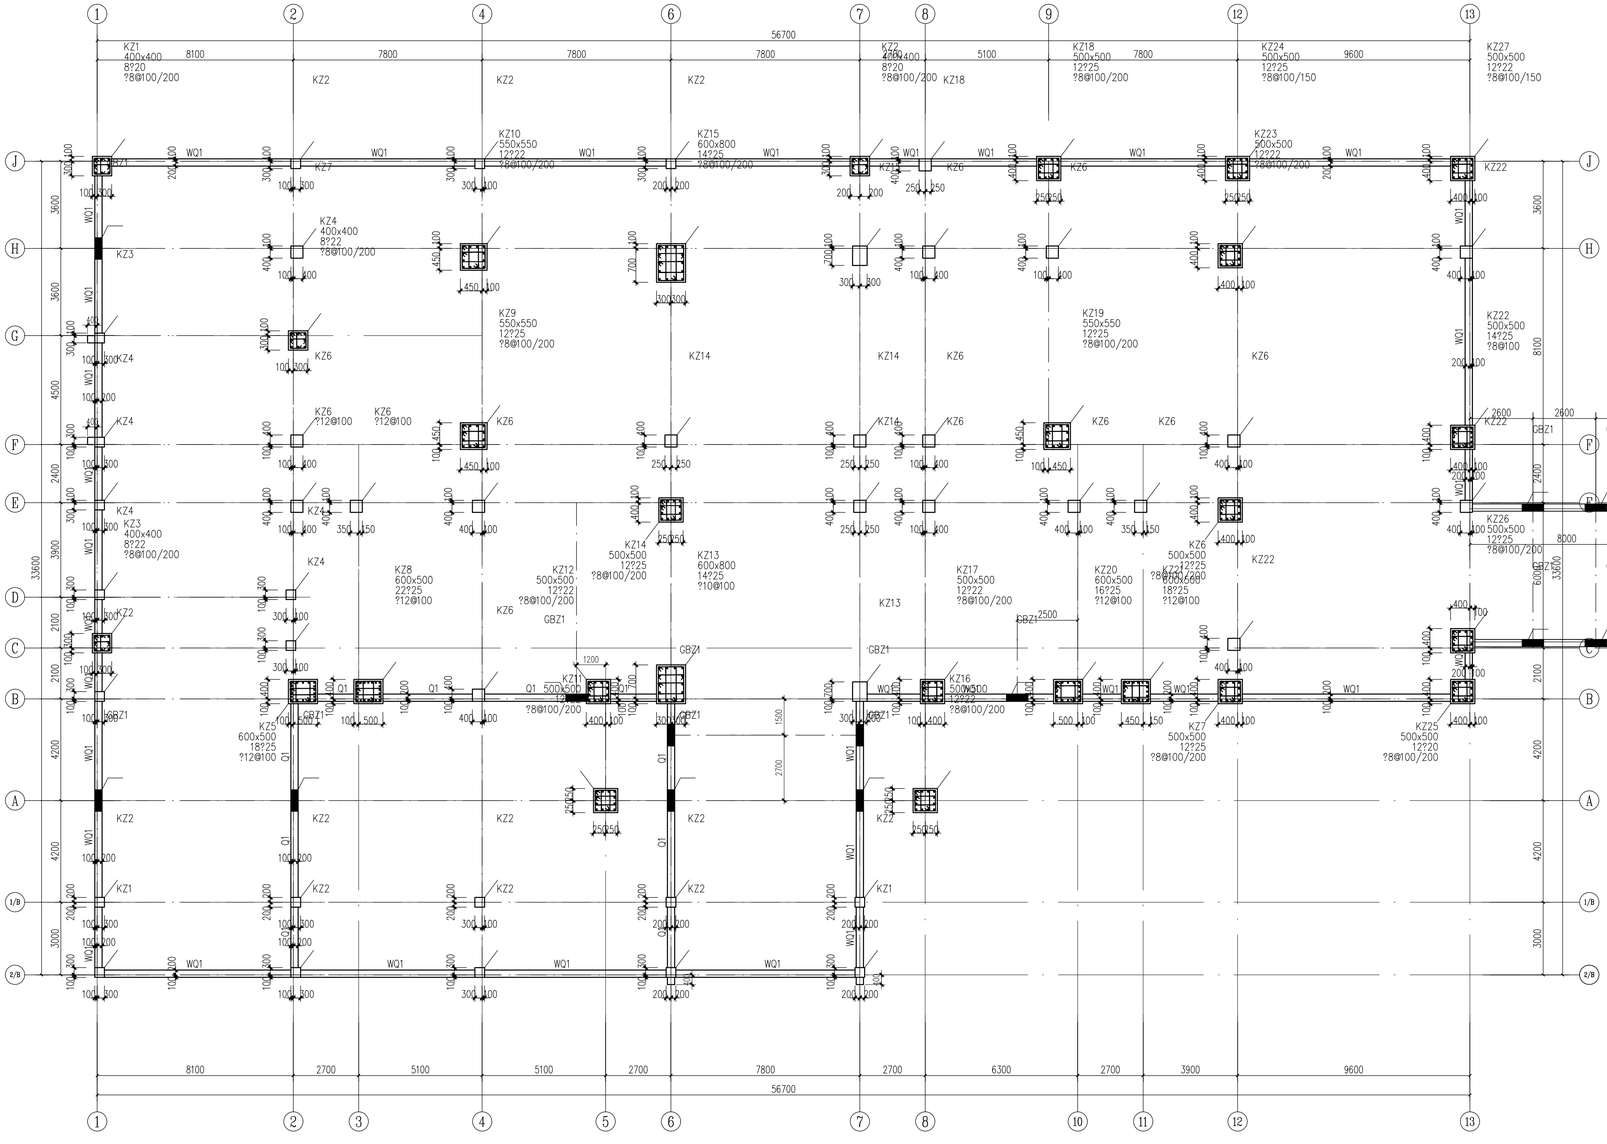

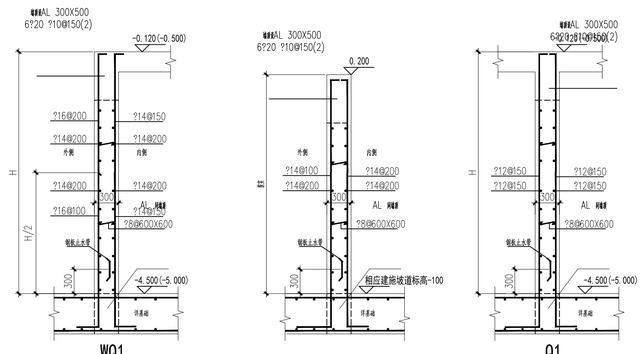
负一层（基础顶~-0.120,-0.500）墙、柱配筋平面图 1:100

| | | | |
|---|---|---|---|
| 设计单位 | 杭州园林设计院股份有限公司 HANGZHOU LANDSCAPE ARCHITECTURE DESIGN INSTITUTE CO.,LTD<br>建筑、风景园林甲级：A133013139<br>规划乙级：城规编（142056）<br>市政乙级：A233013136<br>文物保护工程勘察设计乙级：0102520002<br>公司地址：杭州市西湖区北山街120号西湖世纪中心17楼邮编<br>电话：0571-87021013 传真：0571-87021002 网址：www.hzyly.com | | |
| 建设单位 | 江苏茂源电气有限公司 | | |
| 工程总称 | 云创中心生产综合楼 | | |
| 子项名称 | 生产综合楼 | | |
| 图纸名称 | 负一层墙、柱配筋平面图 | | |
| | 姓 名 | 签 名 | |
| 审 定 | 张永龙 | | |
| 审 核 | 邵 文 | | |
| 项目负责人 | 朱 君 | | |
| 专业负责人 | 高 欣 | | |
| 设 计 | 高 欣 | | |
| 制 图 | 高 欣 | | |
| 校 对 | 罗孝敏 | | |
| 执业专用章 | 按规定加盖 | | |
| 出图章 | 未盖出图专用章无效 | | |
| 工号 | 25-14 | 图别 | 结施 |
| 图号 | 03 | 修改版次 | |
| 日期 | 2025.12 | | |

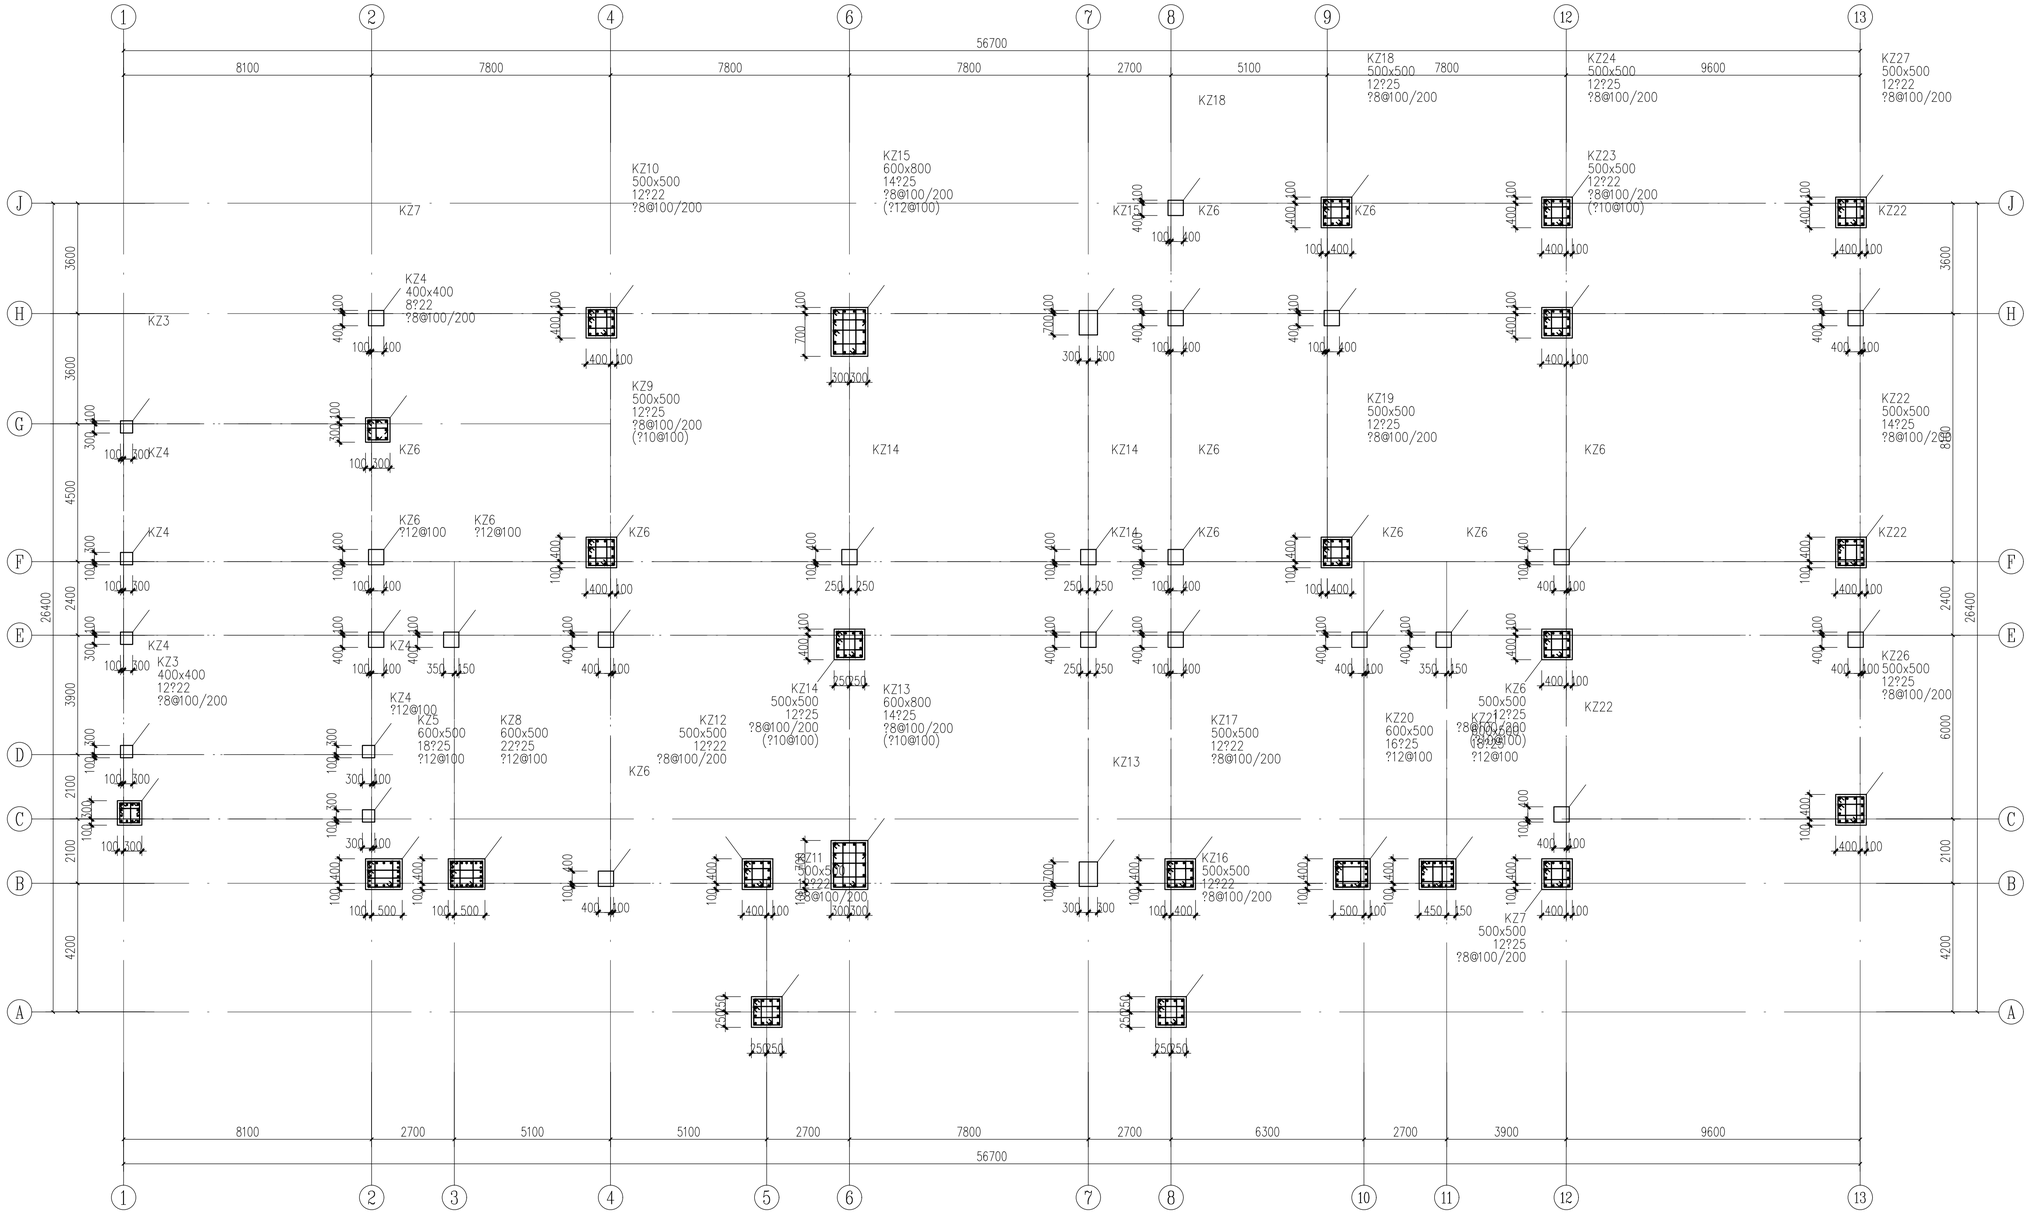


一层（-0.120~4.980,或相应屋面）柱配筋平面图 1:100

专业会签栏

| | |
|---|---|
| 园林 | 建筑 |
| | 结构 |
| 给排水 | |
| 电气 | 暖通 |
| | 器电 |

备注栏

设计单位

杭州园林设计院股份有限公司
HANGZHOU LANDSCAPE ARCHITECTURE DESIGN INSTITUTE CO.,LTD

建筑、风景园林甲级:A133013139
规划乙级:城规编（142056）
市政乙级:A233013136
文物保护工程勘察设计乙级:0102SJ00002

公司地址：杭州市西湖区双龙街38号西城世纪中心2号楼南楼
电话：0571-87031011　　传真：0571-87031002　　网址：www.hzyly.com

建设单位　江苏茂源电气有限公司

| | |
|---|---|
| 工程总称 | 云创中心生产综合楼 |
| 子项名称 | 生产综合楼 |
| 图纸名称 | 一层柱配筋平面图 |

| | 姓 名 | 签 名 |
|---|---|---|
| 审 定 | 张永龙 | |
| 审 核 | 郑 文 | |
| 项目负责人 | 朱 君 | |
| 专业负责人 | 高 欣 | |
| 设 计 | 高 欣 | |
| 制 图 | 高 欣 | |
| 校 对 | 罗孝敏 | |


执业专用章

按规定加盖

出图章

未盖出图专用章无效

| | | | |
|---|---|---|---|
| 工号 | 25-14 | 图别 | 结施 |
| 图号 | 04 | 修改版次 | |
| 日期 | 2025.12 | | |

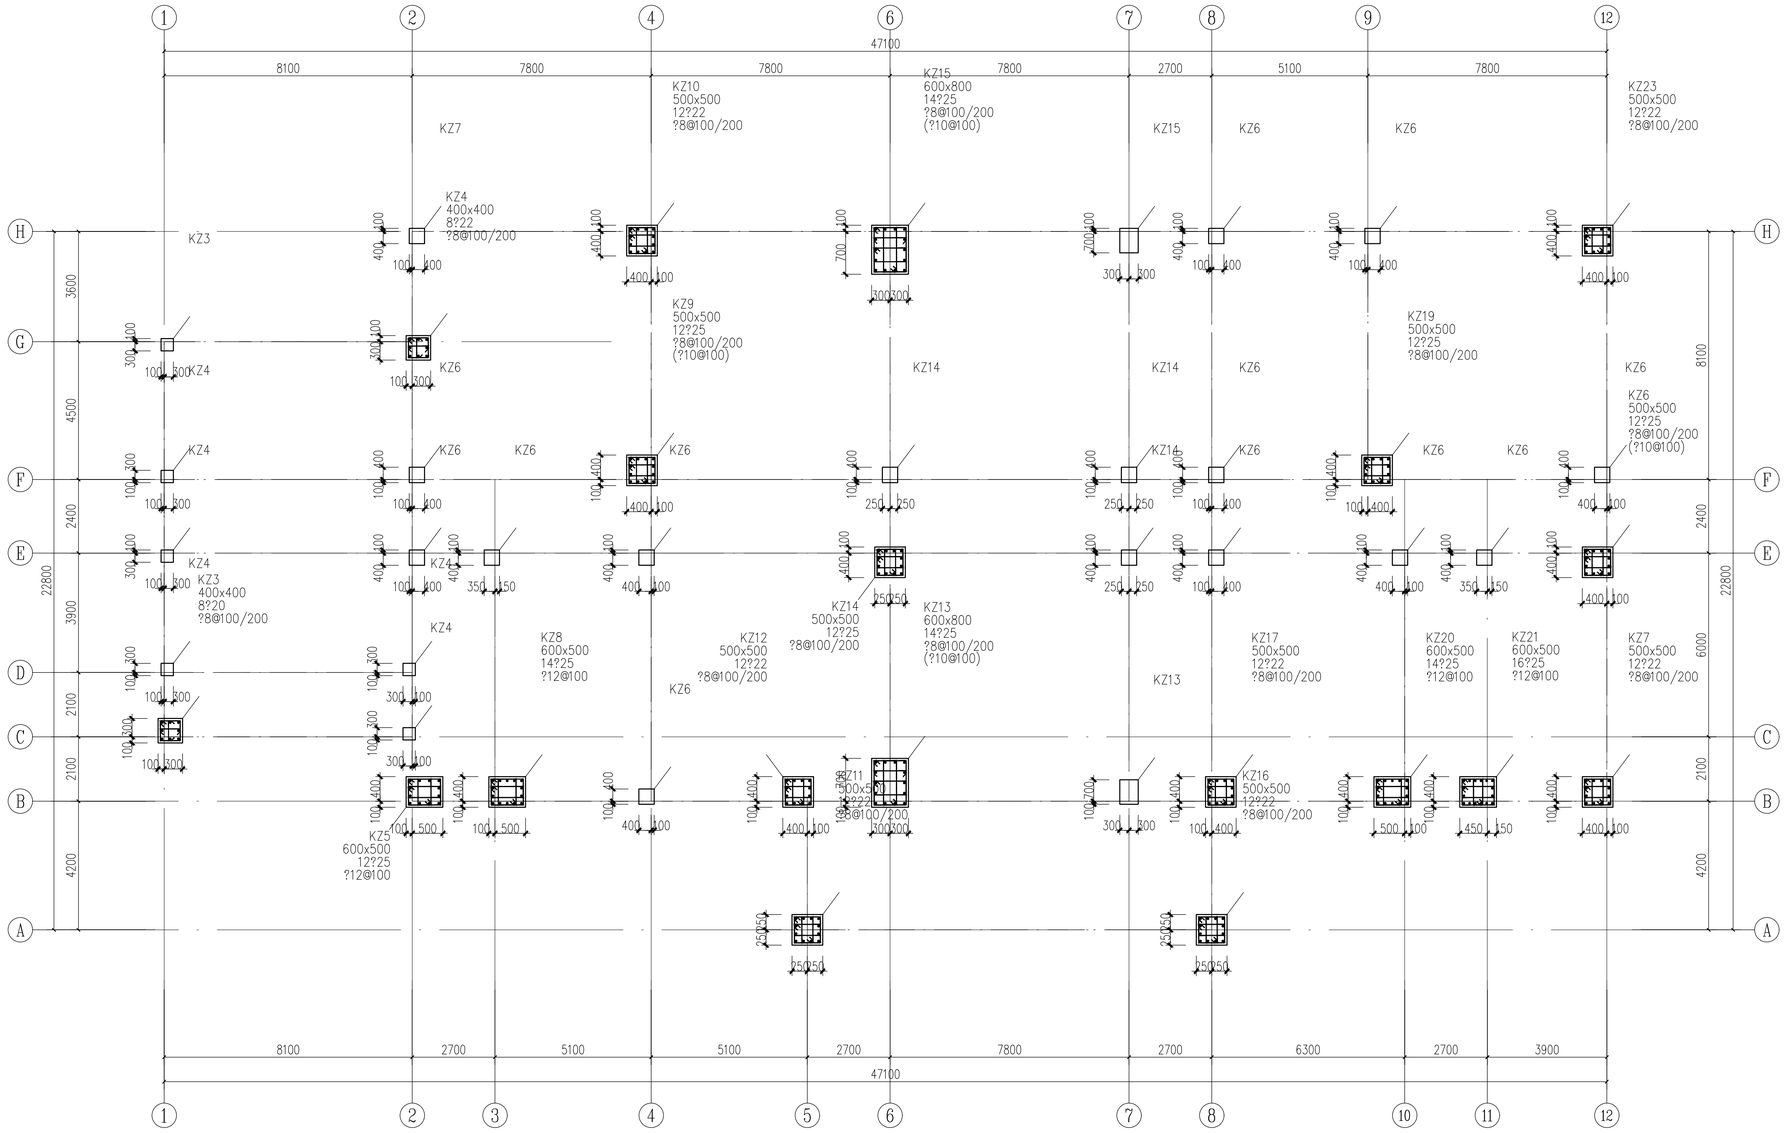


二层（4.980~9.480,或相应屋面）柱配筋平面图 1:100

备注栏

设计单位

杭州园林设计院股份有限公司
HANGZHOU LANDSCAPE ARCHITECTURE DESIGN INSTITUTE CO.,LTD
建筑、风景园林甲级:A133013139
规划乙级:城规编（142056）
市政乙级:A233013136
文物保护工程勘察设计乙级:0102SJ0002
公司地址：杭州市西湖区双龙街138号西湖世纪中心2号楼南楼
电话：0571-87031011　　传真：0571-87031002　　网址：www.hzyly.com

建设单位 江苏茂源电气有限公司

| | |
|---|---|
| 工程总称 | 云创中心生产综合楼 |
| 子项名称 | 生产综合楼 |
| 图纸名称 | 二层柱配筋平面图 |

| | 姓 名 | 签 名 |
|---|---|---|
| 审 定 | 张永龙 | |
| 审 核 | 郑 文 | |
| 项目负责人 | 朱 君 | |
| 专业负责人 | 高 欣 | |
| 设 计 | 高 欣 | |
| 制 图 | 高 欣 | |
| 校 对 | 罗孝敏 | |

执业专用章


按规定加盖

出图章

未盖出图专用章无效

| | | | |
|---|---|---|---|
| 工号 | 25-14 | 图别 | 结施 |
| 图号 | 05 | 修改版次 | |
| 日期 | 2025.12 | | |

专业会签栏：园林 建筑 结构 给排水 电气 暖通 器电

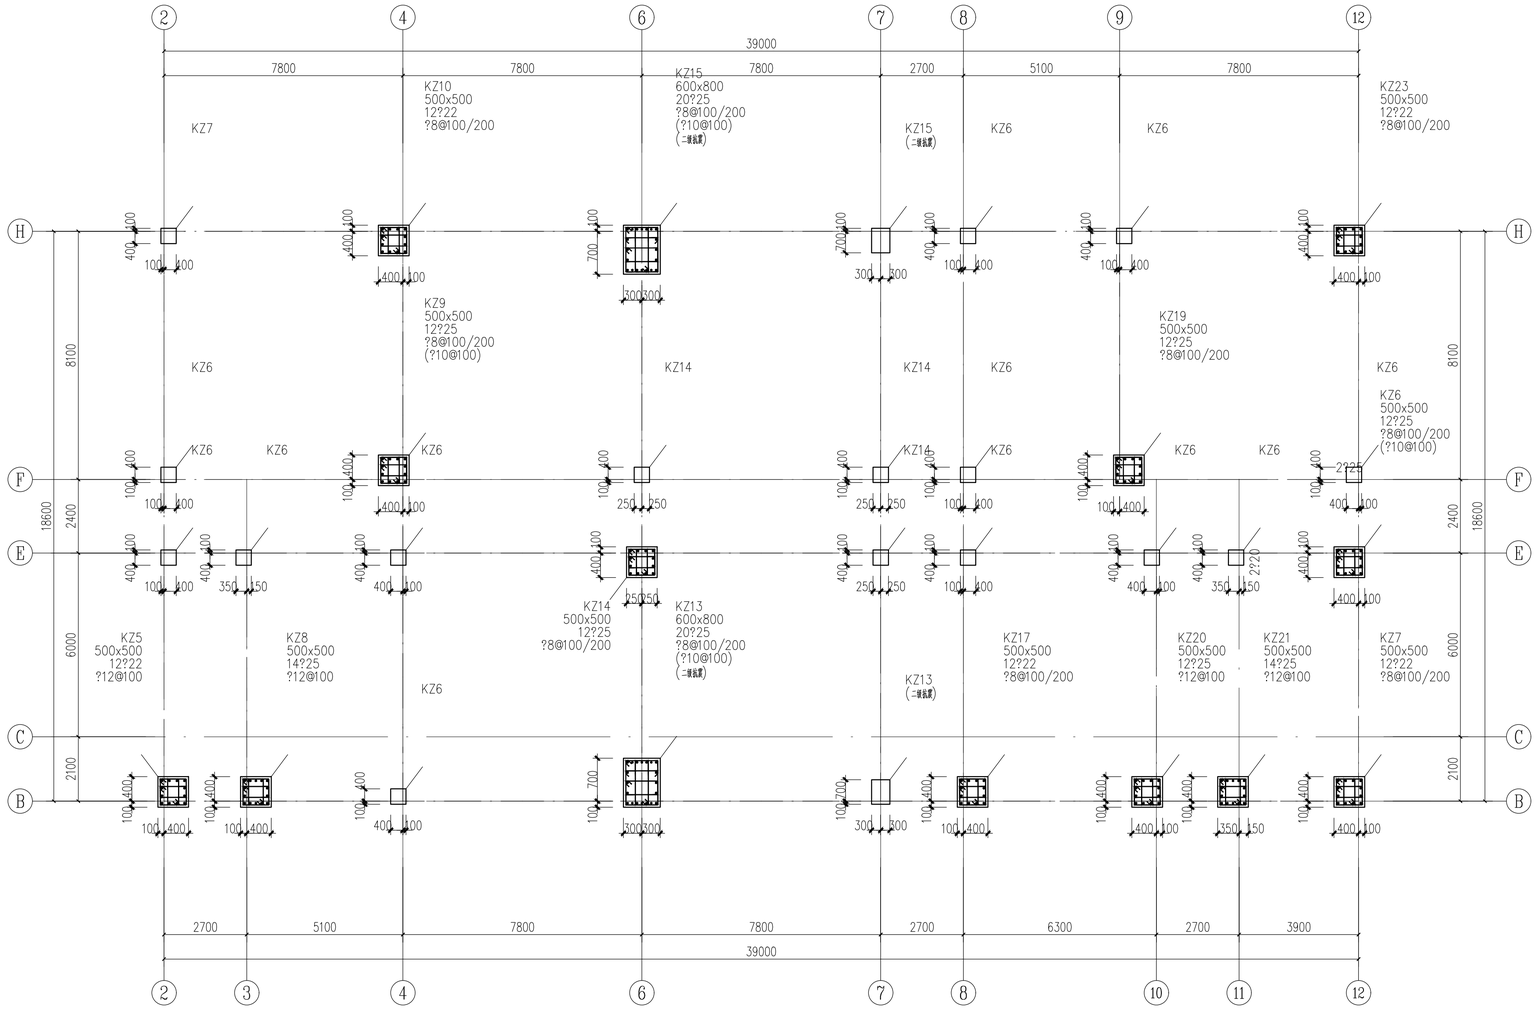


三层（9.480~13.980）柱配筋平面图 1:100

备注栏

设计单位

杭州园林设计院股份有限公司
HANGZHOU LANDSCAPE ARCHITECTURE DESIGN INSTITUTE CO.,LTD
建筑、风景园林甲级:A133013139
规划乙级:城规编（142056）
市政乙级:A233013136
文物保护工程勘察设计乙级:0102SJ0002
公司地址：杭州市西湖区双龙街136号西溪世纪中心2号楼南楼
电话：0571-87631011　　传真：0571-87631002　　网址：www.hzyls.com

建设单位 江苏茂源电气有限公司

| | |
|---|---|
| 工程总称 | 云创中心生产综合楼 |
| 子项名称 | 生产综合楼 |
| 图纸名称 | 三层柱配筋平面图 |

| | 姓 名 | 签 名 |
|---|---|---|
| 审 定 | 张永龙 | |
| 审 核 | 郑 文 | |
| 项目负责人 | 朱 君 | |
| 专业负责人 | 高 欣 | |
| 设 计 | 高 欣 | |
| 制 图 | 高 欣 | |
| 校 对 | 罗孝敏 | |

执业专用章

按规定加盖


出图章

未盖出图专用章无效

| | | | |
|---|---|---|---|
| 工号 | 25-14 | 图别 | 结施 |
| 图号 | 06 | 修改版次 | |
| 日期 | 2025.12 | | |

专业会签栏

| | | | | | | | |
|---|---|---|---|---|---|---|---|
| 园林 | 建筑 | 结构 | 给排水 | 暖通 | 电气 | 暖通 | 强电 |

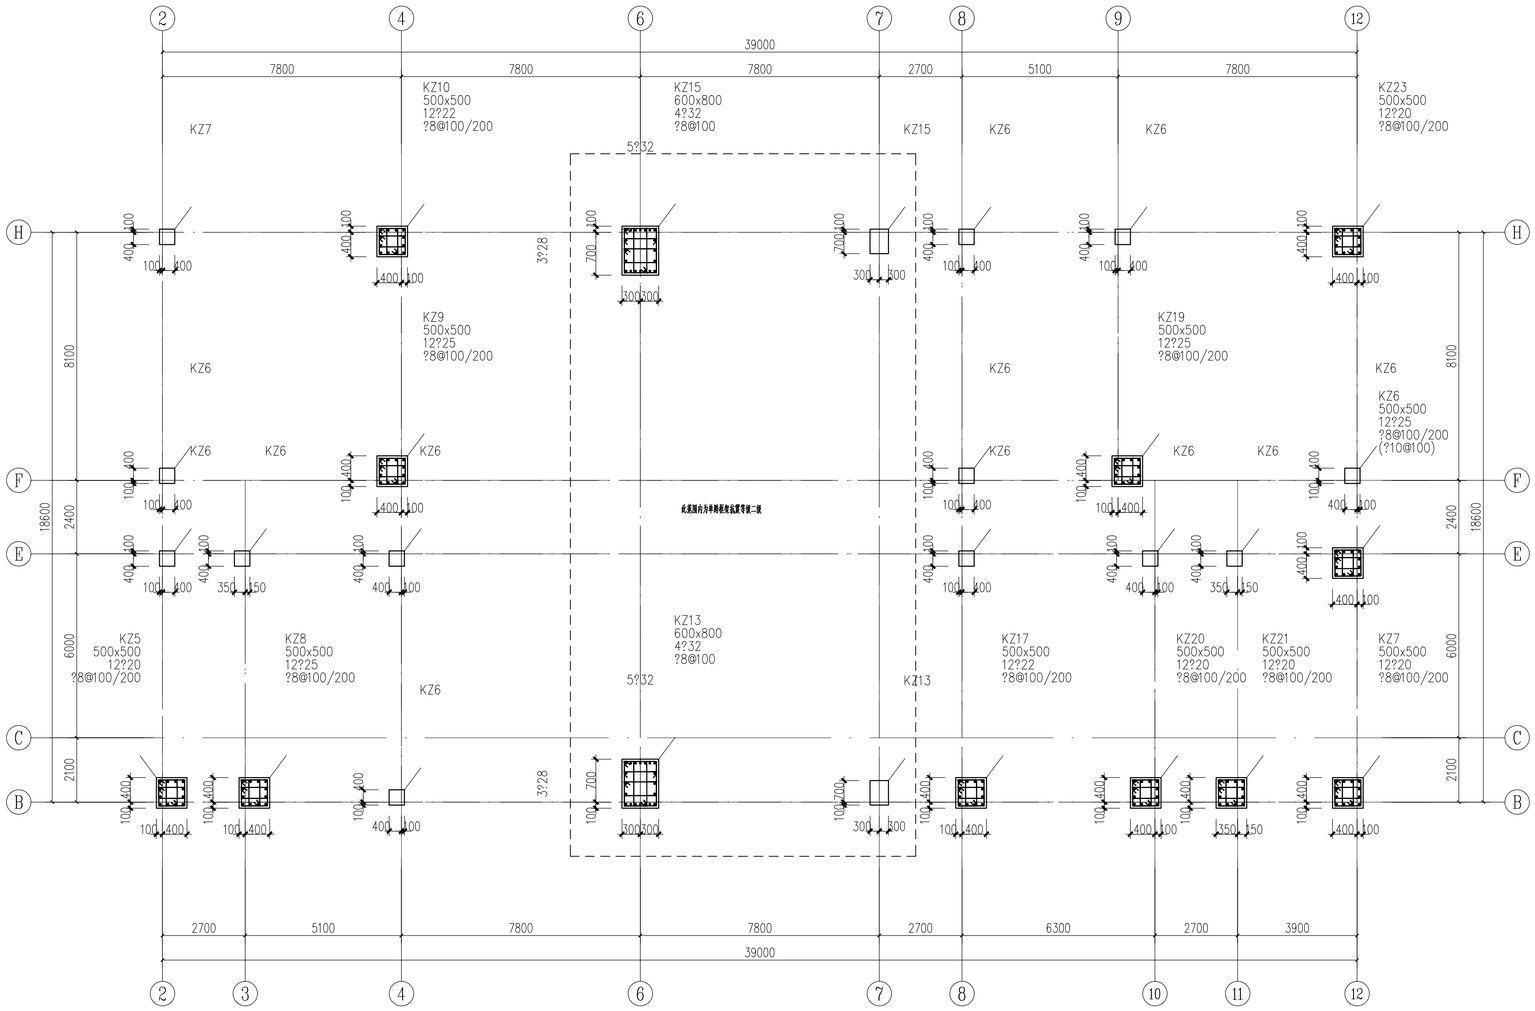


四层（13.980~相应屋面）柱配筋平面图 1:100

| 专业会签栏 | 园林 | 建筑 | 结构 | 给排水 | 电气 | 暖通 | 器电 |
|---|---|---|---|---|---|---|---|

备注栏

设计单位

杭州园林设计院股份有限公司
HANGZHOU LANDSCAPE ARCHITECTURE DESIGN INSTITUTE CO.,LTD

建筑、风景园林甲级:A133013139
规划乙级:城规编（1420356）
市政乙级:A233013136
文物保护工程勘察设计乙级:0102SJ00002

公司地址：杭州市西湖区双龙街138号西溪世纪中心5号楼南楼
电话：0571-87031011　　传真：0571-87031092　　网址：www.hzyly.com

建设单位：江苏茂源电气有限公司

| | |
|---|---|
| 工程总称 | 云创中心生产综合楼 |
| 子项名称 | 生产综合楼 |
| 图纸名称 | 四层柱配筋平面图 |

| | 姓 名 | 签 名 |
|---|---|---|
| 审 定 | 张永龙 | |
| 审 核 | 郑 文 | |
| 项目负责人 | 朱 君 | |
| 专业负责人 | 高 欣 | |
| 设 计 | 高 欣 | |
| 制 图 | 高 欣 | |
| 校 对 | 罗孝敏 | |

执业专用章


按规定加盖

出图章

未盖出图专用章无效

| 工号 | 25-14 | 图别 | 结施 |
|---|---|---|---|
| 图号 | 07 | 修改版次 | |
| 日期 | 2025.12 | | |

专业会签栏 | 结构 | 给排水 | 电气 | 暖通 | 空调 | 园林 | 建筑 | 弱电

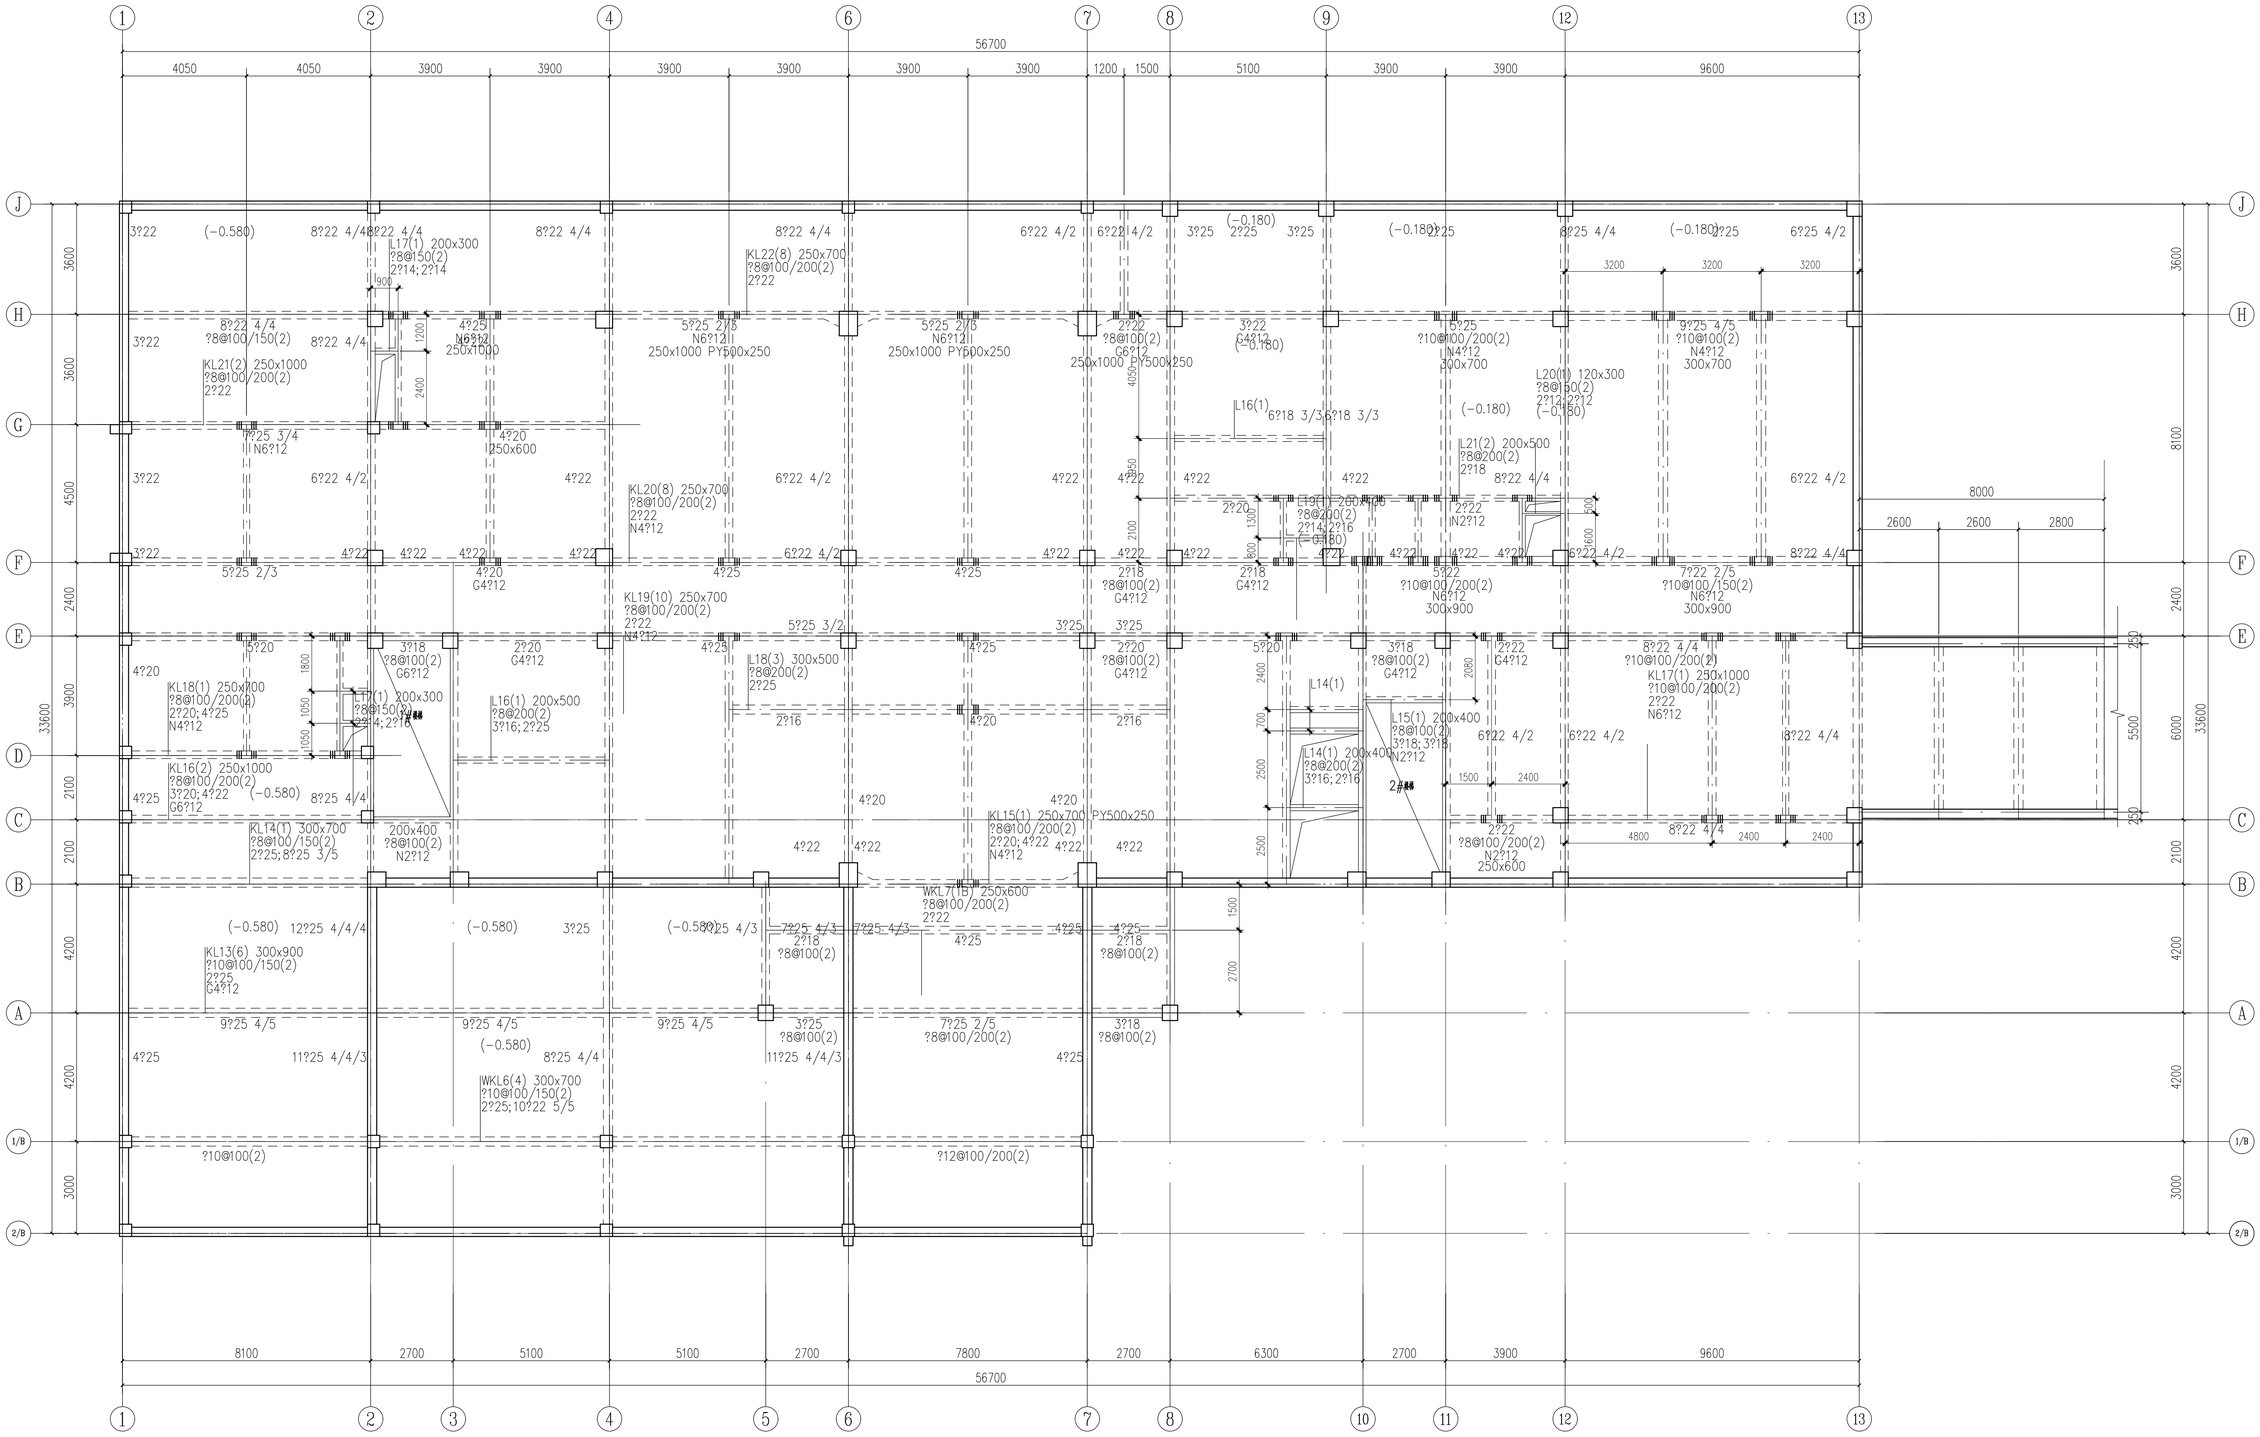


# 一层(-0.120)梁配筋平面图1 1:100

1. 本层梁基准标高(除注明外)为-0.120，梁标注括号中数字为相对基准标高的高差值
2. 主次梁箍筋加密为相应主梁箍筋每边加密3道@50。
3. 水管穿梁应结合水施预埋套管，避免后凿

备注栏

设计单位

杭州园林设计院股份有限公司
HANGZHOU LANDSCAPE ARCHITECTURE DESIGN INSTITUTE CO, LTD
建筑、风景园林甲级:A133013139
规划乙级:城规编（142056）
市政乙级:A233013139
文物保护工程勘察设计乙级:0102SJ0002
公司地址：杭州市西湖区双龙街138号西城世纪中心5号楼南楼
电话：0571-87031011 传真：0571-87031092 网址：www.hzyly.com

| 建设单位 | 江苏茂源电气有限公司 | | |
|---|---|---|---|
| 工程总称 | 云创中心生产综合楼 | | |
| 子项名称 | 生产综合楼 | | |
| 图纸名称 | 一层梁配筋平面图1 | | |
| | 姓 名 | 签 名 | |
| 审 定 | 张永龙 | | |
| 审 核 | 郑 文 | | |
| 项目负责人 | 朱 君 | | |
| 专业负责人 | 高 欣 | | |
| 设 计 | 高 欣 | | |
| 制 图 | 高 欣 | | |
| 校 对 | 罗孝敏 | | |

执业专用章

按规定加盖


出图章

未盖出图专用章无效

| 工号 | 25-14 | 图别 | 结施 |
|---|---|---|---|
| 图号 | 08 | 修改版次 | |
| 日期 | 2025.12 | | |

专业会签栏

| 园林 | 结构 | 电气 | 暖通 | 给排水 | 建筑 | 电 |
|---|---|---|---|---|---|---|
| | | | | | | |

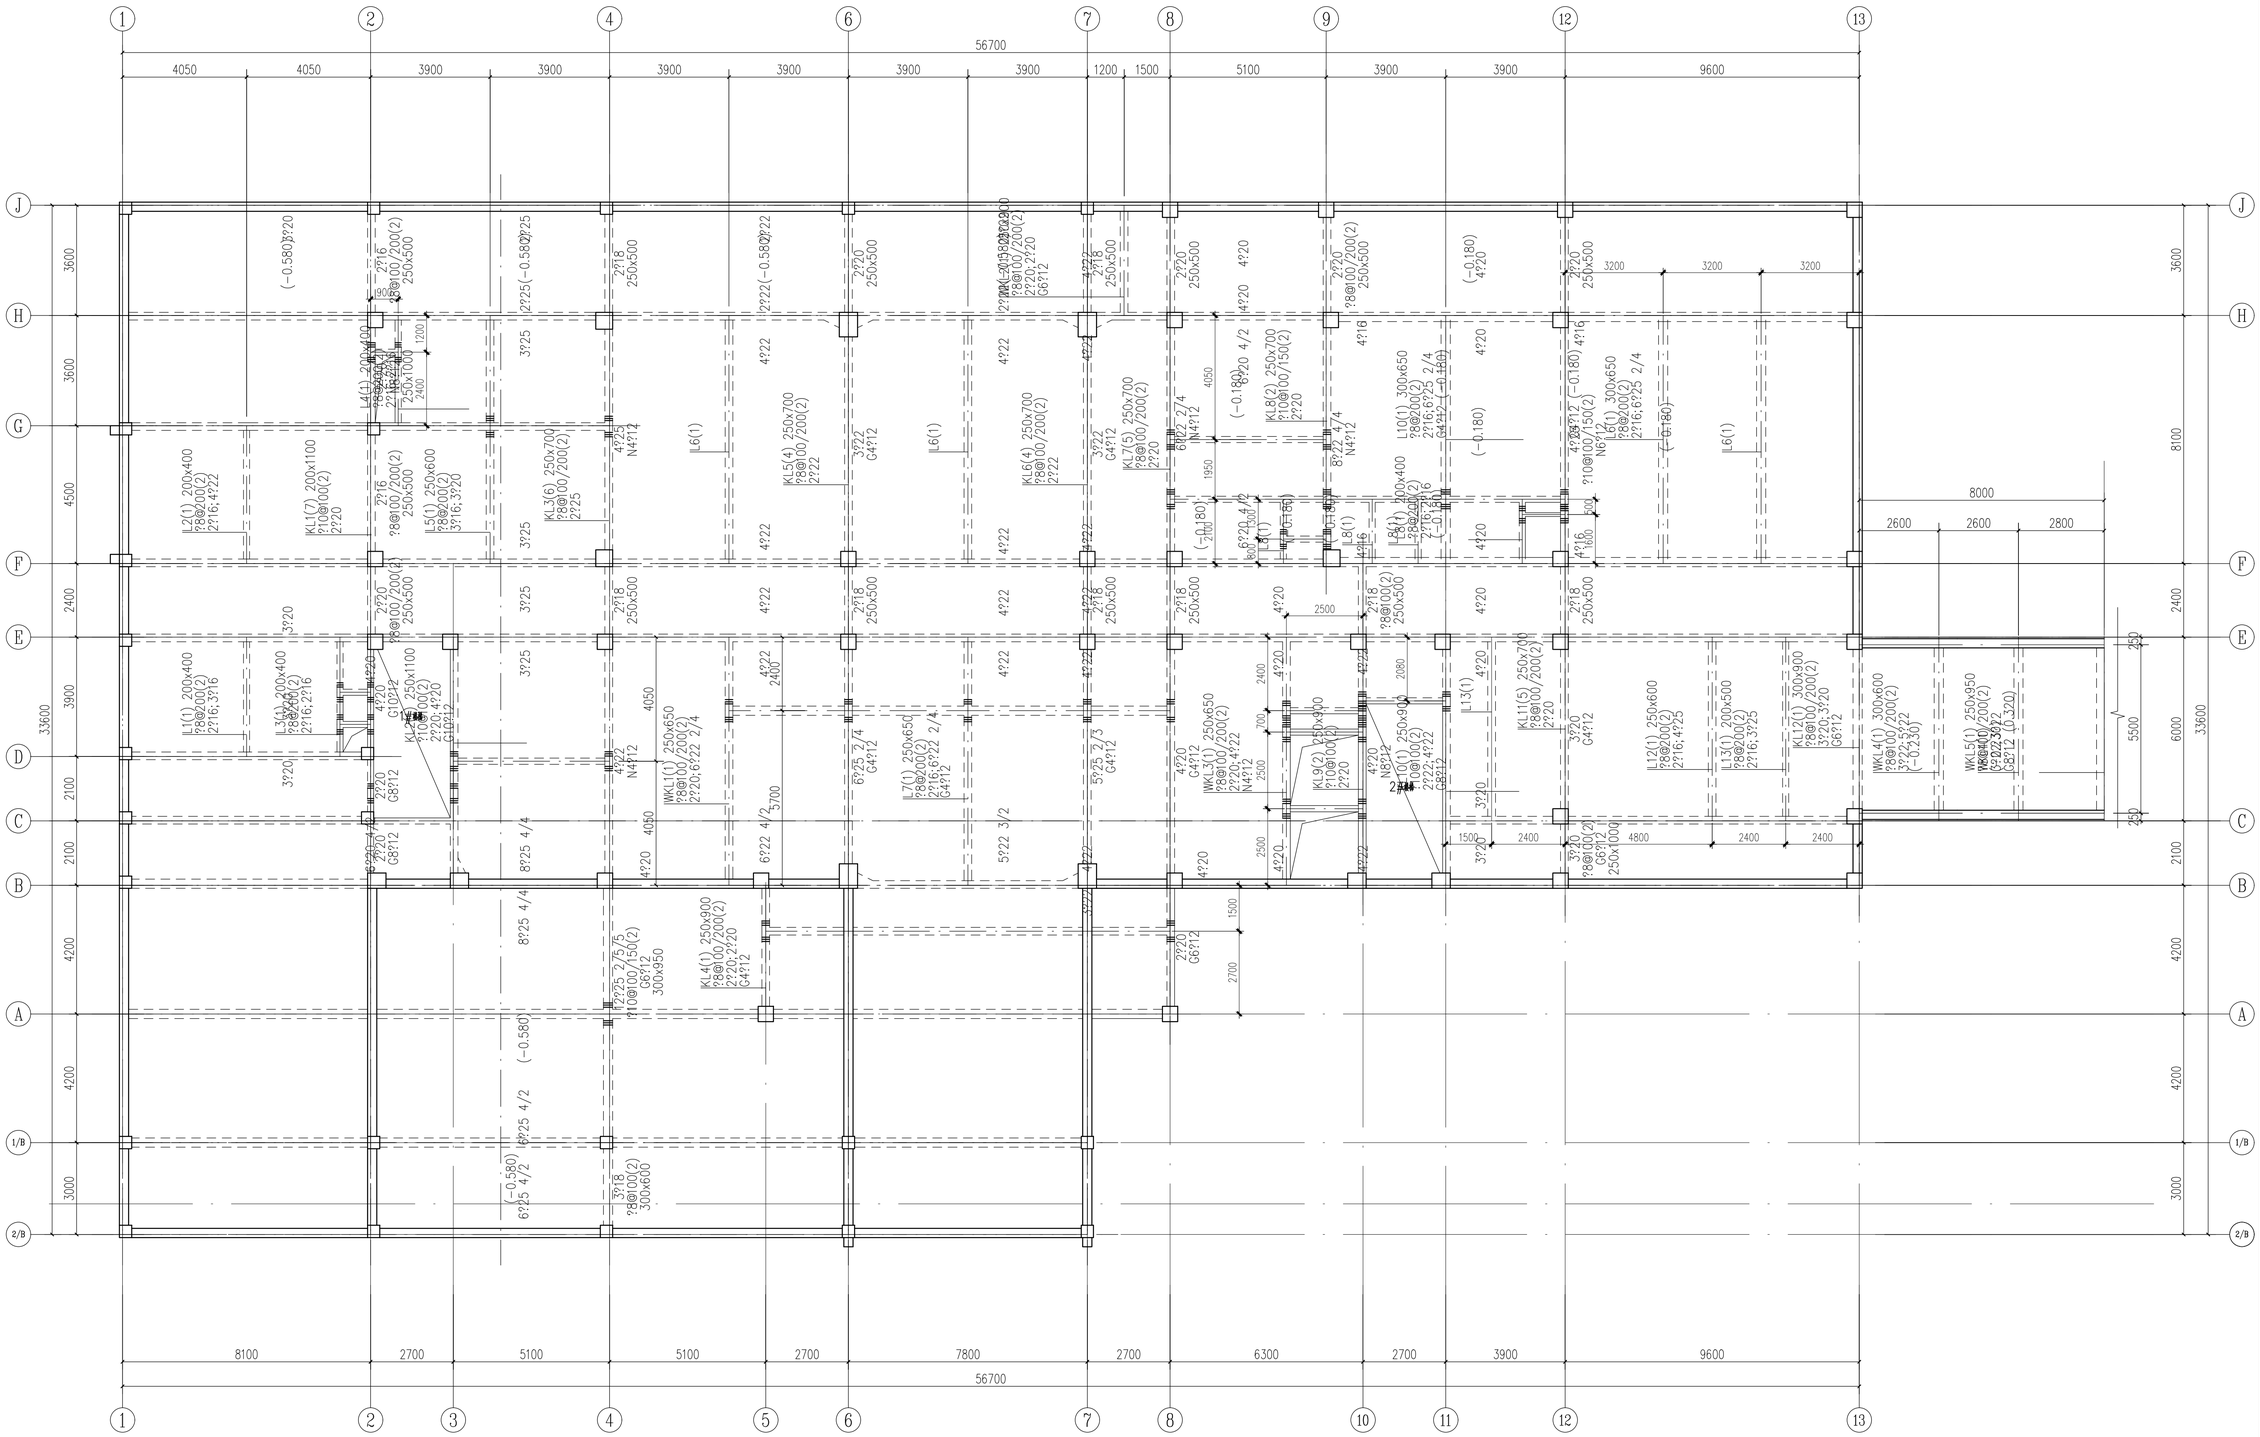


## 一层(-0.120)梁配筋平面图2 1:100

1. 本层梁基准标高(除注明外)为-0.120，梁标注括号中数字为相对基准标高的高差值
2. 主次梁集箍加密为相应主梁集箍每边加密3道@50。
3. 水管穿梁应结合水施预埋套管，避免后凿

备注栏

设计单位

杭州园林设计院股份有限公司
HANGZHOU LANDSCAPE ARCHITECTURE DESIGN INSTITUTE CO.,LTD
建筑、风景园林甲级:A133013139
规划乙级:城规编(142056)
市政乙级:A233013136
文物保护工程勘察设计乙级:0102SJ0002
公司地址：杭州市西湖区双龙街136号西溪世纪中心2号楼南楼
电话：0571-87031011　　传真：0571-87031092　　网址：www.hzyls.com

建设单位：江苏茂源电气有限公司

| | |
|---|---|
| 工程总称 | 云创中心生产综合楼 |
| 子项名称 | 生产综合楼 |
| 图纸名称 | 一层梁配筋平面图2 |

| | 姓名 | 签名 |
|---|---|---|
| 审定 | 张永龙 | |
| 审核 | 郑文 | |
| 项目负责人 | 朱君 | |
| 专业负责人 | 高欣 | |
| 设计 | 高欣 | |
| 制图 | 高欣 | |
| 校对 | 罗孝敏 | |


执业专用章


按规定加盖

出图章

未盖出图专用章无效

| 工号 | 25-14 | 图别 | 结施 |
|---|---|---|---|
| 图号 | 09 | 修改版次 | |
| 日期 | 2025.12 | | |

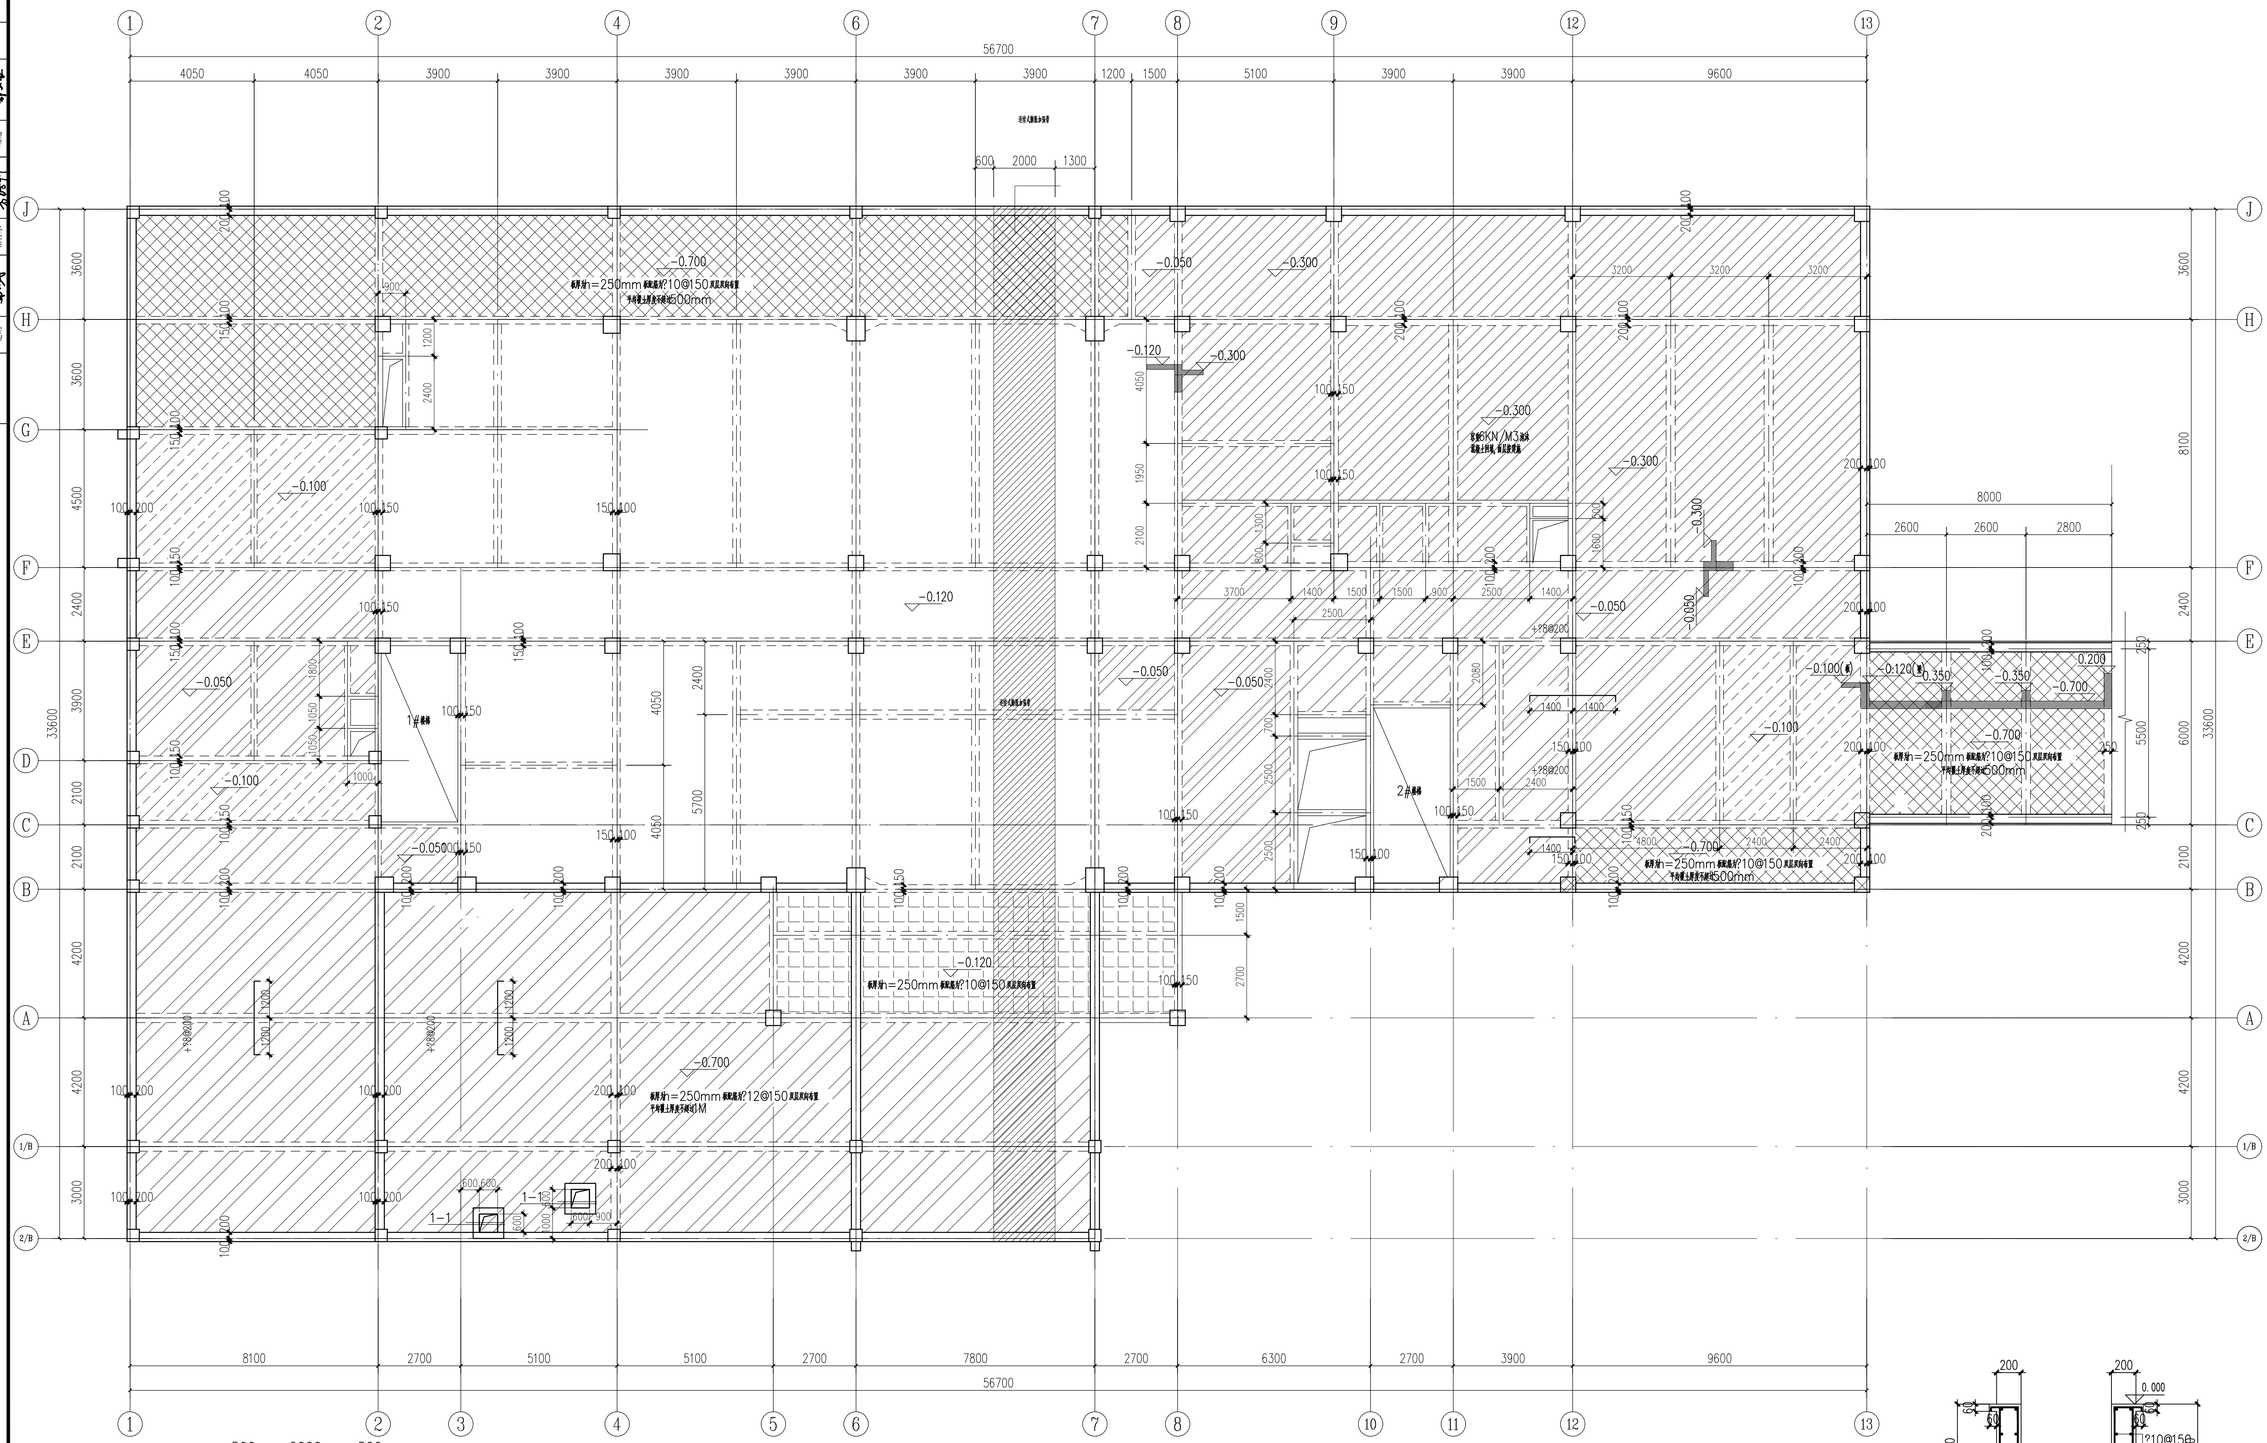
1
2
4
6
7
8
9
12
13
56700
4050
4050
3900
3900
3900
3900
3900
3900
1200
1500
5100
3900
3900
9600
600
2000
1300
J
H
G
F
E
D
C
B
A
1/B
2/B
3600
3600
4500
2400
3900
2100
4200
4200
3000
8100
6000
5500
2500
2500
-0.700
板厚h=250mm 板配直径?10@150 双层双向布置
平布置上排直至延伸500mm
-0.050
-0.300
-0.120
-0.100
-0.350
0.200
-0.350
-0.700
-0.700
板厚h=250mm 板配直径?10@150 双层双向布置
平布置上排直至延伸500mm
-0.700
板厚h=250mm 板配直径?12@150 双层双向布置
平布置上排直至延伸1M
-0.120
板厚h=250mm 板配直径?10@150 双层双向布置
-0.050
-0.100
-0.050
-0.120
-0.300
-0.300
-0.300
-0.300
-0.050
-0.050
-0.100
-0.050
-0.050
-0.100
-0.120
-0.050
-0.050
-0.100
-0.050
-0.050
-0.100
-0.050
-0.050
-0.100

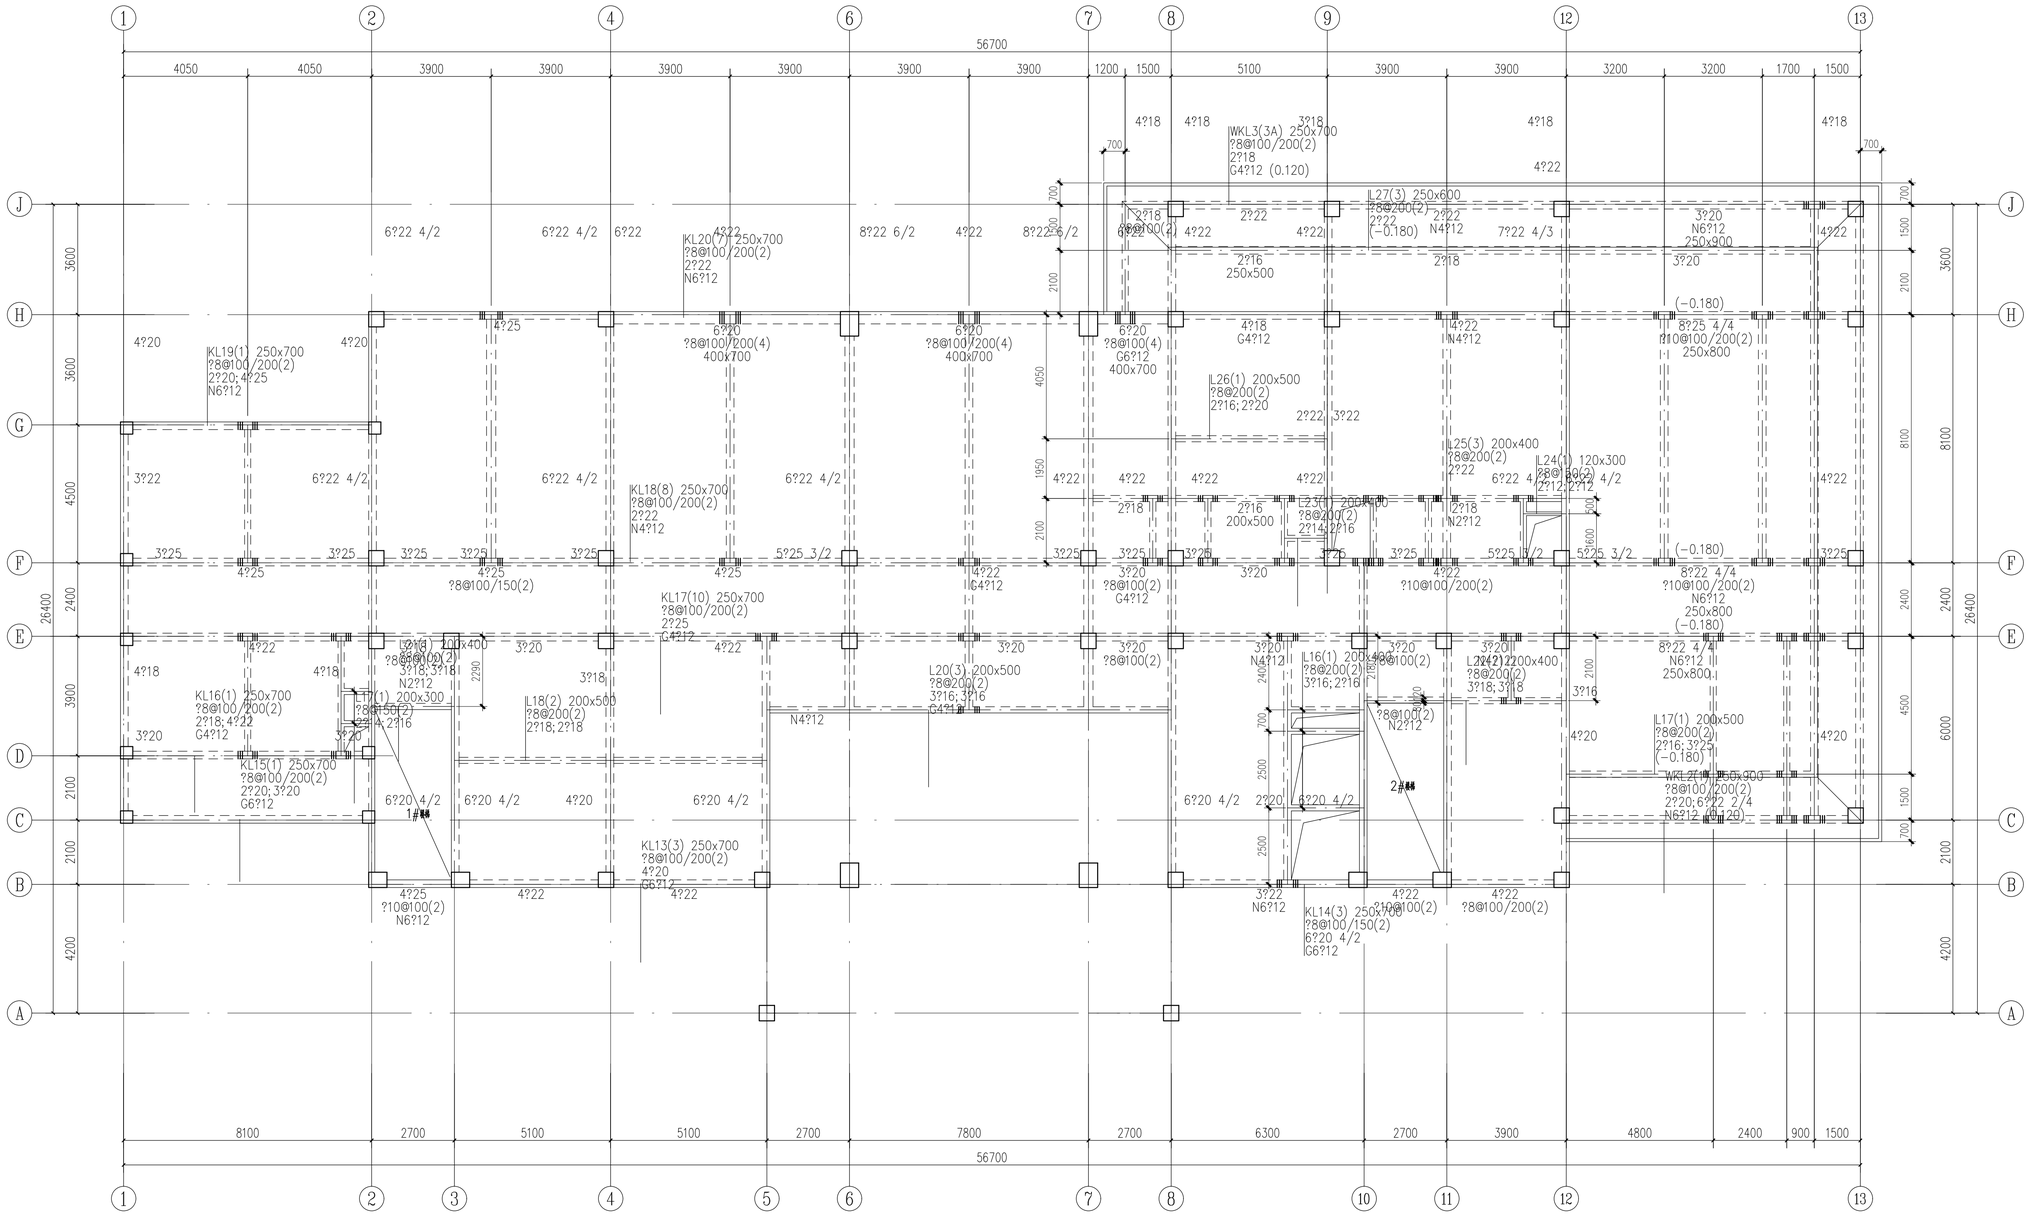


## 二层(4.980)梁配筋平面图1 1:100

1. 本层梁基准标高(除注明外)为4.980，梁标注括号中数字为相对基准标高的高差值
2. 主次梁箍筋加密为相应主梁箍筋每边加密3道@50。
3. 水管穿梁应结合水施预埋套管，避免后凿

备注栏

设计单位

杭州园林设计院股份有限公司
HANGZHOU LANDSCAPE ARCHITECTURE DESIGN INSTITUTE CO.,LTD
建筑、风景园林甲级:A133013139
规划乙级:城规编（142056）
市政乙级:A233013136
文物保护工程勘察设计乙级:0102SJ0002
公司地址：杭州市西湖区双龙街38号西湖世纪中心25号楼南楼
电话：0571-87931011　　传真：0571-87931002　　网址：www.hzylc.com

建设单位 江苏茂源电气有限公司

| | |
|---|---|
| 工程总称 | 云创中心生产综合楼 |
| 子项名称 | 生产综合楼 |
| 图纸名称 | 二层梁配筋平面图1 |

| | 姓 名 | 签 名 |
|---|---|---|
| 审 定 | 张水龙 | |
| 审 核 | 郑 文 | |
| 项目负责人 | 朱 君 | |
| 专业负责人 | 高 欣 | |
| 设 计 | 高 欣 | |
| 制 图 | 高 欣 | |
| 校 对 | 罗孝敏 | |

执业专用章

按规定加盖

出图章


未盖出图专用章无效


| | | | |
|---|---|---|---|
| 工号 | 25-14 | 图别 | 结施 |
| 图号 | 11 | 修改版次 | |
| 日期 | 2025.12 | | |


专业会签栏：结构 张水龙；给排水 郑文；电气 戚德；暖通 朱君；建筑 高欣；园林 高欣；弱电

专业会签栏

| 园林 | | 结构 | | 电气 | | 给排水 | | 暖通 | | 弱电 | |
|---|---|---|---|---|---|---|---|---|---|---|---|
| 建筑 | | 给排水 | | 暖通 | | 电气 | | 弱电 | | 结构 | |

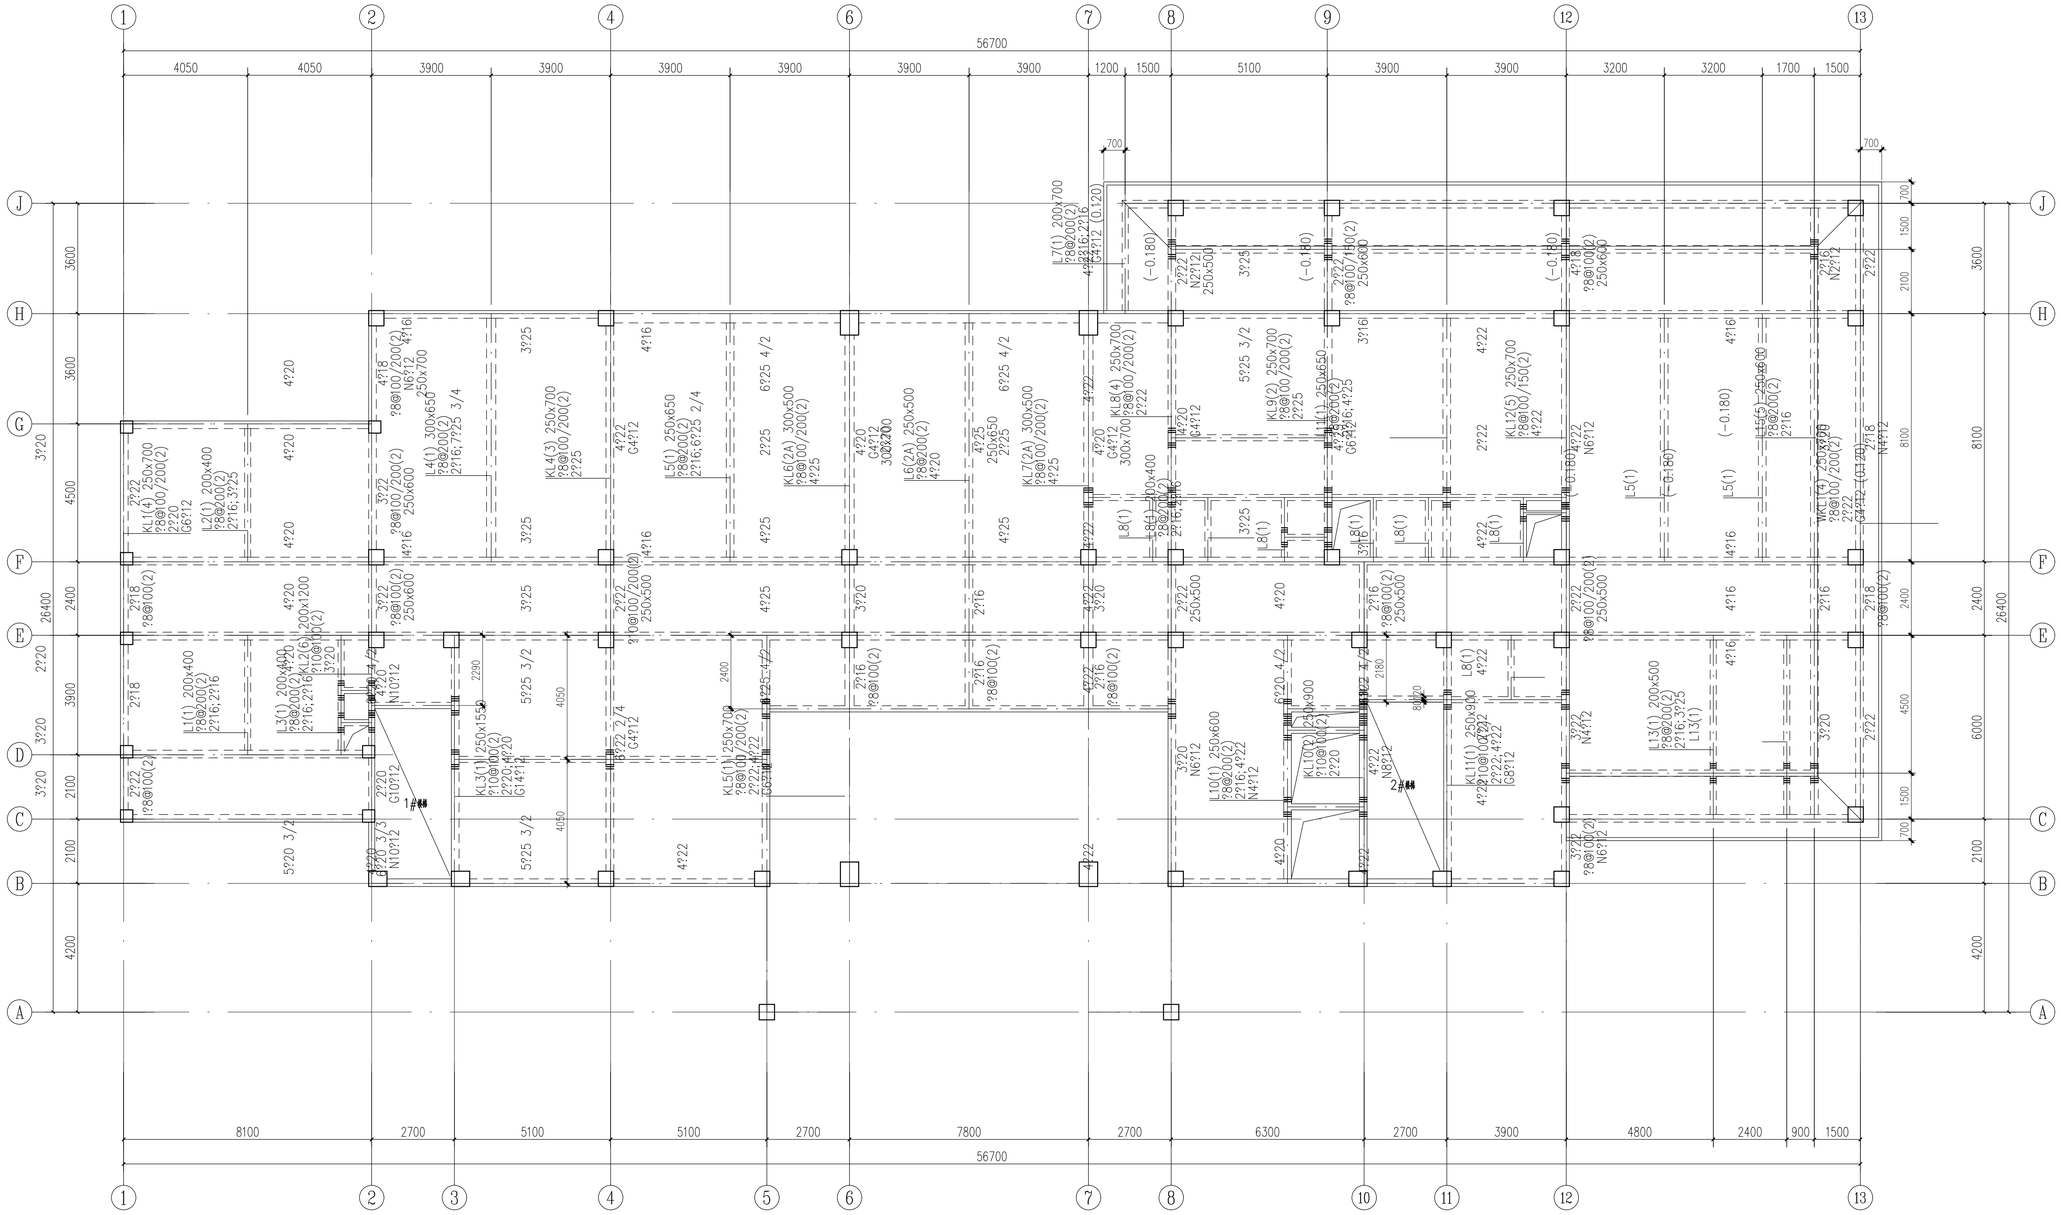
1
2
3
4
5
6
7
8
9
10
11
12
13
A
B
C
D
E
F
G
H
J
56700
4050 4050 3900 3900 3900 3900 3900 3900 1200 1500 5100 3900 3900 3200 3200 1700 1500
8100 2700 5100 5100 2700 7800 2700 6300 2700 3900 4800 2400 900 1500
3600 3600 4500 2400 2100 4200
3600 8100 2400 6000 2100 4200
700
1#楼梯
2#楼梯
(-0.180)
(-0.160)
L7(1) 200x700 ?8@200(2) 2?16;2?16 G4?12 (0.120)
KL1(4) 250x700 ?8@100/200(2) 2?20 G6?12
L2(1) 200x400 ?8@200(2) 2?16;3?25
L4(1) 300x650 ?8@200(2) 2?16;7?25 3/4
KL4(3) 250x700 ?8@100/200(2) 2?25
L5(1) 250x650 ?8@200(2) 2?16;6?25 2/4
KL6(2A) 300x500 ?8@100/200(2) 4?25
KL7(2A) 300x500 ?8@100/200(2) 4?25
L6(2A) 250x500 ?8@200(2) 4?20
KL8(4) 250x700 ?8@100/200(2)
KL9(2) 250x700 ?8@100/200(2) 2?25
L1(1) 250x650 ?8@200(2) G6?16;4?25
KL12(5) 250x700 ?8@100/150(2) 4?22
L5(1)
WKL1(4) 250x700 ?8@100/200(2) G4?12 (0.120)
L3(1) 200x400 ?8@200(2) 2?16;2?16
L2(6) 200x1200 ?10@100(2) 3?20
KL3(1) 250x1550 ?10@100(2) 2?20;4?20 G4?12
KL5(1) 250x700 ?8@100/200(2) 2?22;4?22 G6?12
L10(1) 250x600 ?8@200(2) 2?16;4?22 N4?12
KL10(2) 250x900 ?10@100(2) 2?20
KL11(1) 250x900 ?10@100(2) 2?22;4?22 G8?12
L8(1)
L13(1) 200x500 ?8@200(2) 2?16;3?25
L13(1)
N6?12
N2?12
N4?12
N8?12
N10?12
G10?12
G14?12
5?25 3/2
5?20 3/2
6?25 4/2
6?20 4/2
4?22 2/4
3?22 2/4
3?22 3/5
4?22
4?20
4?16
3?25
3?20
3?16
2?22
2?18
2?16
2?20
2?25
2?22;4?22
2?22;3?25
2?16;2?16
2?16;3?25
2?16;4?22
2?16;6?25
2?16;7?25
2?16;4?25
2?16;2?16
2?16;4?22
2?16;3?25
2?16;4?25
2?16;6?25
2?16;7?25
2?16;4?25
2?16;6?25
2?16;4?25
2?16;4?22
2?16;3

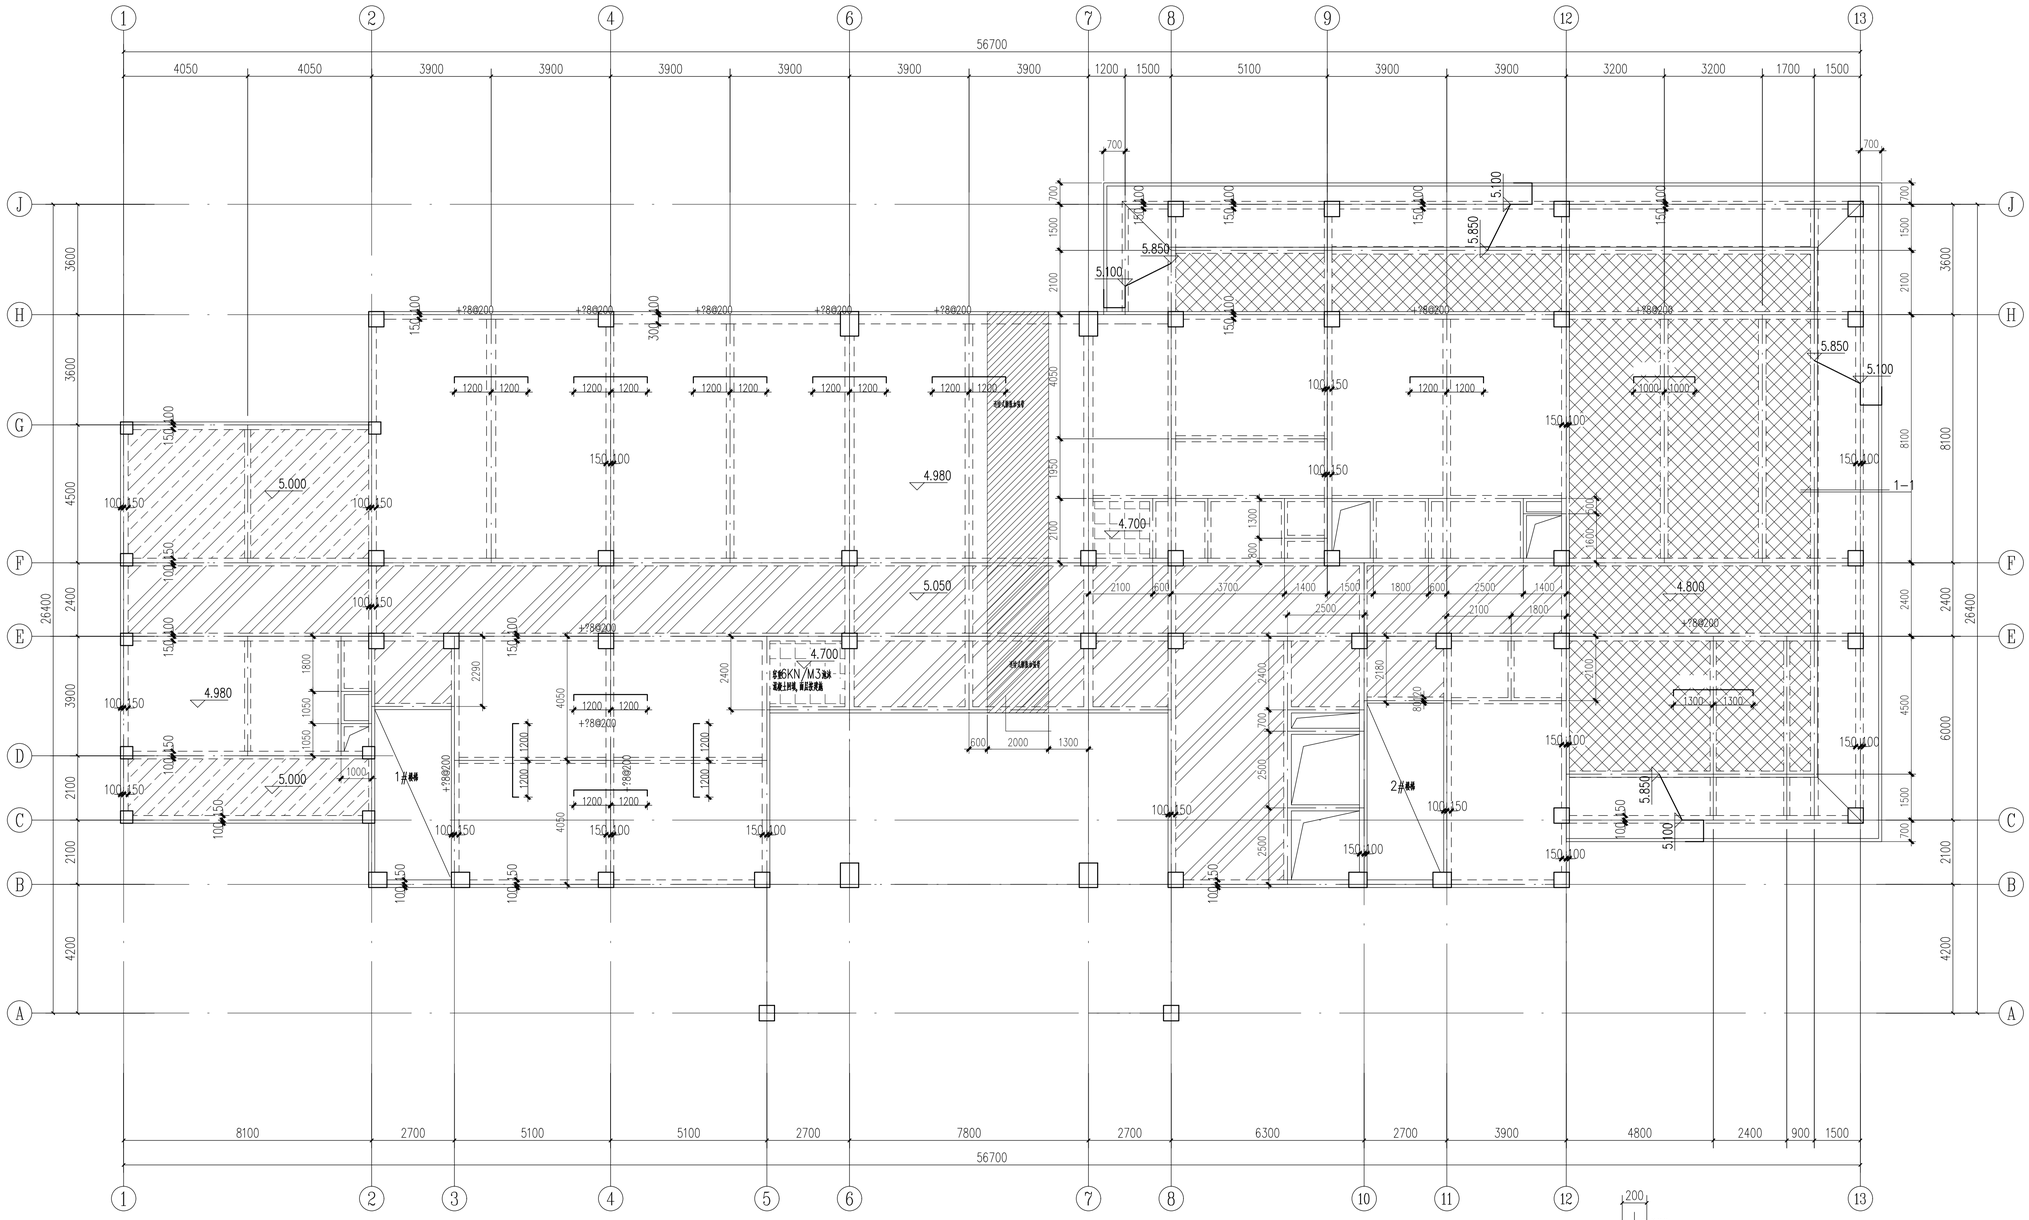


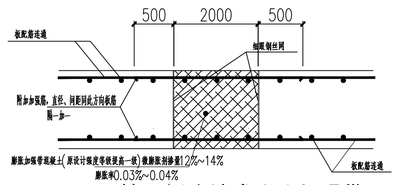
楼面板连续式膨胀加强带

二层(4.980)结构布置平面图 1:100

1. 现浇板(除注明)板厚为h=120mm,楼面板顶标高4.980(除注明外)
2. 未注明板配筋为?10@200双层双向布置,图示带"十"为本跨板面附加筋.
3. 排水沟穿梁应结合水施预埋套管,避免后凿
   排水沟按局部降板做法参16G101-1,P108.(穿梁预埋套管)

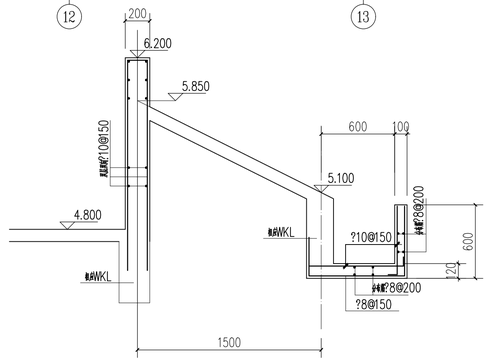


1-1

备注栏

设计单位

杭州园林设计院股份有限公司
HANGZHOU LANDSCAPE ARCHITECTURE DESIGN INSTITUTE CO.,LTD
建筑、风景园林甲级:A133013139
规划乙级:城规编(142056)
市政乙级:A233013136
文物保护工程勘察设计乙级:0102S200002
公司地址:杭州市西湖区双龙街369号西城世纪中心2号楼9楼
电话:0571-87031011 传真:0571-87031002 网址:www.hzyly.com

建设单位 江苏茂源电气有限公司

| | |
|---|---|
| 工程总称 | 云创中心生产综合楼 |
| 子项名称 | 生产综合楼 |
| 图纸名称 | 二层结构布置平面图 |

| | 姓 名 | 签 名 |
|---|---|---|
| 审 定 | 张水龙 | |
| 审 核 | 郑 文 | |
| 项目负责人 | 朱 君 | |
| 专业负责人 | 高 欣 | |
| 设 计 | 高 欣 | |
| 制 图 | 高 欣 | |
| 校 对 | 罗孝敏 | |

执业专用章

按规定加盖


出图章


未盖出图专用章无效

| | | | |
|---|---|---|---|
| 工号 | 25-14 | 图别 | 结施 |
| 图号 | 13 | 修改版次 | |
| 日期 | 2025.12 | | |

专业会签栏

| | |
|---|---|
| 园林 | |
| 建筑 | 张水龙 |
| 结构 | |
| 给排水 | 高欣 |
| 电气 | 郑文 |
| 暖通 | 朱君 |
| 器电 | 罗孝敏 |

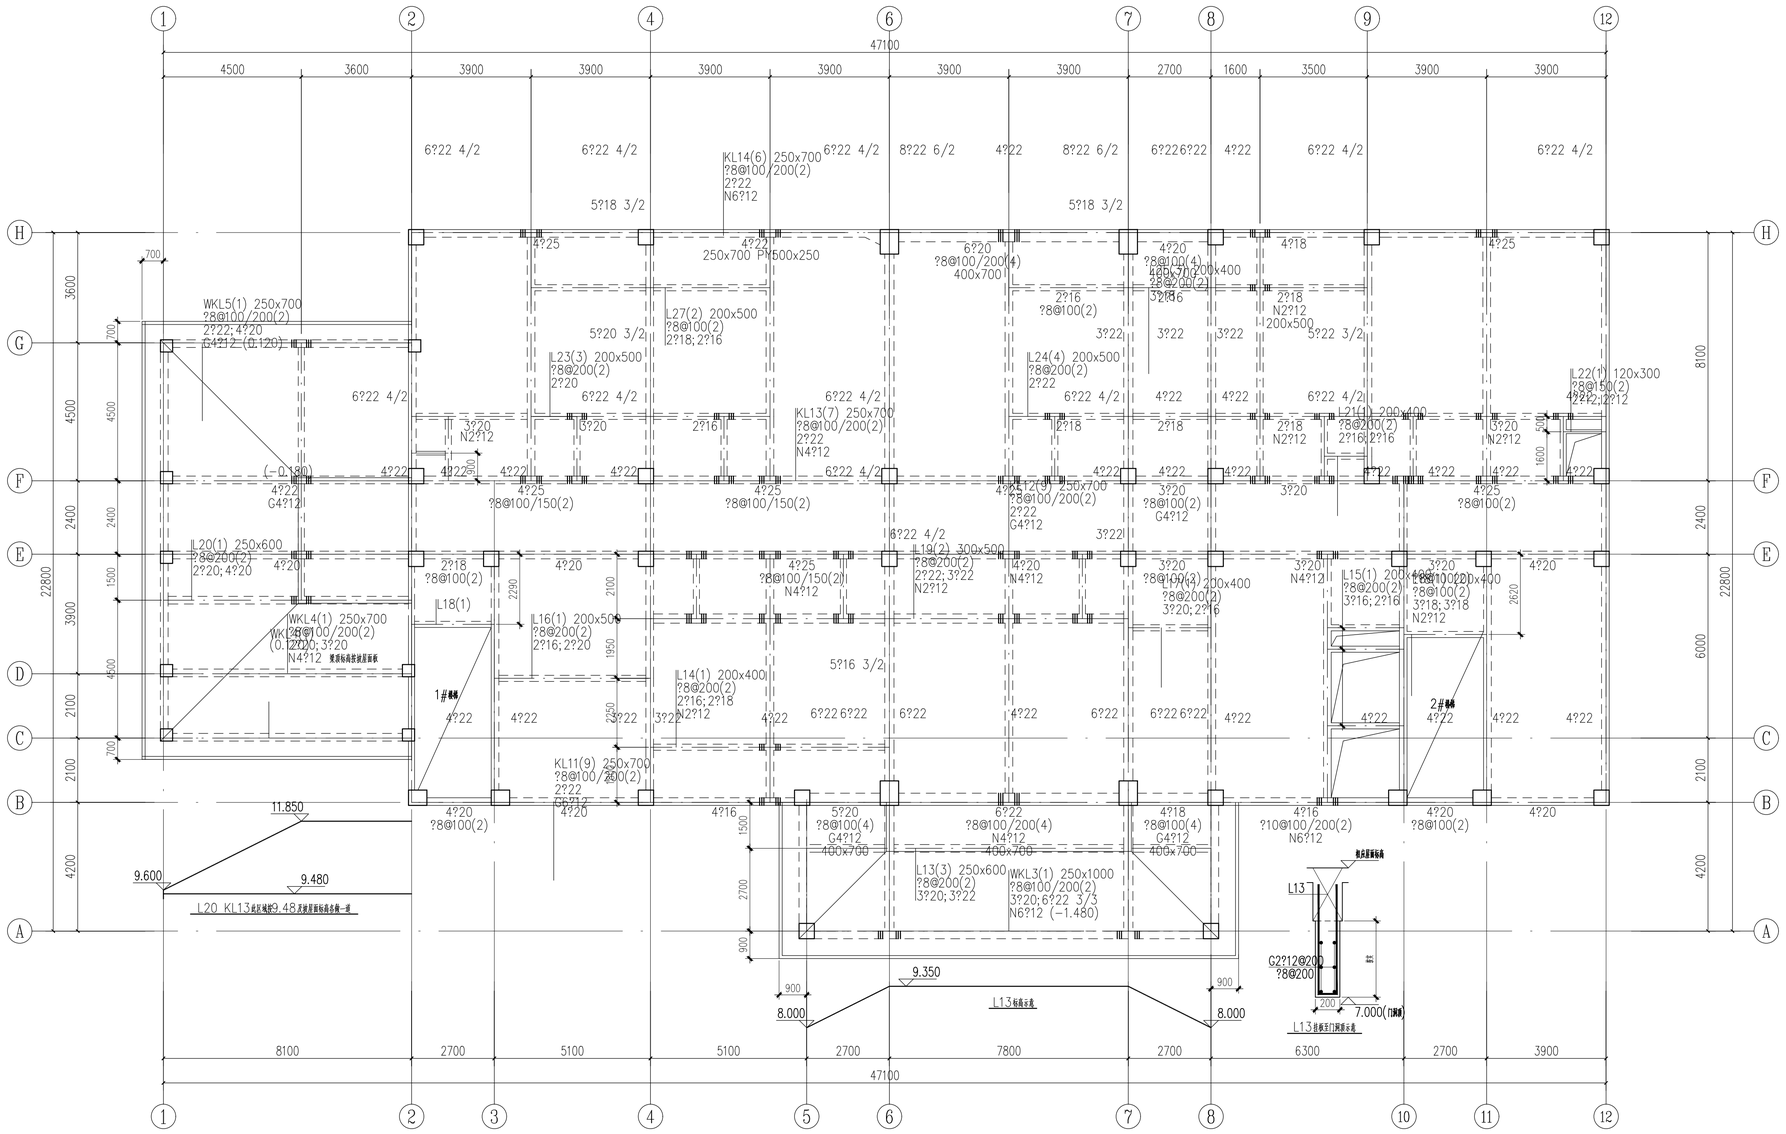
1
2
4
6
7
8
9
12
47100
4500
3600
3900
3900
3900
3900
3900
3900
2700
1600
3500
3900
3900
H
G
F
E
D
C
B
A
3600
4500
2400
1500
2100
2100
4200
22800
3900
4500
2100
2100
4200
8100
2400
6000
2100
2100
4200
22800
KL14(6) 250x700
?8@100/200(2)
2?22
N6?12
WKL5(1) 250x700
?8@100/200(2)
2?22;4?20
G4?12 (0.120)
L27(2) 200x500
?8@100(2)
2?18;2?16
L23(3) 200x500
?8@200(2)
2?20
L24(4) 200x500
?8@200(2)
2?22
L22(1) 120x300
?8@150(2)
2?12;2?12
KL13(7) 250x700
?8@100/200(2)
2?22
N4?12
L21(1) 200x400
?8@200(2)
2?16;2?16
L20(1) 250x600
?8@200(2)
2?20;4?20
L18(1)
L19(2) 300x500
?8@200(2)
2?22;3?22
N2?12
L17(1) 200x400
?8@200(2)
3?20;2?16
L15(1) 200x400
?8@200(2)
3?16;2?16
?8@100(2)
3?18;3?18
N2?12
WKL4(1) 250x700
WK?8@100/200(2)
(0.120)
2?20;3?20
N4?12
L16(1) 200x500
?8@200(2)
2?16;2?20
L14(1) 200x400
?8@200(2)
2?16;2?18
N2?12
KL11(9) 250x700
?8@100/200(2)
2?22
G6?12
KL12(9) 250x700
?8@100/200(2)
2?22
G4?12
L13(3) 250x600
?8@200(2)
3?20;3?22
WKL3(1) 250x1000
?8@100/200(2)
3?20;6?22 3/3
N6?12 (-1.480)
L13
G2?12@200
?8@200
L13板面标高
L13挑板至门洞顶标高
L20 KL13处标高9.48,其余屋面标高参照一层
11.850
9.600
9.480
9.350
8.000
8.000
7.000(门洞顶)
1#楼梯
2#楼梯
5?18 3/2
6?22 4/2
8?22 6/2
6?22 6?22
4?22
5?16 3/2
5?20 3/2
3?22
3?20
4?25
?8@100/150(2)
4?20
?8@100(2)
5?20
?8@100(4)
G4?12
400x700
6?20
?8@100/200(4)
400x700
4?18
4?16
?10@100/200(2)
N6?12
2?16
?8@100(2)
2?18
N2?12
200x500
3?16
3?20
N2?12
G?20
2?16
2?18
N4?12
4?25
?8@100(2)
(-0.180)
4?22
G4?12
?8@100(2)
2?18
?8@100(2)
5?16
6?22 6?22
5?20
?8@100(4)
G4?12
400x700
6?22
?8@100/200(4)
N4?12
400x700
4?18
?8@100(4)
G4?12
400x700
4?16
?10@100/200(2)
N6?12
4?20
?8@100(2)
4?20
4?20
4?20

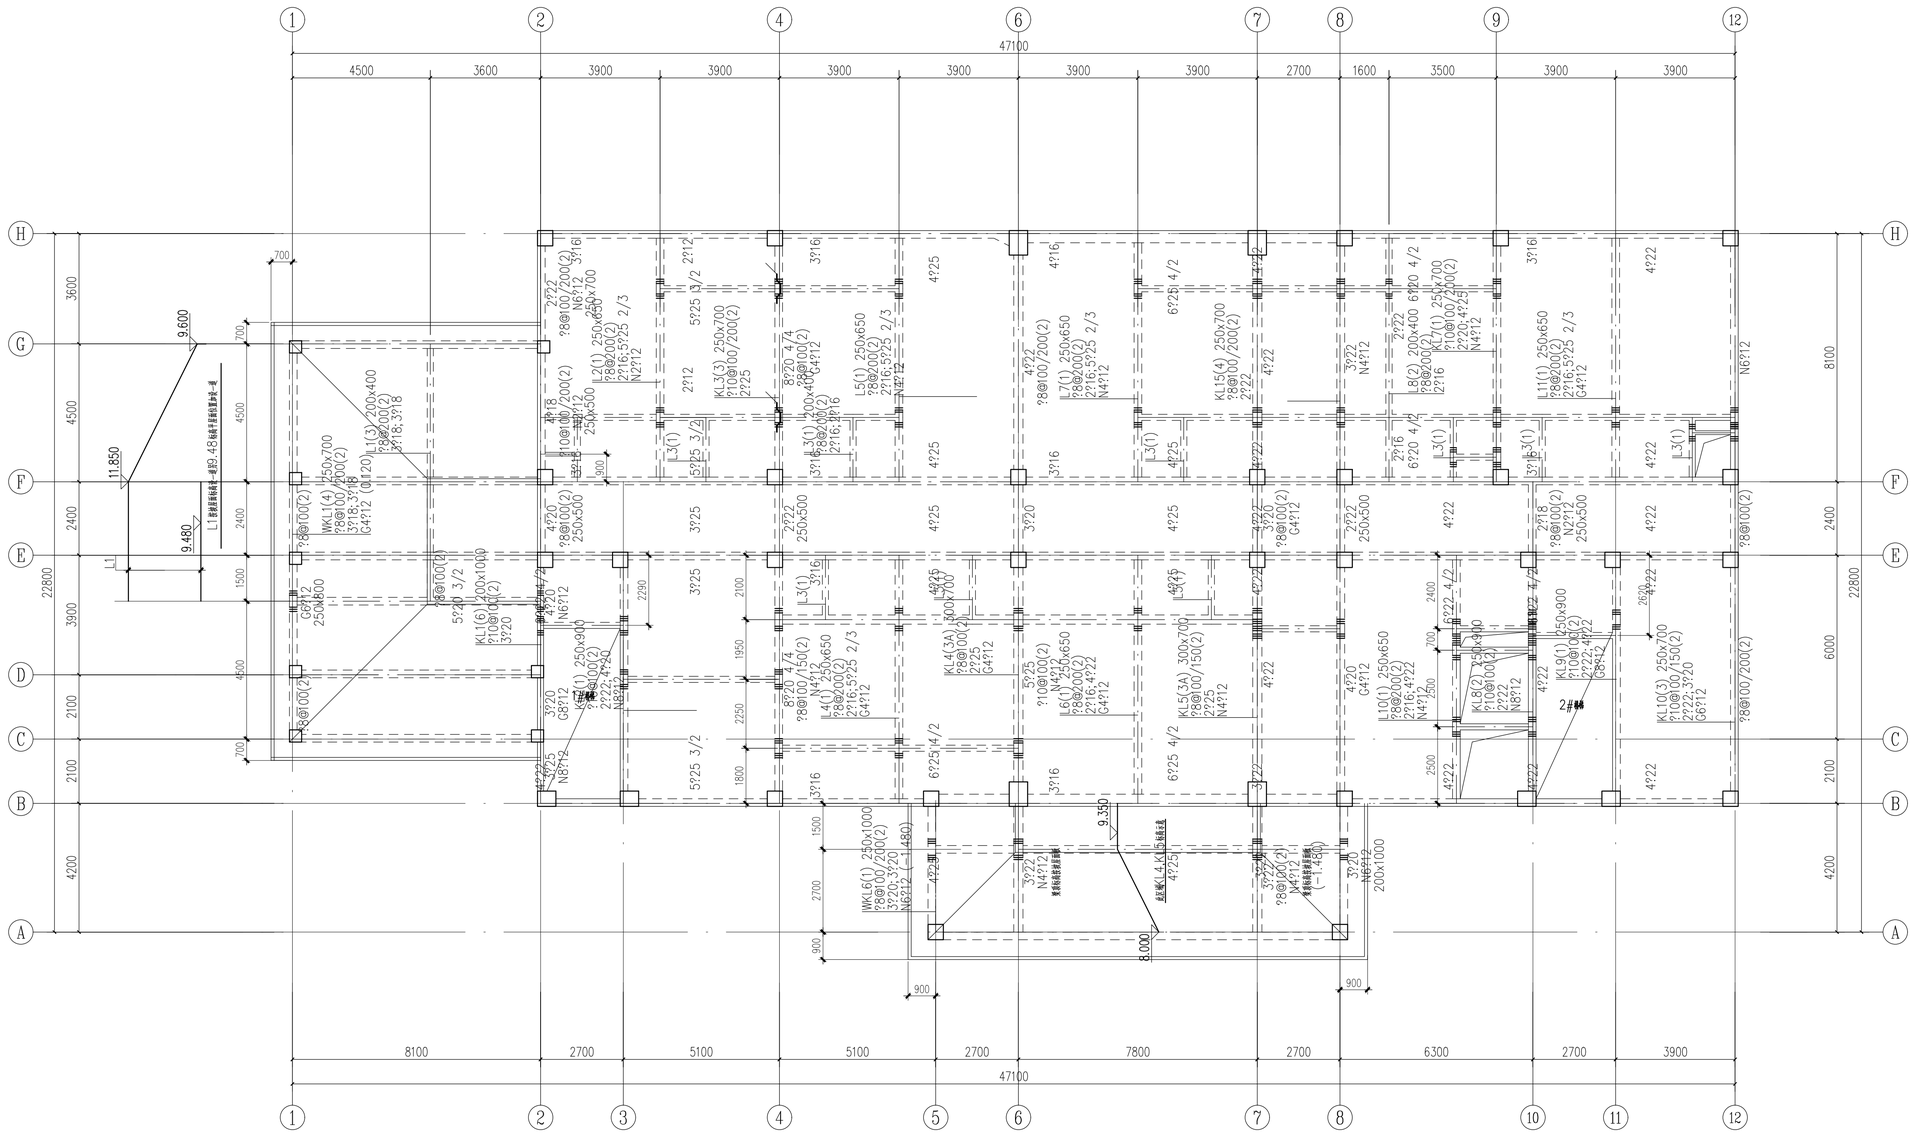


## 三层(9.480)梁配筋平面图2 1:100

1. 本层梁基准标高(除注明外)为9.480，梁标注括号中数字为相对基准标高的高差值
2. 主次梁箍筋加密方相应主梁箍筋每边加密3道@50。
3. 水管穿梁应结合水施预埋套管，避免后凿

备注栏

设计单位

杭州园林设计院股份有限公司
HANGZHOU LANDSCAPE ARCHITECTURE DESIGN INSTITUTE CO.,LTD

建筑、风景园林甲级:A133013139
规划乙级:城规编（142056）
市政乙级:A233013136
文物保护工程勘察设计乙级:0102SJ0002

公司地址：杭州市西湖区双龙街130号西城世纪中心5号楼南楼
电话：0571-87031011　　传真：0571-87031092　　网址：www.hzyly.com

| | |
|---|---|
| 建设单位 | 江苏茂源电气有限公司 |
| 工程总称 | 云创中心生产综合楼 |
| 子项名称 | 生产综合楼 |
| 图纸名称 | 三层梁配筋平面图2 |

| | 姓 名 | 签 名 |
|---|---|---|
| 审 定 | 张永龙 | |
| 审 核 | 郑 文 | |
| 项目负责人 | 朱 君 | |
| 专业负责人 | 高 欣 | |
| 设 计 | 高 欣 | |
| 制 图 | 高 欣 | |
| 校 对 | 罗孝敏 | |

执业专用章

按规定加盖


出图章


未盖出图专用章无效

| | | | |
|---|---|---|---|
| 工号 | 25-14 | 图别 | 结施 |
| 图号 | 15 | 修改版次 | |
| 日期 | 2025.12 | | |

专业会签栏


| | | | | | | | |
|---|---|---|---|---|---|---|---|
| 园林 | | 结构 | | 电气 | | 给排水 | |
| 建筑 | | 给排水 | | 暖通 | | 结构 | |
| | | | | | | 建筑 | |
| | | | | | | 暖通 | |
| | | | | | | 电气 | |
| | | | | | | 园林 | |

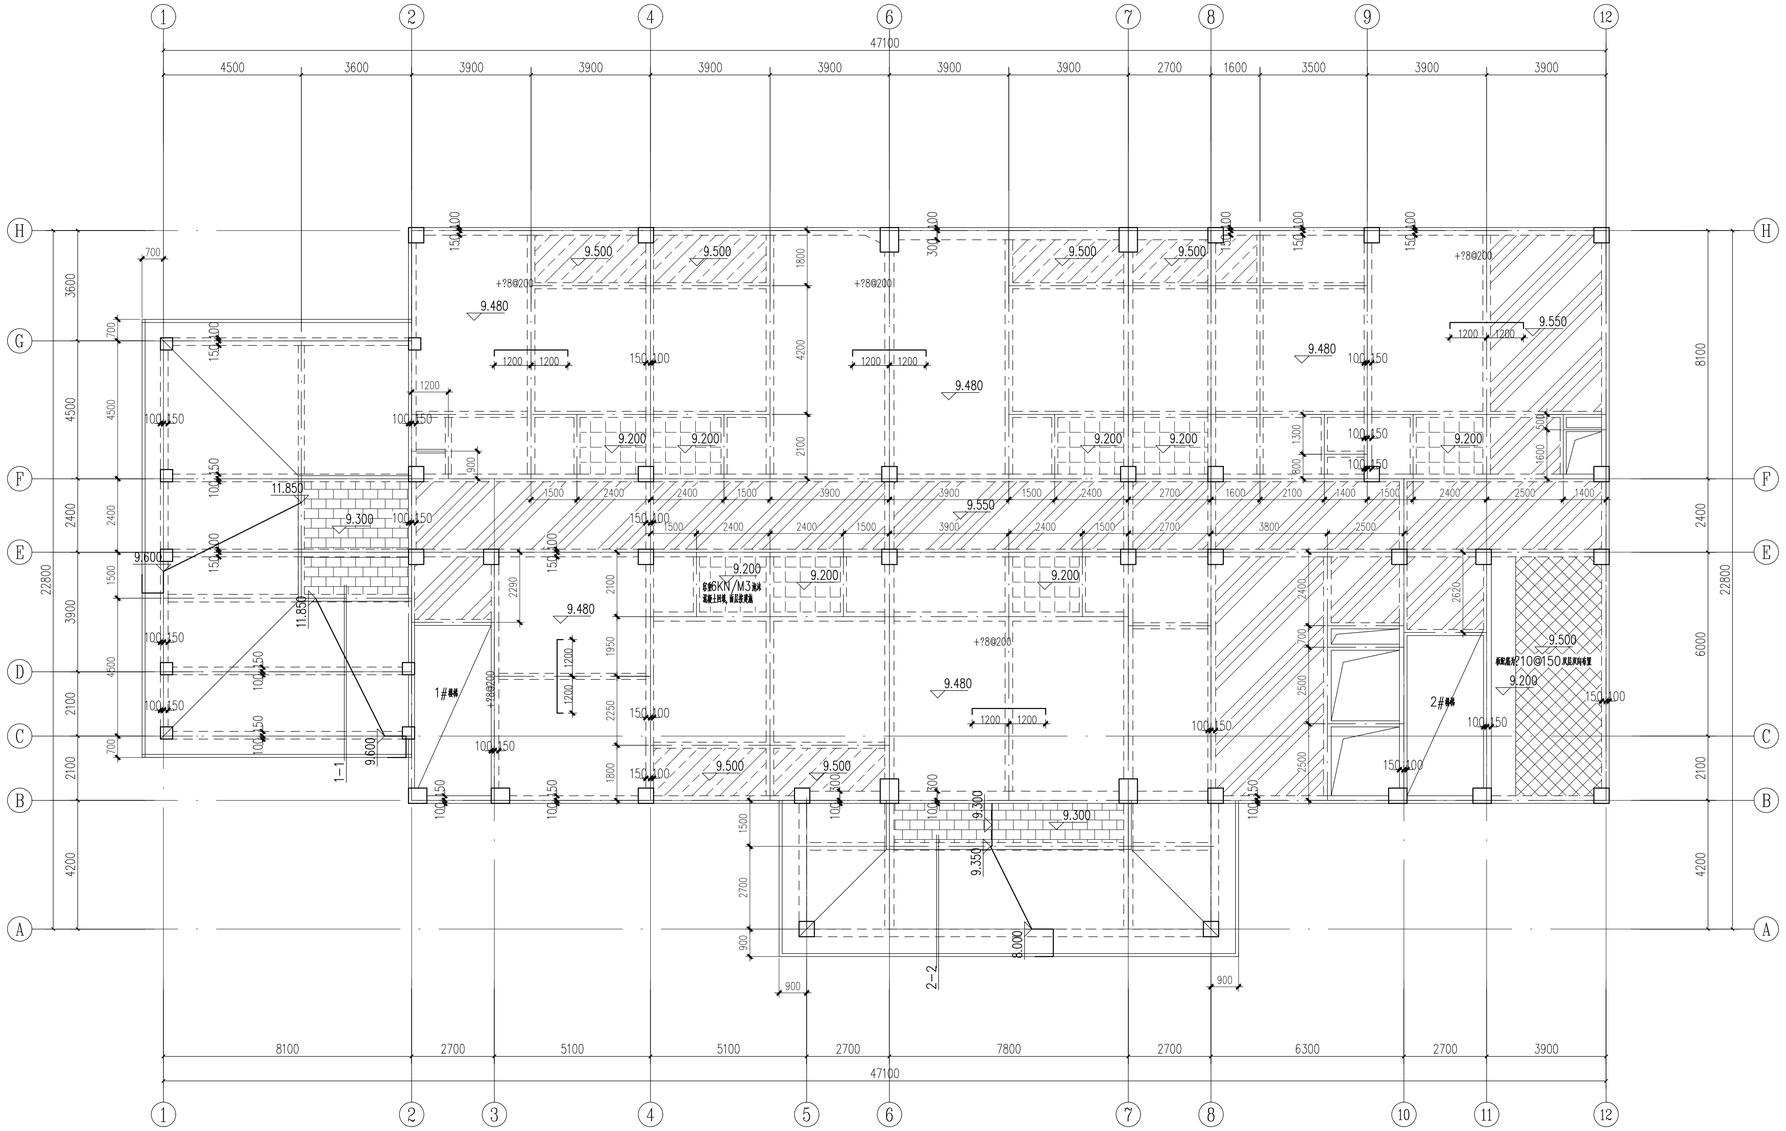

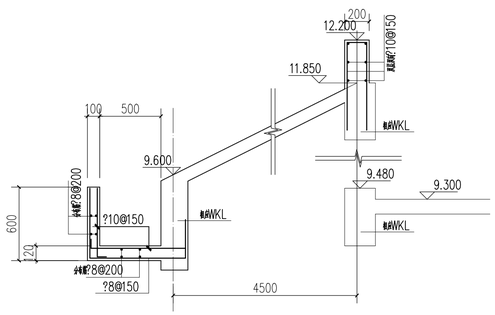
## 三层(9.480)结构布置平面图 1:100

1. 现浇板(除注明)板厚为h=120mm,楼面板面标高9.480(除注明外)
2. 未注明板配筋为?10@200双层双向布置,图示带"+"为本跨板面附加筋.
3. 排水沟穿梁应结合水施预埋套管,避免后凿
   排水沟放后倒坡板做法参1 6G101-1,P108.(穿梁预埋套管)

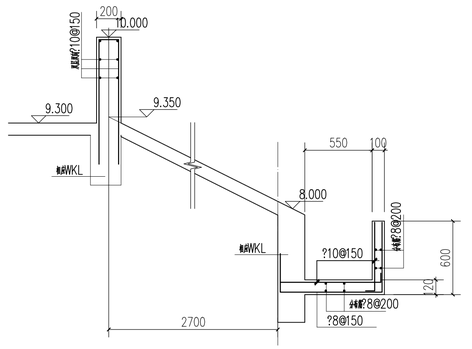


备注栏

设计单位

杭州园林设计院股份有限公司
HANGZHOU LANDSCAPE ARCHITECTURE DESIGN INSTITUTE CO.,LTD
建筑、风景园林甲级:A133013139
规划乙级:城规编(142056)
市政乙级:A233013136
文物保护工程勘察设计乙级:0102SJ0002
公司地址:杭州市西湖区双龙街136号西溪世纪中心5号楼南楼
电话:0571-87631011 传真:0571-87631082 网址:www.hzyly.com

建设单位 江苏茂源电气有限公司

| | |
|---|---|
| 工程总称 | 云创中心生产综合楼 |
| 子项名称 | 生产综合楼 |
| 图纸名称 | 三层结构布置平面图 |

| | 姓 名 | 签 名 |
|---|---|---|
| 审 定 | 张永龙 | |
| 审 核 | 郑 文 | |
| 项目负责人 | 朱 君 | |
| 专业负责人 | 高 欣 | |
| 设 计 | 高 欣 | |
| 制 图 | 高 欣 | |
| 校 对 | 罗孝敏 | |

执业专用章

按规定加盖


出图章

未盖出图专用章无效

| | | | |
|---|---|---|---|
| 工号 | 25-14 | 图别 | 结施 |
| 图号 | 16 | 修改版次 | |
| 日期 | 2025.12 | | |

专业会签栏

| | |
|---|---|
| 园林 | 建筑 |
| | 幼城 |
| 结构 | 给排水 |
| 电气 | 暖通 |
| 器电 | |

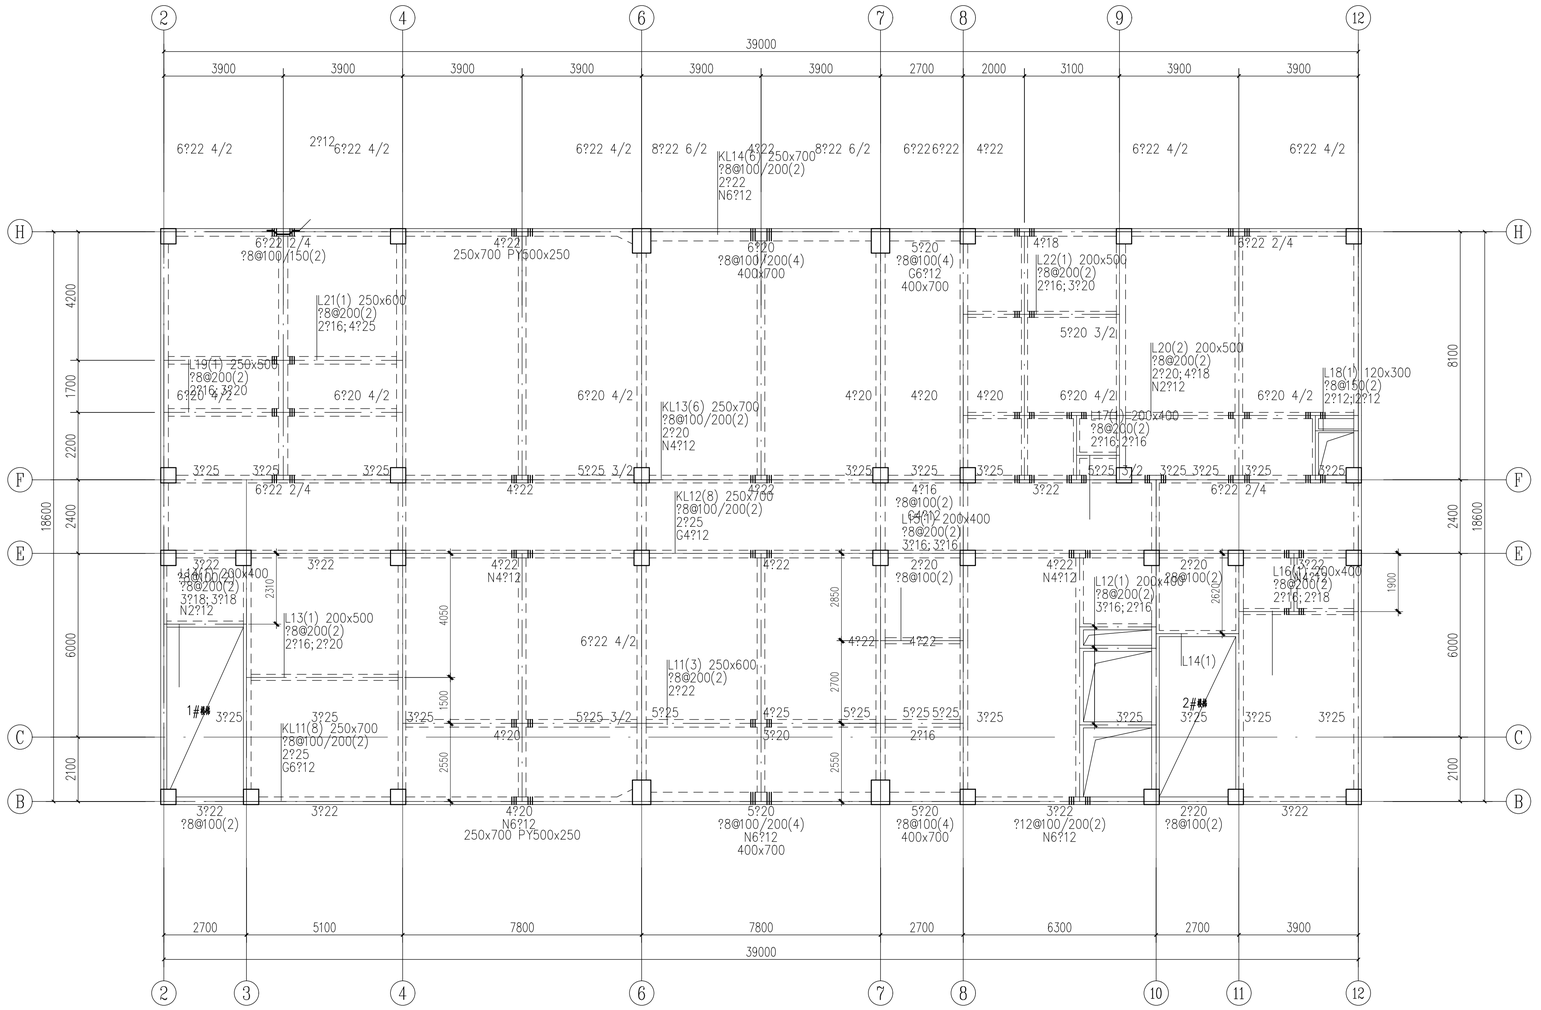


## 四层(13.980)梁配筋平面图1 1:100

1. 本层梁基准标高(除注明外)为13.980，梁标注括号中数字为相对基准标高的高差值
2. 主次梁重箍加密为相应主梁箍筋每边加密3道@50。
3. 水管穿梁应结合水施预埋套管，避免后凿

备注栏

设计单位

杭州园林设计院股份有限公司
HANGZHOU LANDSCAPE ARCHITECTURE DESIGN INSTITUTE CO.,LTD
建筑、风景园林甲级:A133013139
规划乙级:城规编（1620056）
市政乙级:A233013136
文物保护工程勘察设计乙级:0102SJ0002
公司地址：杭州市西湖区双龙街138号西湖世纪中心5号楼南楼
电话：0571-87031011　　传真：0571-87031002　　网址：www.hzyly.com

建设单位 江苏茂源电气有限公司

| | |
|---|---|
| 工程总称 | 云创中心生产综合楼 |
| 子项名称 | 生产综合楼 |
| 图纸名称 | 四层梁配筋平面图1 |

| | 姓 名 | 签 名 |
|---|---|---|
| 审 定 | 张永龙 | |
| 审 核 | 郑 文 | |
| 项目负责人 | 朱 君 | |
| 专业负责人 | 高 欣 | |
| 设 计 | 高 欣 | |
| 制 图 | 高 欣 | |
| 校 对 | 罗孝敏 | |

执业专用章


按规定加盖

出图章

未盖出图专用章无效

| | | | |
|---|---|---|---|
| 工号 | 25-14 | 图别 | 结施 |
| 图号 | 17 | 修改版次 | |
| 日期 | 2025.12 | | |

专业会签栏：园林 建筑 | 结构 | 给排水 | 电气 暖通 | 器电

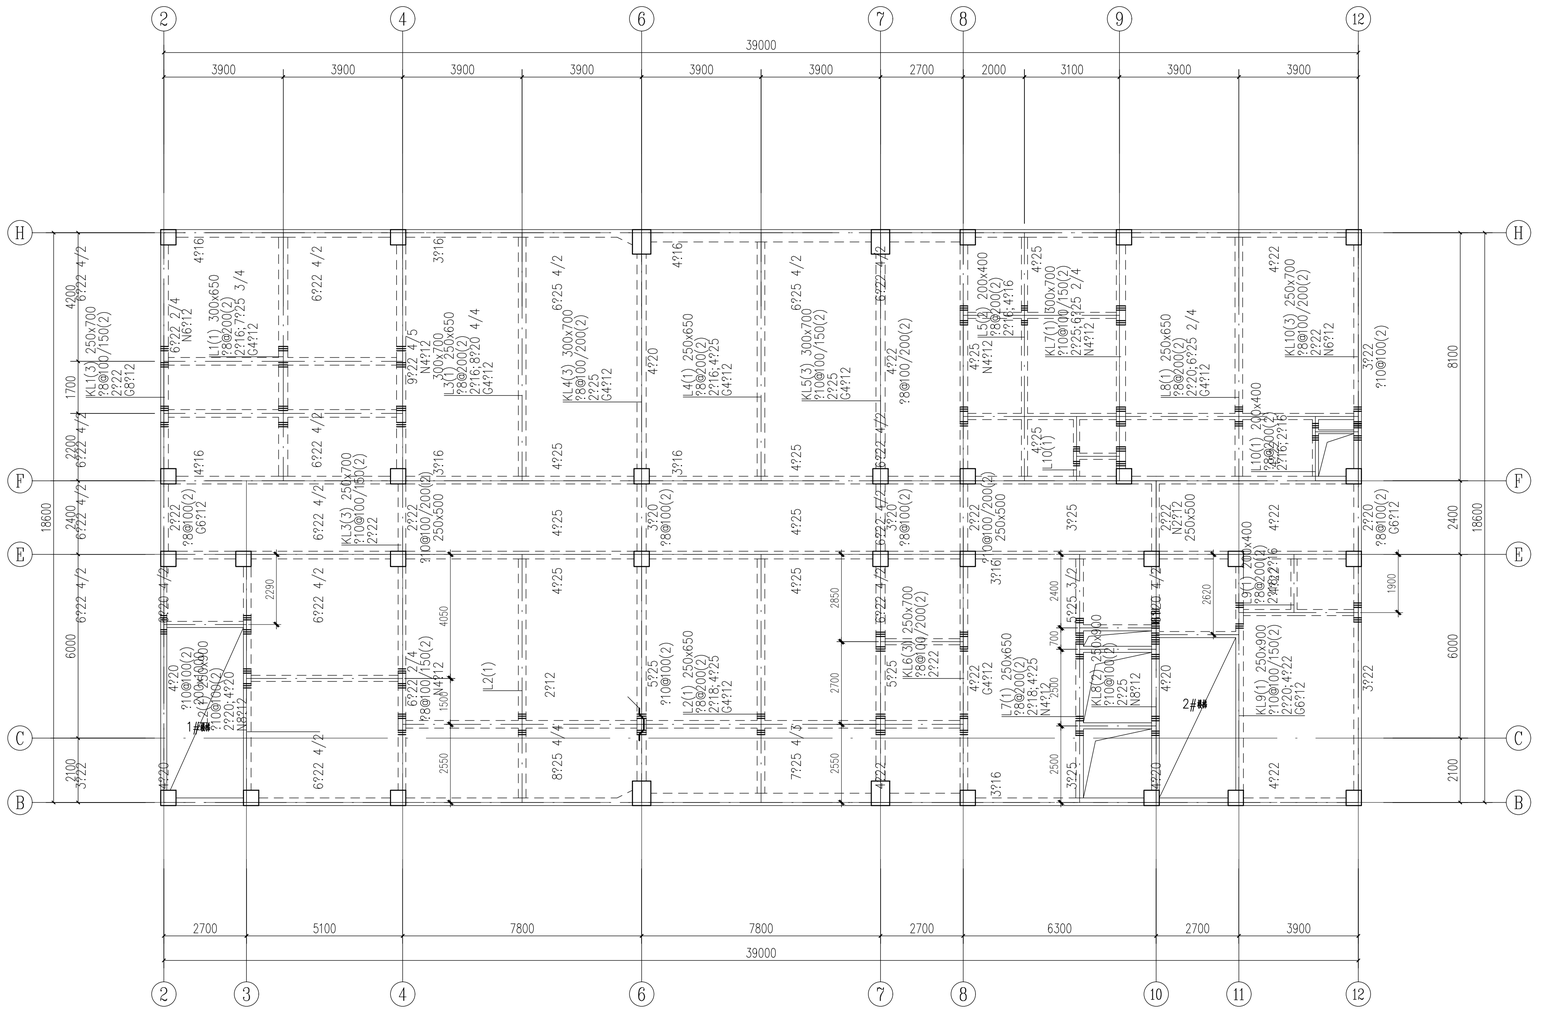


## 四层(13.980)梁配筋平面图2 1:100

1. 本层梁基准标高(除注明外)为13.980，梁标注括号中数字为相对基准标高的高差值
2. 主次梁集箍加密为相应主梁箍筋每边加密3道@50。
3. 水管穿梁应结合水施预埋套管，避免后凿

备注栏

设计单位

杭州园林设计院股份有限公司
HANGZHOU LANDSCAPE ARCHITECTURE DESIGN INSTITUTE CO.,LTD
建筑、风景园林甲级:A133013139
规划乙级:城规编（142056）
市政乙级:A233013136
文物保护工程勘察设计乙级:0102SJ0002
公司地址：杭州市西湖区双龙街38号西湖世纪中心2号楼南楼
电话：0571-87031011 传真：0571-87031002 网址：www.hzylc.com

建设单位 江苏茂源电气有限公司

工程总称 云创中心生产综合楼

子项名称 生产综合楼

图纸名称 四层梁配筋平面图2

| | 姓 名 | 签 名 |
|---|---|---|
| 审 定 | 张水龙 | |
| 审 核 | 郑 文 | |
| 项目负责人 | 朱 君 | |
| 专业负责人 | 高 欣 | |
| 设 计 | 高 欣 | |
| 制 图 | 高 欣 | |
| 校 对 | 罗孝敏 | |

执业专用章

按规定加盖


出图章

未盖出图专用章无效

| 工号 | 25-14 | 图别 | 结施 |
|---|---|---|---|
| 图号 | 18 | 修改版次 | |
| 日期 | 2025.12 | | |

专业会签栏

| 园林 | | 结构 | | 电气 | | 器电 | |
|---|---|---|---|---|---|---|---|
| 建筑 | | 给排水 | | 暖通 | | | |

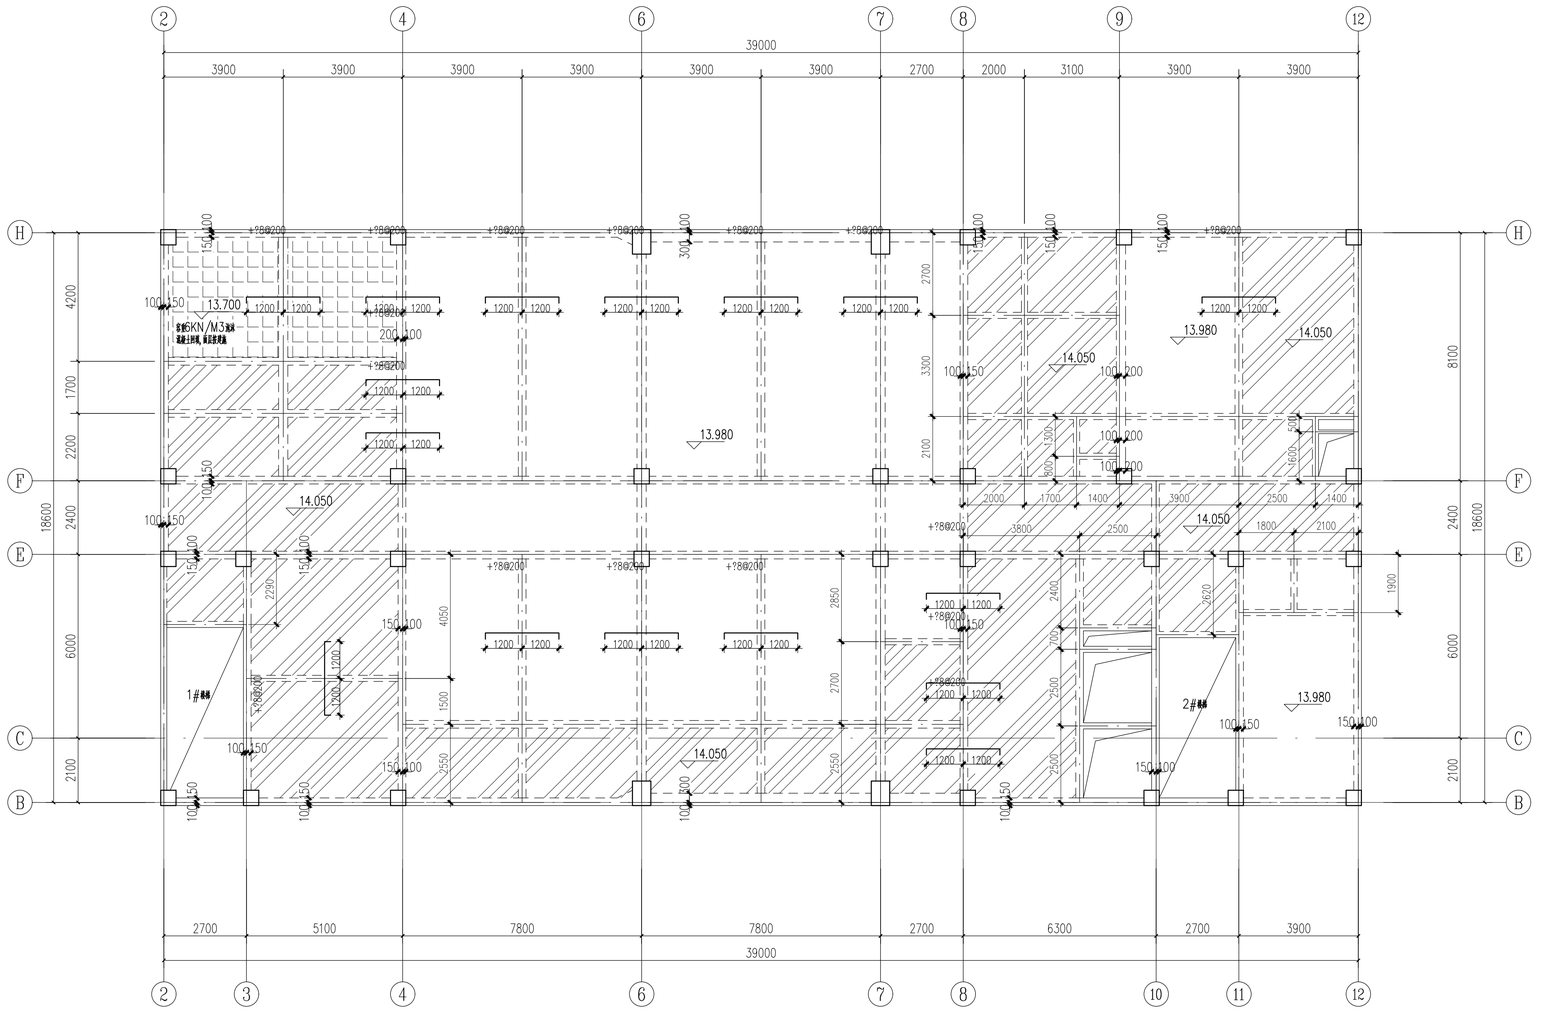


## 四层(13.980)结构布置平面图 1:100

1. 现浇板(除注明)板厚为h=120mm,板顶标高13.980(除注明外)
2. 未注明板配筋为?10@200双层双向布置,图示带"十"为本跨板面附加筋.
3. 排水沟穿梁应结合水施预埋套管,避免后凿
   排水沟放局部降板做法参16G101-1,P108.(穿梁预埋套管)

备注栏

设计单位

杭州园林设计院股份有限公司
HANGZHOU LANDSCAPE ARCHITECTURE DESIGN INSTITUTE CO.,LTD
建筑、风景园林甲级:A133013139
规划乙级:城规编(142056)
市政乙级:A233013136
文物保护工程勘察设计乙级:0102SJ0002
公司地址:杭州市西湖区双龙街138号西溪世纪中心5号楼南楼
电话:0571-87051011 传真:0571-87051082 网址:www.hzyly.com

建设单位 江苏茂源电气有限公司

| | |
|---|---|
| 工程总称 | 云创中心生产综合楼 |
| 子项名称 | 生产综合楼 |
| 图纸名称 | 四层结构布置平面图 |

| | 姓 名 | 签 名 |
|---|---|---|
| 审 定 | 张永龙 | |
| 审 核 | 郑 文 | |
| 项目负责人 | 朱 君 | |
| 专业负责人 | 高 欣 | |
| 设 计 | 高 欣 | |
| 制 图 | 高 欣 | |
| 校 对 | 罗孝敏 | |

执业专用章

按规定加盖


出图章

未盖出图专用章无效

| | | | |
|---|---|---|---|
| 工号 | 25-14 | 图别 | 结施 |
| 图号 | 19 | 修改版次 | |
| 日期 | 2025.12 | | |

专业会签栏

| | |
|---|---|
| 园林 | |
| 建筑 | 结构 |
| 给排水 | 电气 |
| 暖通 | 弱电 |

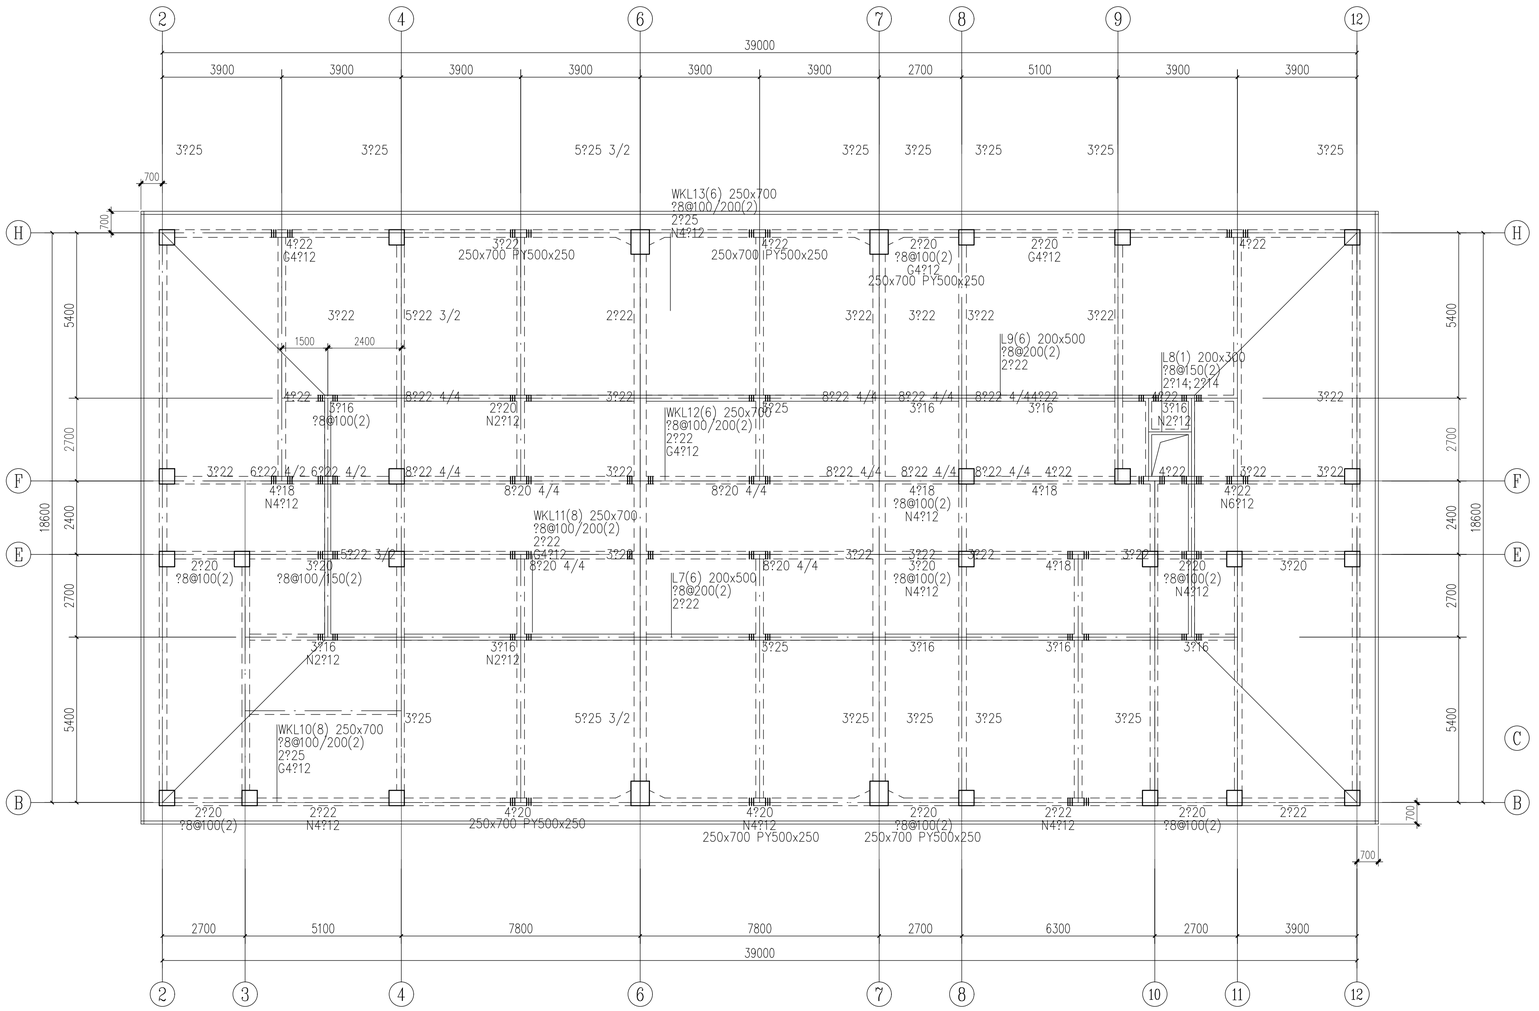


## 屋面梁配筋平面图1 1:100

1. 本层屋面梁为板屋面板标高的折梁
2. 主次梁箍筋加密为相应主梁箍筋每边加密3道@50。
3. 水管穿梁应结合水施预埋套管，避免后凿

备注栏

设计单位

杭州园林设计院股份有限公司
HANGZHOU LANDSCAPE ARCHITECTURE DESIGN INSTITUTE CO.,LTD
建筑、风景园林甲级:A133013139
规划乙级:城规编（142056）
市政乙级:A233013136
文物保护工程勘察设计乙级:0102SJ00002
公司地址：杭州市西湖区双龙街38号西城世纪中心2号楼南楼
电话：0571-87031011 传真：0571-87031002 网址：www.hzyly.com

建设单位 江苏茂源电气有限公司

| | |
|---|---|
| 工程总称 | 云创中心生产综合楼 |
| 子项名称 | 生产综合楼 |
| 图纸名称 | 屋面梁配筋平面图1 |

| | 姓 名 | 签 名 |
|---|---|---|
| 审 定 | 张永龙 | |
| 审 核 | 郑 文 | |
| 项目负责人 | 朱 君 | |
| 专业负责人 | 高 欣 | |
| 设 计 | 高 欣 | |
| 制 图 | 高 欣 | |
| 校 对 | 罗孝敏 | |

执业专用章


按规定加盖

出图章

未盖出图专用章无效

| | | | |
|---|---|---|---|
| 工号 | 25-14 | 图别 | 结施 |
| 图号 | 20 | 修改版次 | |
| 日期 | 2025.12 | | |

专业会签栏：园林 建筑；结构 给排水；电气 暖通；器电

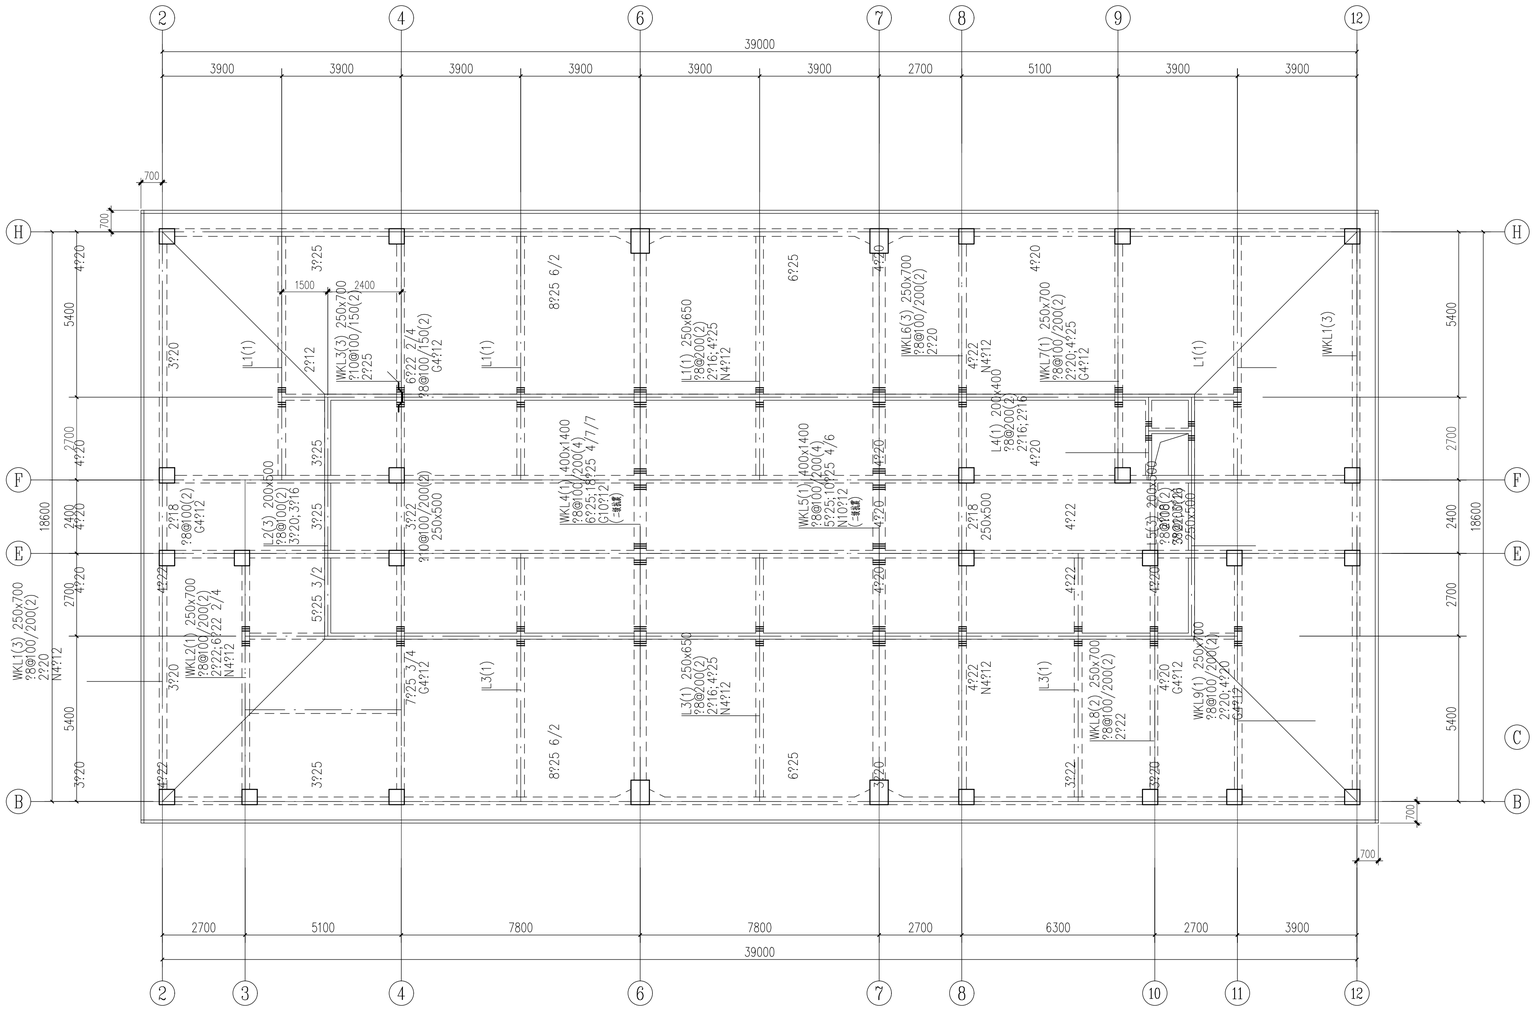


## 屋面梁配筋平面图2 1:100

1. 本层屋面梁为按屋面板标高均折梁
2. 主次梁覆盖加密为相应主梁覆盖每边加设3道@50。
3. 水管穿梁应结合水施预埋套管，避免后凿

备注栏

设计单位

杭州园林设计院股份有限公司
HANGZHOU LANDSCAPE ARCHITECTURE DESIGN INSTITUTE CO.,LTD

建筑、风景园林甲级:A133013139
规划乙级:城规编（142056）
市政乙级:A233013136
文物保护工程勘察设计乙级:0102SJ0002

公司地址：杭州市西湖区双龙街136号西溪世纪中心2号楼南楼
电话：0571-87831011　　传真：0571-87831082　　网址：www.hzyls.com

| | |
|---|---|
| 建设单位 | 江苏茂源电气有限公司 |
| 工程总称 | 云创中心生产综合楼 |
| 子项名称 | 生产综合楼 |
| 图纸名称 | 屋面梁配筋平面图2 |

| | 姓 名 | 签 名 |
|---|---|---|
| 审 定 | 张永龙 | |
| 审 核 | 郑 文 | |
| 项目负责人 | 朱 君 | |
| 专业负责人 | 高 欣 | |
| 设 计 | 高 欣 | |
| 制 图 | 高 欣 | |
| 校 对 | 罗孝敏 | |

执业专用章

按规定加盖


出图章


未盖出图专用章无效

| | | | |
|---|---|---|---|
| 工号 | 25-14 | 图别 | 结施 |
| 图号 | 21 | 修改版次 | |
| 日期 | 2025.12 | | |

专业会签栏


| | | | | | | | |
|---|---|---|---|---|---|---|---|
| 园林 | | 结构 | | 电气 | | 弱电 | |
| 建筑 | | 给排水 | | 暖通 | | | |

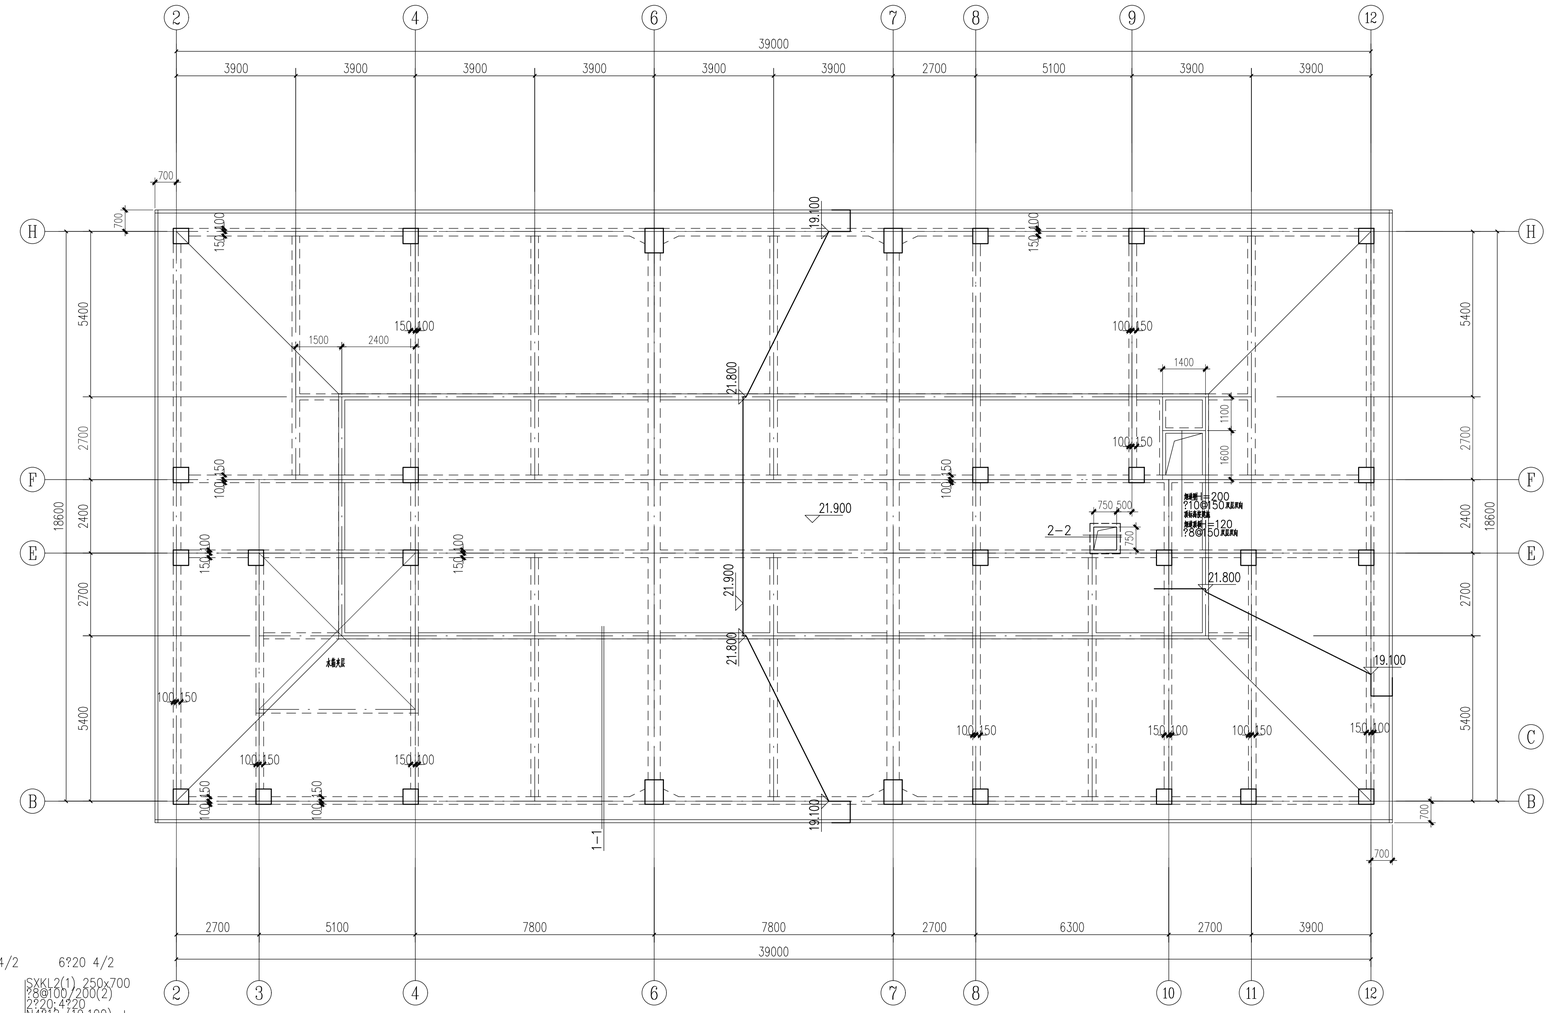

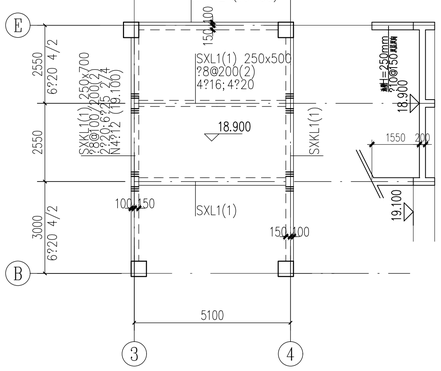
水箱夹层结构平面图 1:100


1. 板厚为h=200mm,板顶标高18.900
2. 水箱底板配筋为?10@150双层双向布置。
3. 未注梁为18.900,梁标注括号中数字为绝对标高

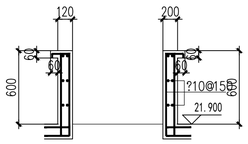


2-2

屋面结构布置平面图 1:100

1. 现浇板(除注明)板厚为h=120mm,
2. 未注明板配筋为?10@150双层双向布置,图示带"+"为本跨板面附加筋
3. 排水沟穿梁点结合水施预埋套管,避免后凿
排水沟按局部降板做法参16G101-1,P108.(穿梁预埋套管)

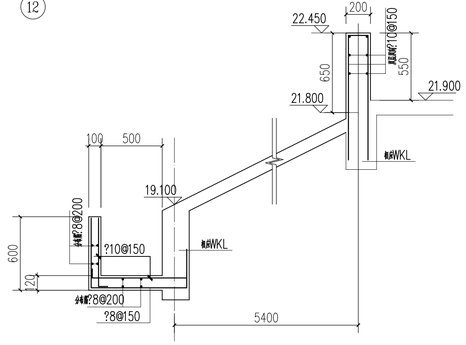


1-1

备注栏

设计单位

杭州园林设计院股份有限公司
HANGZHOU LANDSCAPE ARCHITECTURE DESIGN INSTITUTE CO.,LTD
建筑、风景园林甲级:A133013139
规划乙级:城规编(140056)
市政乙级:A233013136
文物保护工程勘察设计乙级:0102SJ00002
公司地址:杭州市西湖区灵隆街18号西湖创业中心9号楼南楼
电话:0571-87031011 传真:0571-87031002 网址:www.hzyly.com

建设单位 江苏茂源电气有限公司

| | |
|---|---|
| 工程总称 | 云创中心生产综合楼 |
| 子项名称 | 生产综合楼 |
| 图纸名称 | 屋面结构布置平面图 |

| | 姓名 | 签名 |
|---|---|---|
| 审定 | 张永龙 | |
| 审核 | 郑文 | |
| 项目负责人 | 朱君 | |
| 专业负责人 | 高欣 | |
| 设计 | 高欣 | |
| 制图 | 高欣 | |
| 校对 | 罗孝敏 | |

执业专用章

按规定加盖


出图章

未盖出图专用章无效


| | | | |
|---|---|---|---|
| 工号 | 25-14 | 图别 | 结施 |
| 图号 | 22 | 修改版次 | |
| 日期 | 2025.12 | | |

专业会签栏


| | | | |
|---|---|---|---|
| 园林 | 建筑 | 结构 | 给排水 |
| 电气 | 暖通 | 弱电 | |

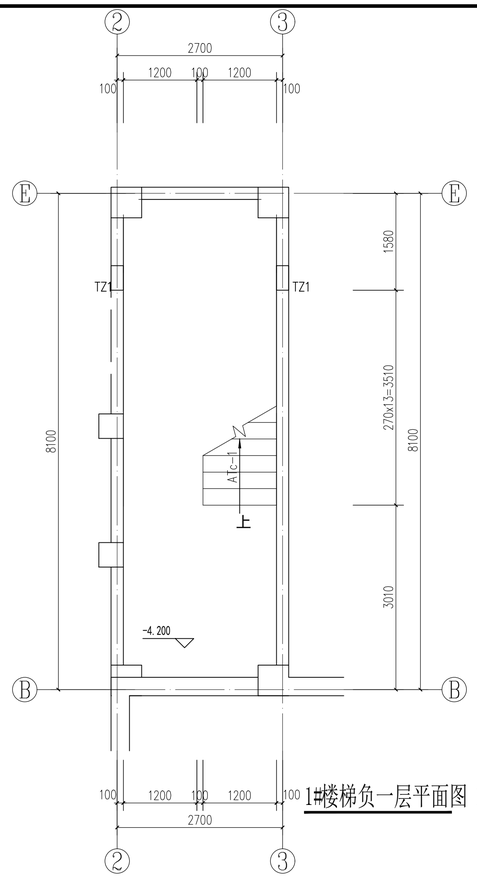



1#楼梯负一层平面图 1:50

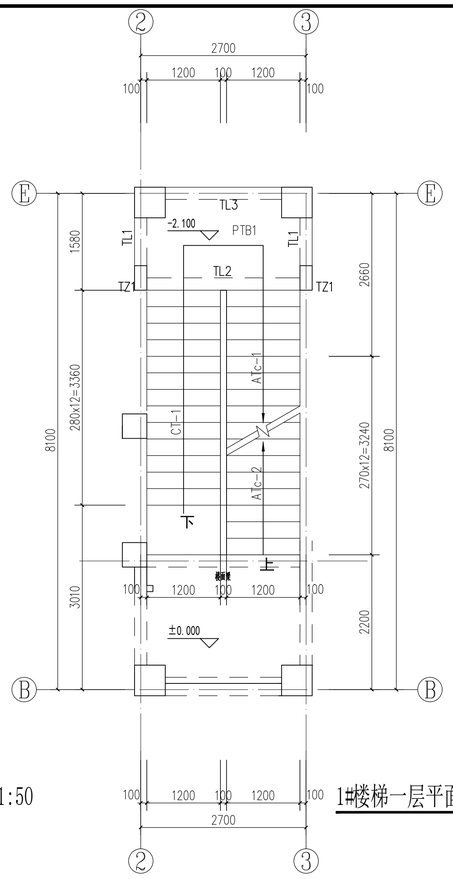



1#楼梯一层平面图 1:50

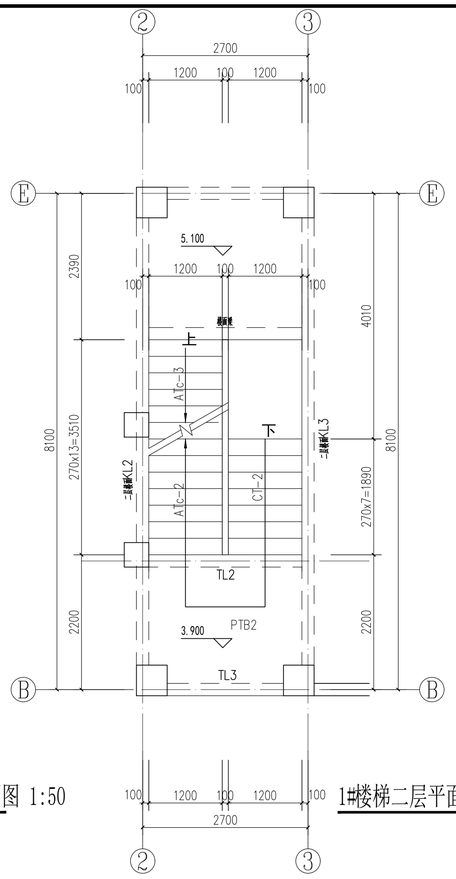



1#楼梯二层平面图 1:50

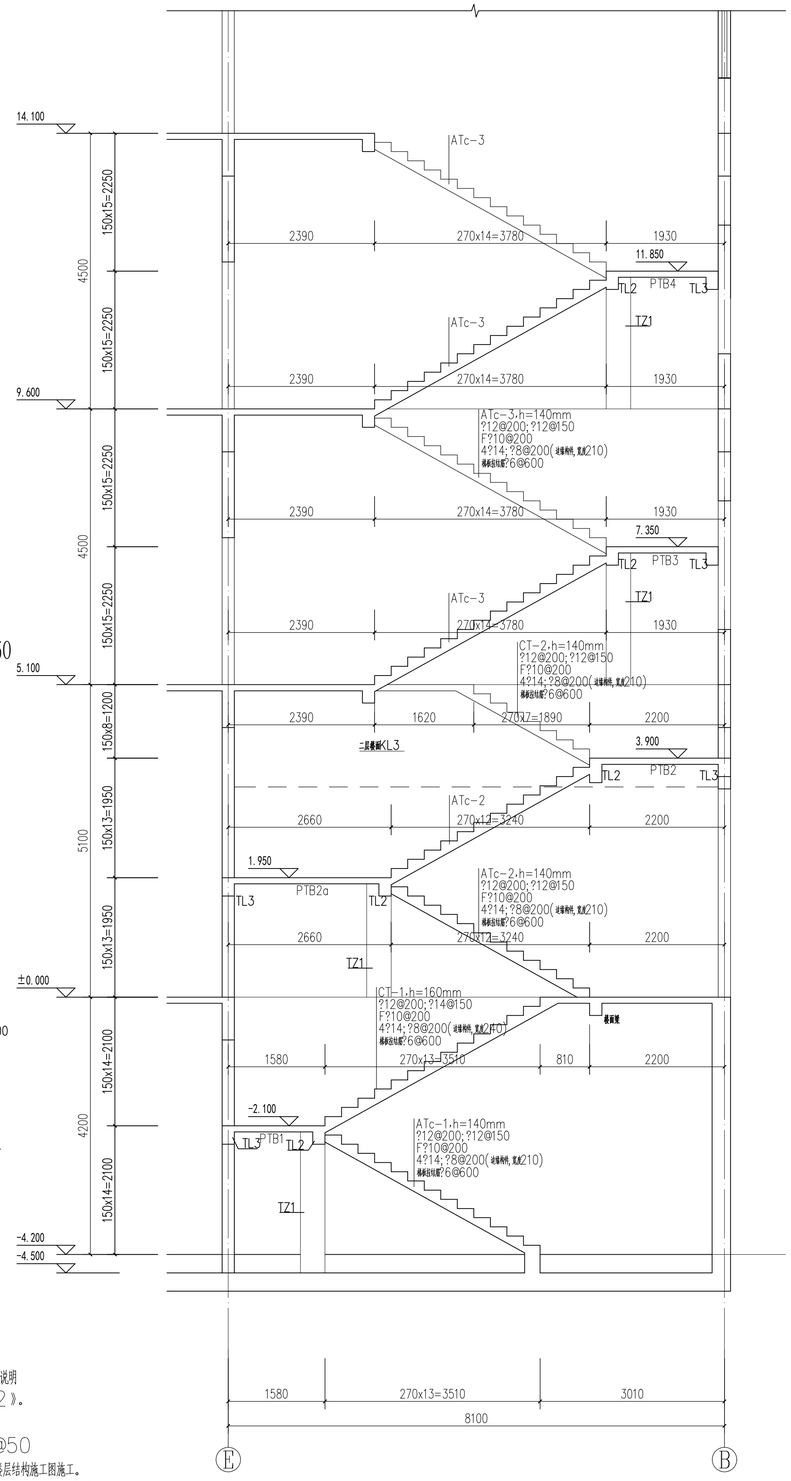



1#楼梯结构剖面图 1:50

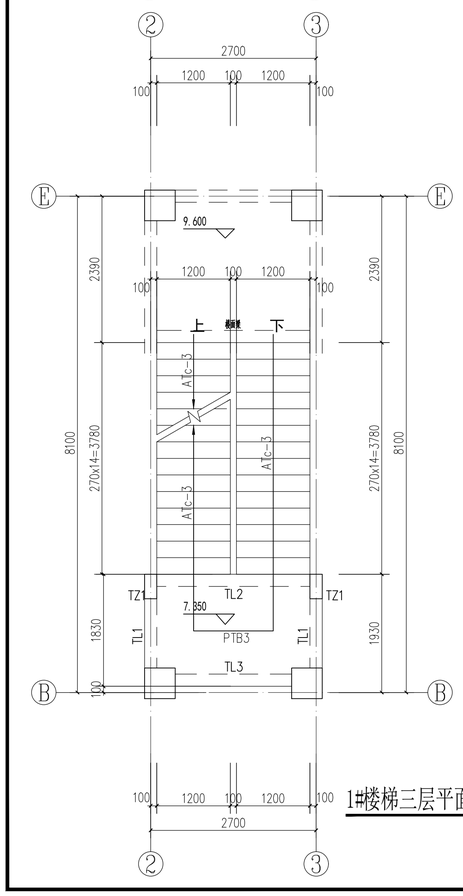



1#楼梯三层平面图 1:50

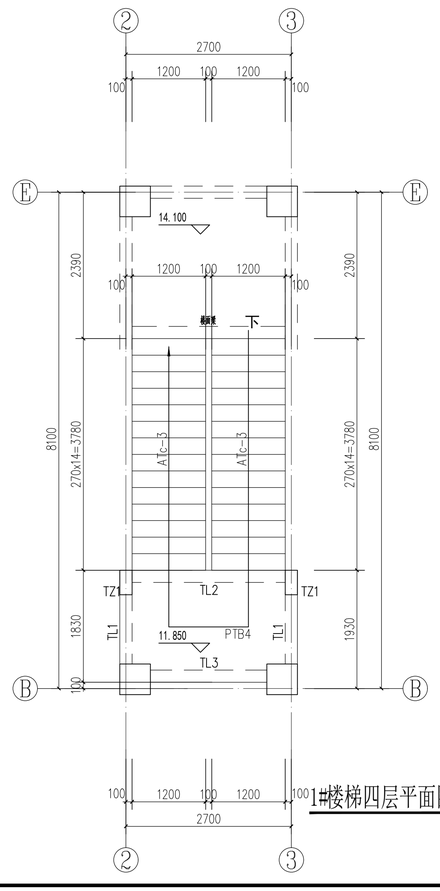


1#楼梯四层平面图 1:50

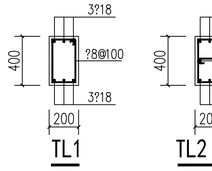


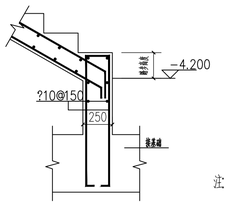

楼梯一层起步构造

注 1. 混凝土楼梯施工图平面表示方法和构造详见设计总说明
和《国家建筑标准设计图集16G101－2》。
2. 楼梯抗震等级同主体。梯板纵筋通长布置。
3. TZ 位置相应架空层KL 箍筋等边加密3 道@50
4. 楼层处楼梯同范围内楼板的板厚和配筋等按相应楼层结构施工图施工。
5. PTBX 板厚均为120mm，配筋均为?10@150 双层双向。
6. 本图所注标高为建筑标高，楼梯结构标高= 相应建筑标高－50mm。
7. 本图必须与建筑施工图配合使用，确认无矛盾后方可用于施工。


| 专业会签栏 | | |

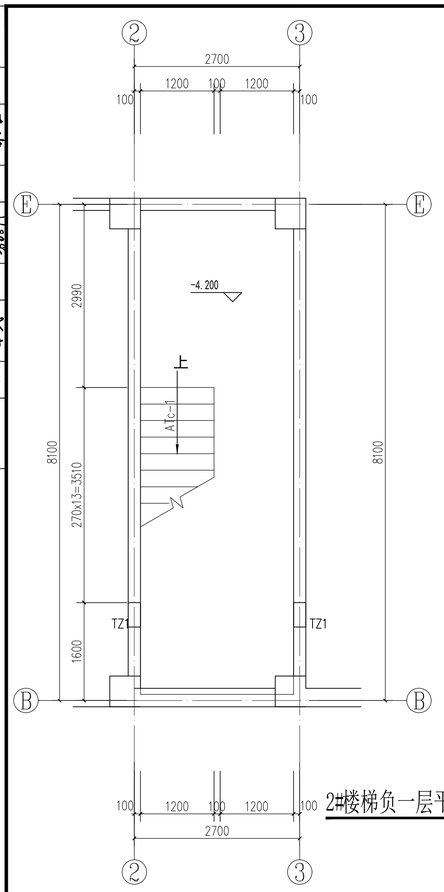



2#楼梯负一层平面图 1:50

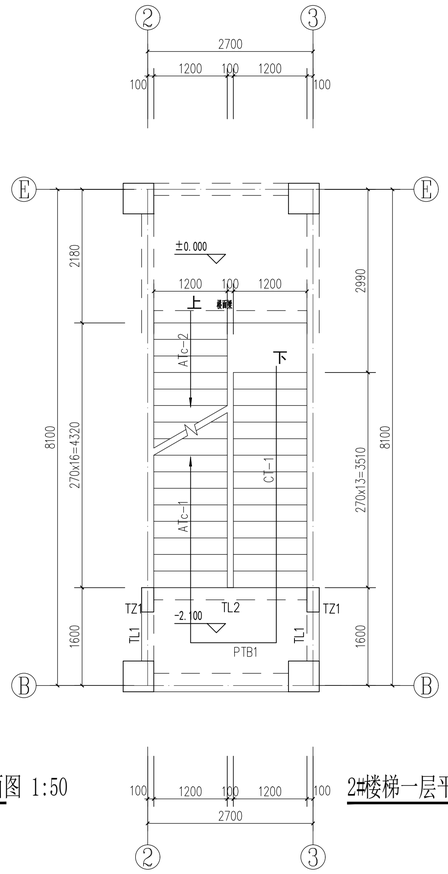



2#楼梯一层平面图 1:50

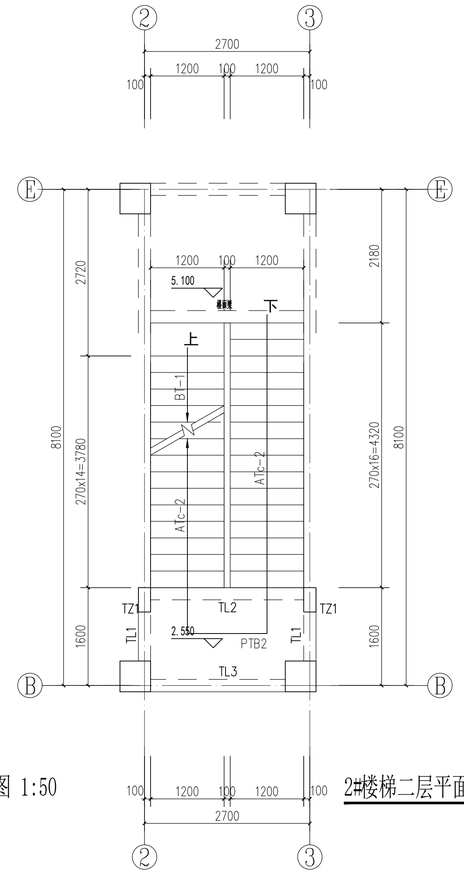




2#楼梯二层平面图 1:50

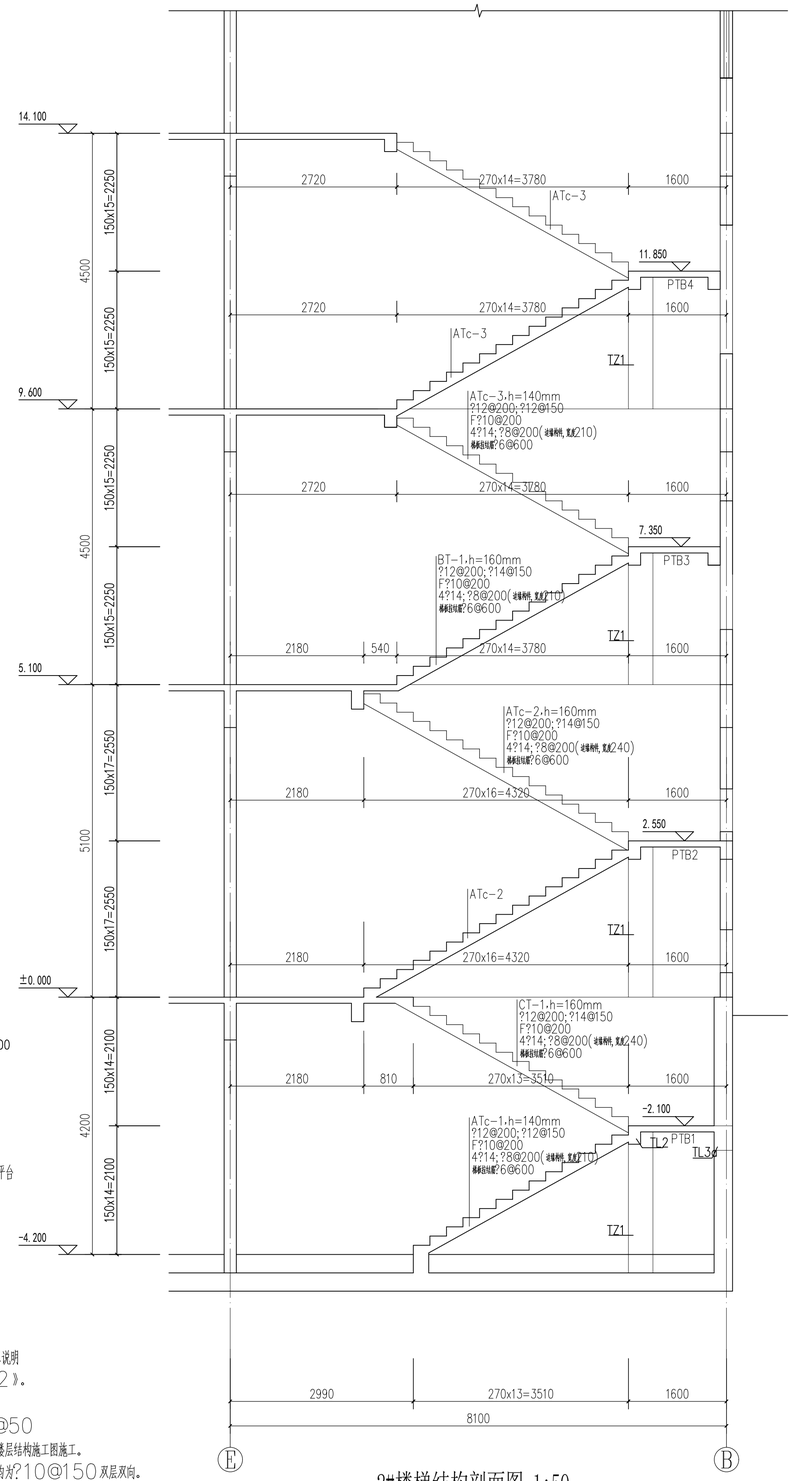



2#楼梯结构剖面图 1:50

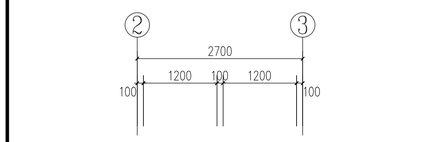

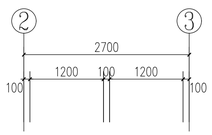


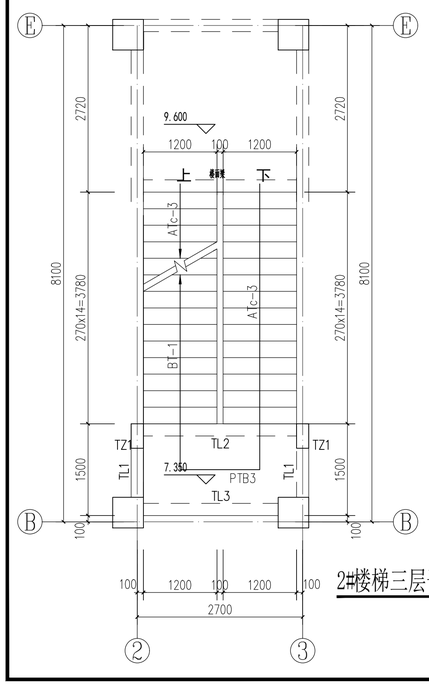
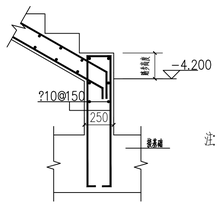


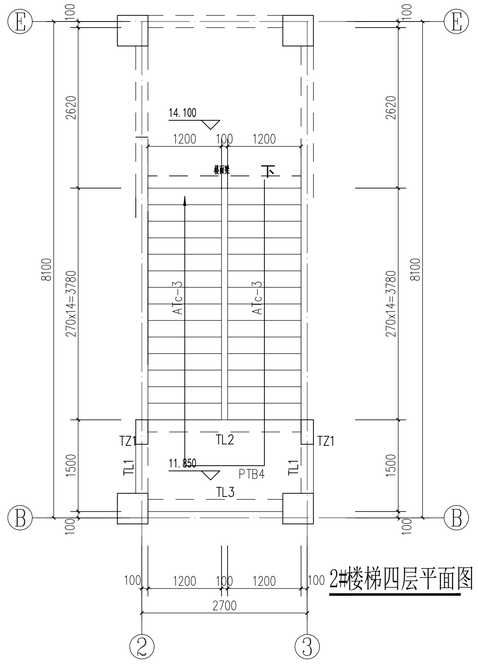

2#楼梯三层平面图 1:50

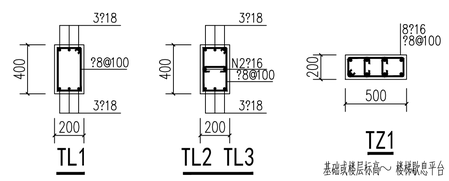


2#楼梯四层平面图 1:50




楼梯一层起步构造

注:
1. 混凝土楼梯施工图平面表示方法和构造详见设计总说明和《国家建筑标准设计图集16G101-2》。
2. 楼梯抗震等级同主体。楼板纵筋通长布置。
3. TZ位置相应架空层KL箍筋每边加密3道@50
4. 楼层处楼梯间范围内楼板的板厚和配筋等按相应楼层结构施工图施工。
5. PTBX板厚均为120mm，配筋均为?10@150双层双向。
6. 本图所注标高为建筑标高，楼梯结构标高=相应建筑标高-50mm。
7. 本图必须与建筑施工图配合使用，确认无矛盾后方可用于施工。

备注栏

设计单位
杭州园林设计院股份有限公司
HANGZHOU LANDSCAPE ARCHITECTURE DESIGN INSTITUTE CO.,LTD
建筑、风景园林甲级:A133013139
规划乙级-城规编(142056)
市政乙级:A233013136
文物保护工程勘察设计乙级:0102SJ0002
公司地址:杭州市西湖区双龙街138号西溪世纪中心5号楼南楼
电话:0571-87031011 传真:0571-87031082 网址:www.hzyly.com

建设单位 江苏茂源电气有限公司

| | |
|---|---|
| 工程总称 | 云创中心生产综合楼 |
| 子项名称 | 生产综合楼 |
| 图纸名称 | 2#楼梯结构 |

| | 姓名 | 签名 |
|---|---|---|
| 审定 | 张永龙 | |
| 审核 | 郑文 | |
| 项目负责人 | 朱君 | |
| 专业负责人 | 高欣 | |
| 设计 | 高欣 | |
| 制图 | 高欣 | |
| 校对 | 罗孝敏 | |

执业专用章

按规定加盖

出图章

未盖出图专用章无效

| | | | |
|---|---|---|---|
| 工号 | 25-14 | 图别 | 结施 |
| 图号 | 24 | 修改版次 | |
| 日期 | 2025.12 | | |

专业会签栏: 园林 建筑 | 结构 给排水 | 电气 暖通 | 弱电